01 现状土地功能分类

Existing mapped land functions

图例 / LEGEND

- 商业商务
- 在建待核实
- 绿地与开敞
- 工业仓储
- 公共管理与服务
- 居住功能
- 交通与停车
- 待核实
- 水域
- 核心设计范围 / Design Site

主要发现 / FINDINGS

- 未知功能保留，非法定用途调查
- 设计线仅标注，不改变22.009km²统计范围

指标与方法 / METHOD

现状功能研究分类；非法定用途。仅映射有证据的面，不用单个POI填满未知地。2023指南参考代码的最新修订未核实。

0 500 1000 m

地块现状与问题

设计区只有21.2%面积有已映射功能依据，低于全域52.3%。当前主要问题是功能底数不完整，无法据图判断未知地块为空置、低效或可直接置换。

区域协同关系

周边500米环带已映射商业、居住和公共服务用地，已知功能覆盖57.6%。设计地块应放在既有居住—就业—服务关系中理解，避免按红线构造自给封闭单元。

改善方向

先核对地块用途、经营状态和开放入口，再沿江场西路、万荣路评估可共享的首层服务与公共空间；以真实需求补短板，形成与周边既有功能的互补。

A3｜1:20,023.81｜EPSG:32651｜设计66.0948ha｜周边　研究区内500米环带；可达比例为步行路段长度，非人口覆盖。

来源沿用原图：© OpenStreetMap contributors / Overture；ESA、Copernicus、EC-JRC、USGS、WorldPop。三段说明区分现状证据与研究建议。

02 建筑密度分析

Building footprint density

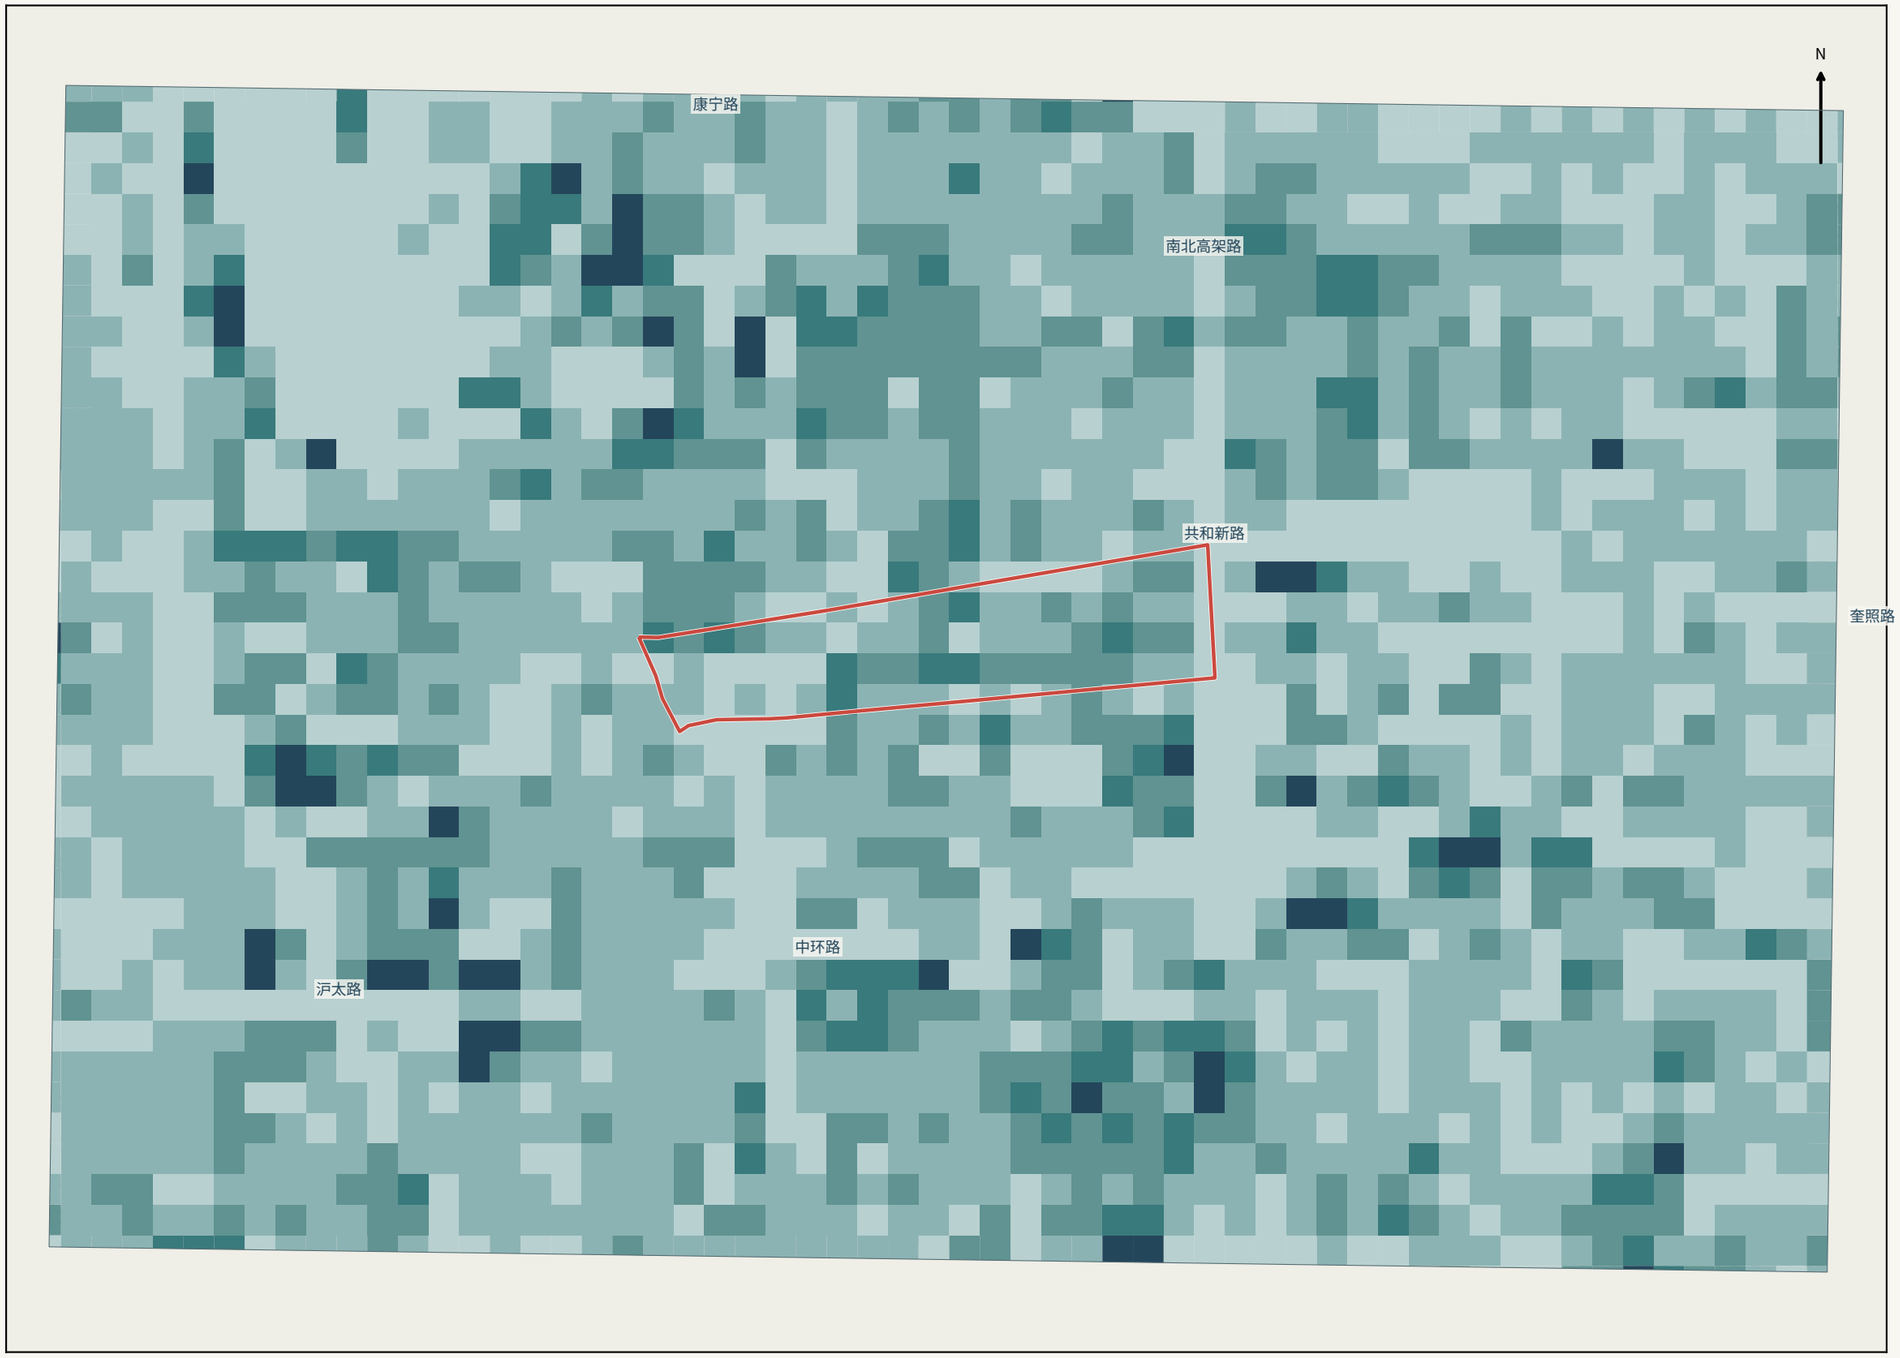

图例 / LEGEND

- 0 – 0.15
- 0.15 – 0.3
- 0.3 – 0.45
- 0.45 – 0.6
- 0.6 – 1
- 核心设计范围 / Design Site

0 500 1000 m

主要发现 / FINDINGS

- 100m真实几何统计；视图内2300个单元
- 有效2300；中位值0.208

指标与方法 / METHOD

建筑占地并集 / 实际单元面积。建筑占地并集面积 / 裁切后500米网格面积；边界网格修正，重叠占地不重复计入。 V3改为100m真实相交重算；设计线仅标注，不改变全域统计口径。

地块现状与问题

建筑轮廓并集覆盖设计区26.6%，高于全域22.6%；触及地块的100米图示单元中，≥45%高值部分约占地块11.0%，内部疏密不均。

区域协同关系

周边环带覆盖率为22.5%。地块需兼顾自身较密集的建筑基底与周边街区连续性，不能仅用全域平均值确定每一处的增减量。

改善方向

优先实查高覆盖单元的日照、消防、院落和通道，沿街道与开敞节点梳理可连通空间；通过局部退让、入口整合和共享院落改善环境，建设强度须另核法定条件。

A3 | 1:20,023.81 | EPSG:32651 | 设计66.0948ha | 周边　研究区内500米环带；可达比例为步行路段长度，非人口覆盖。

来源沿用原图：© OpenStreetMap contributors / Overture；ESA、Copernicus、EC-JRC、USGS、WorldPop。三段说明区分现状证据与研究建议。

03 建筑高度分布｜全部含估算

Building height: source estimates

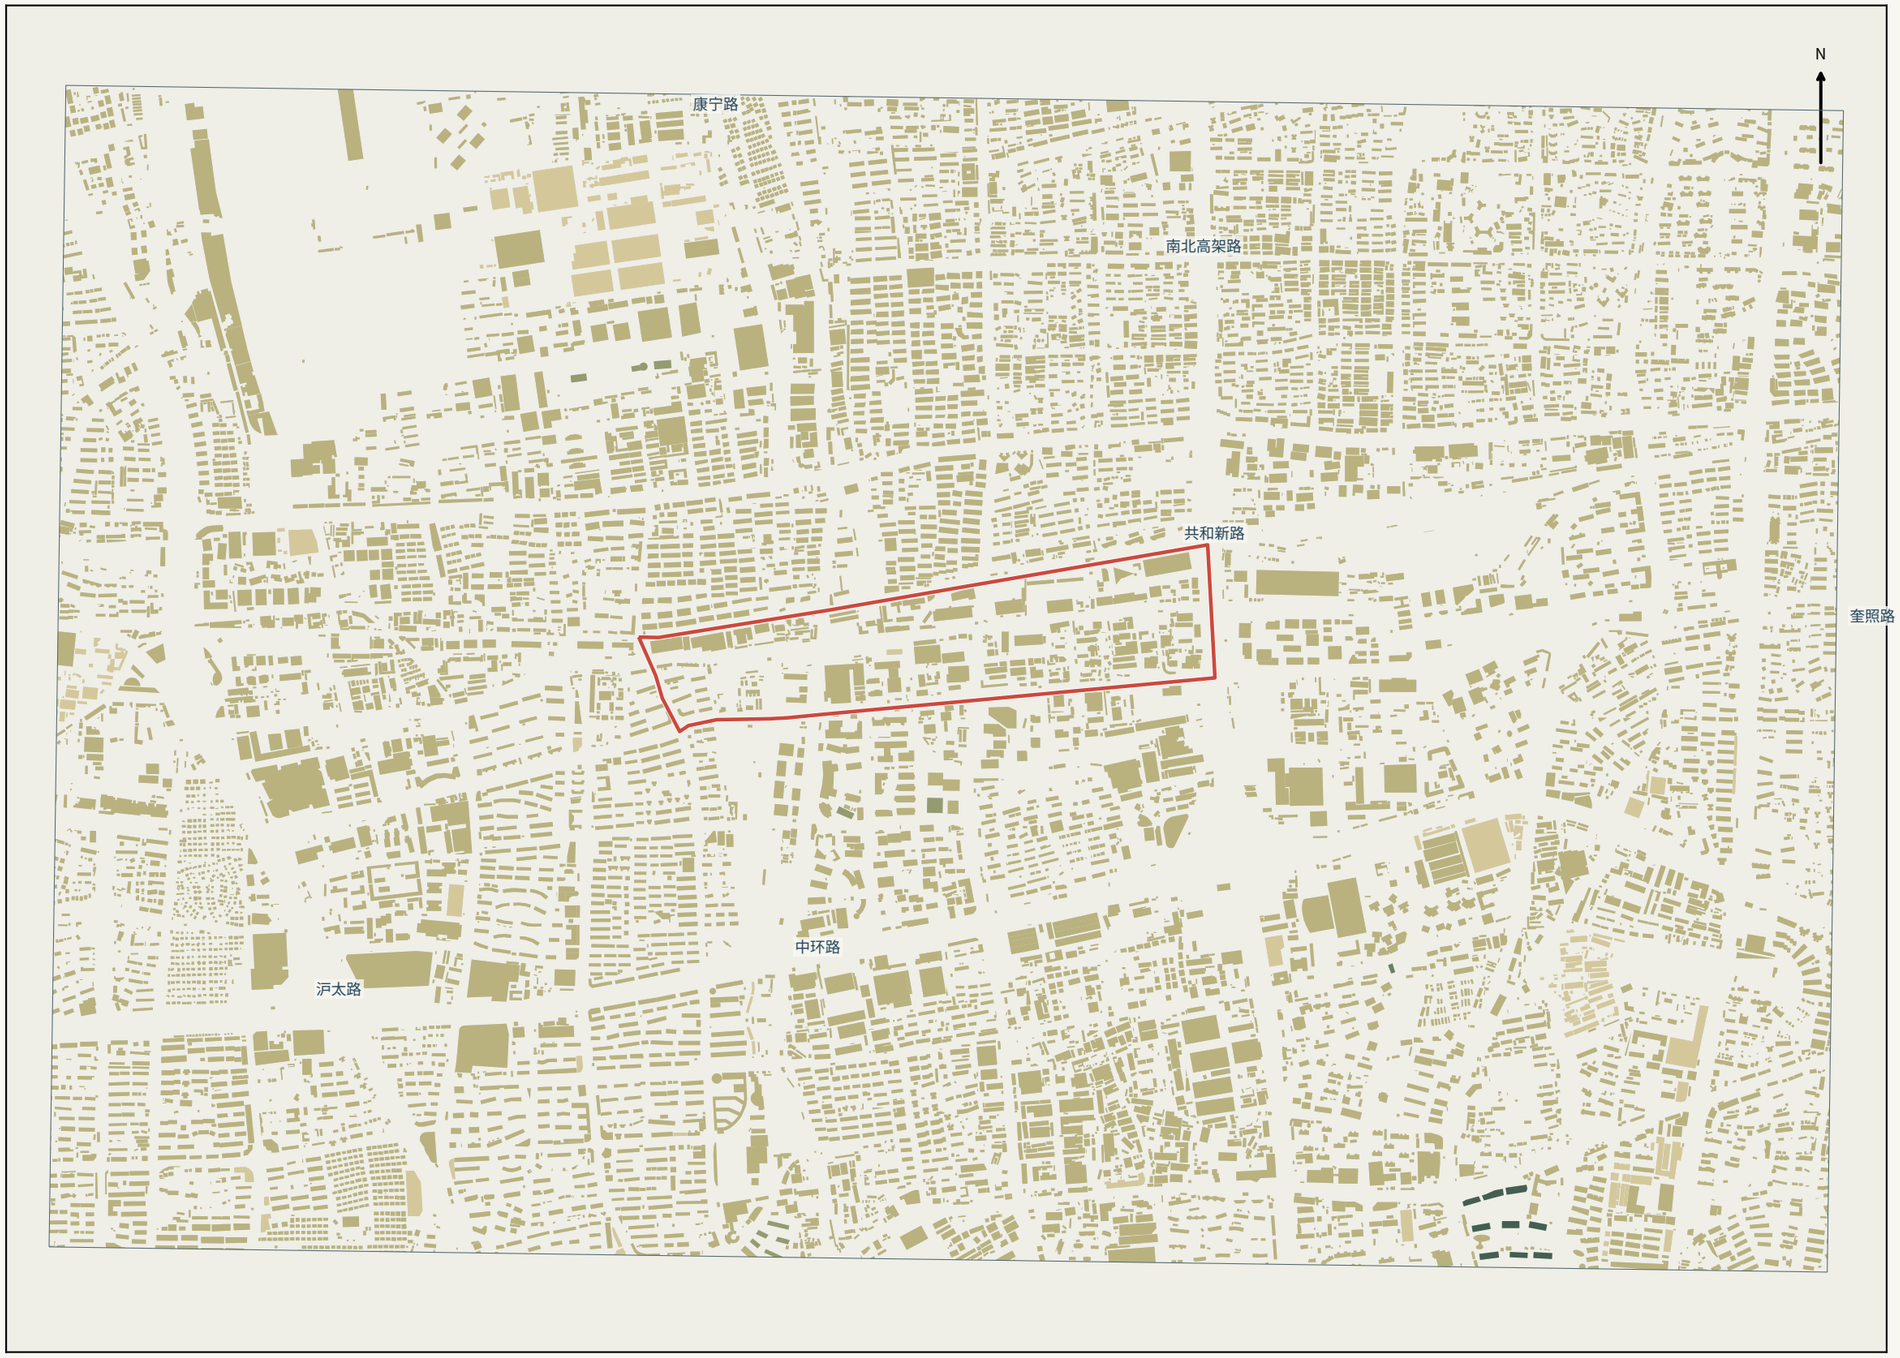

图例 / LEGEND

- 0 – 12
- 12 – 24
- 24 – 54
- 54 – 100
- 100 – 150
- 核心设计范围 / Design Site

0 500 1000 m

主要发现 / FINDINGS

- 11,856个体块；实测高度0
- 11,833默认/上下文估高，23由层数推算

指标与方法 / METHOD

m，全部估计/层数推算。11,856体块均非实测高度：11,833默认/上下文估高，23由层数×3米推算。用于形态研究。

地块现状与问题

设计区相交建筑记录298条，但全部高度来自默认或层数推算。图面高度同质或突变不能作为真实天际线、日照遮挡和高低建筑关系的可靠结论。

区域协同关系

区域高度图可帮助安排建筑复核次序，尚不足以确认地块与周边的高度协调问题。沿江场西路、万荣路和共和新路界面的实际建筑层数与街道断面应统一调查。

改善方向

补测高度、层数、用途和建筑间距后，再研究沿街尺度、重要开敞空间边缘的高度过渡与视线关系；当前保留空间协调议题，不提出具体控高数值。

A3｜1:20,023.81｜EPSG:32651｜设计66.0948ha｜周边　研究区内500米环带；可达比例为步行路段长度，非人口覆盖。

来源沿用原图：© OpenStreetMap contributors / Overture；ESA、Copernicus、EC-JRC、USGS、WorldPop。三段说明区分现状证据与研究建议。

04 建筑体量强度代理

Estimated volume intensity proxy

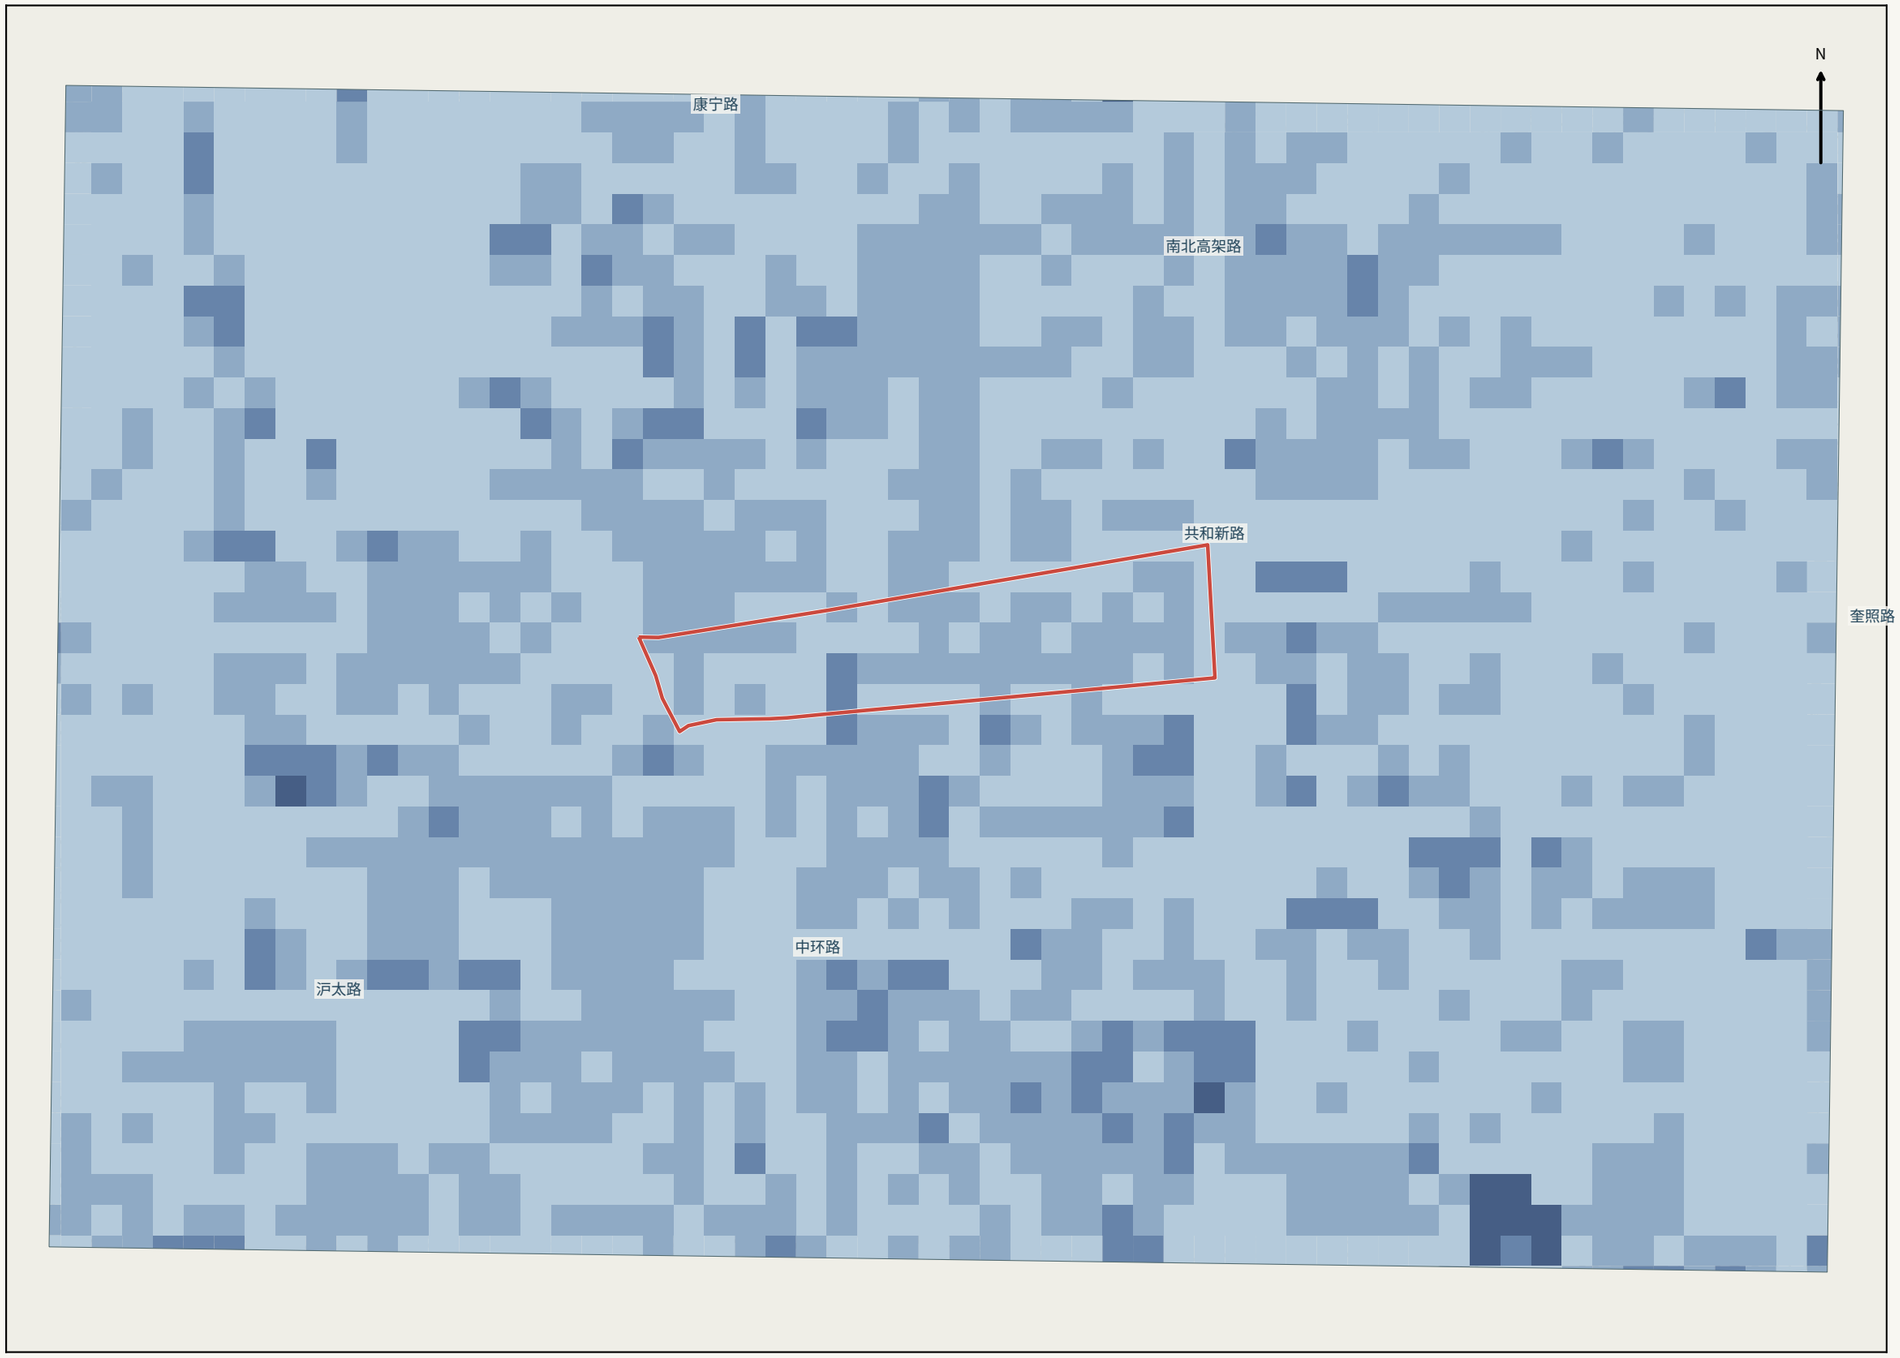

图例 / LEGEND

- 0 – 3
- 3 – 6
- 6 – 12
- 12 – 24
- 24 – 48
- 核心设计范围 / Design Site

0 500 1000 m

主要发现 / FINDINGS

- 100m真实几何统计；视图内2300个单元
- 有效2300；中位值2.59

指标与方法 / METHOD

m^3/m^2，估高体量代理，非容积率。各高度占地互斥面×估算高度之和 / 网格面积（m^3/m^2）。重叠取较高值；不是容积率。V3改为100m真实相交重算；设计线仅标注，不改变全域统计口径。

地块现状与问题

设计区估高体量代理为3.25米³/米²，高于全域2.85；它反映轮廓与估高叠加，不能解释为实测建筑面积、容积率或确定的开发容量。

区域协同关系

周边环带同口径约为2.95米³/米²。地块应结合较高的基底占用，协调内部开放空间与周边街道界面，而非按单一体量指标推导增建任务。

改善方向

先复核建筑真实高度、面积和使用效率，再联动交通承载、日照与公共空间需求比较存量优化方案；新体量应服务于街区关系改善，具体规模另行论证。

A3｜1:20,023.81｜EPSG:32651｜设计66.0948ha｜周边　研究区内500米环带；可达比例为步行路段长度，非人口覆盖。

来源沿用原图：© OpenStreetMap contributors / Overture；ESA、Copernicus、EC-JRC、USGS、WorldPop。三段说明区分现状证据与研究建议。

05 城市肌理与图底关系

Urban figure-ground

0 500 1000 m

图例 / LEGEND

核心设计范围 / Design Site

主要发现 / FINDINGS

- 保留原始建筑几何
- 白地不自动认定为空地或可开发空间

指标与方法 / METHOD

现有建筑真实来源轮廓的图底表达；不表示产权、竣工状态或完整测绘。

地块现状与问题

设计区建筑基底覆盖26.6%，其余图底白地包含道路、水面、院落及未分类空间，不能直接视为可建设用地。痛点在于需要辨明开敞空间是否真正连续、开放和可进入。

区域协同关系

江场西路、万荣路等通道穿联地块与周边街区。图底关系应同时检查沿街连续界面和跨边界步行联系，而不是只优化红线内部的形式构图。

改善方向

逐处核对围墙、门禁与通道，优先连接合法开放的院落和街角空间；在有权属及安全条件的界面补足步行联系，保留必要的生产、后勤与消防空间。

A3｜1:20,023.81｜EPSG:32651｜设计66.0948ha｜周边　研究区内500米环带；可达比例为步行路段长度，非人口覆盖。

来源沿用原图：© OpenStreetMap contributors / Overture；ESA、Copernicus、EC-JRC、USGS、WorldPop。三段说明区分现状证据与研究建议。

06 已映射土地功能面积混合度

Mapped land-function area diversity

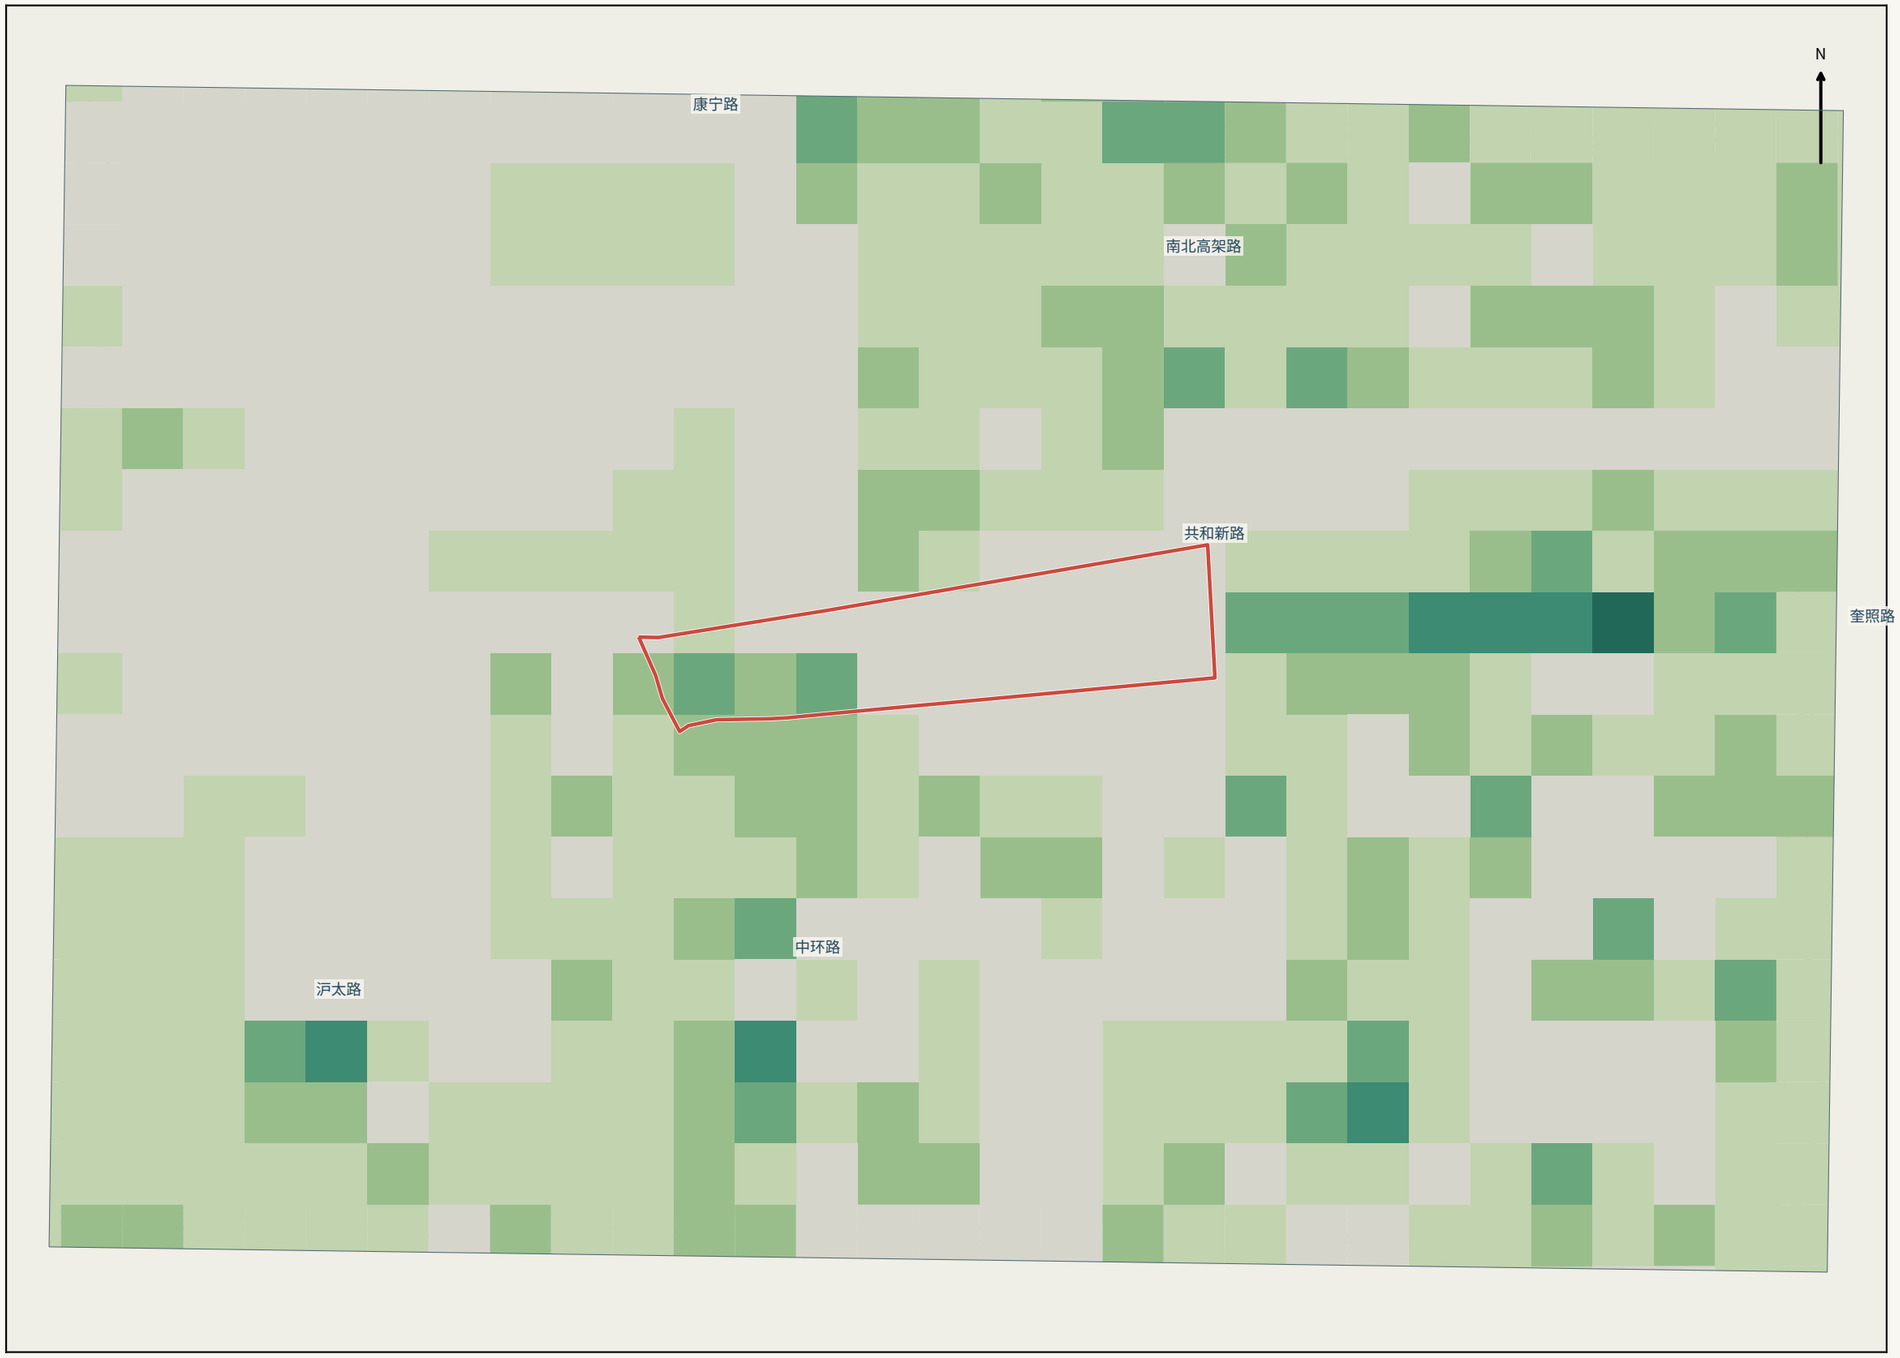

0 500 1000 m

图例 / LEGEND

- 0 – 0.2
- 0.2 – 0.4
- 0.4 – 0.6
- 0.6 – 0.8
- 0.8 – 1
- 资料/有效覆盖不足，未计算
- 核心设计范围 / Design Site

主要发现 / FINDINGS

• 200m真实几何统计；视图内600个单元

• 有效343；中位值0.0985

•
全域已知功能占比仍约52.33%；低覆盖单元不计算

指标与方法 / METHOD

H(已映射功能面积)/ln(8)；已知功能比例≥50%。200m；按已映射功能面面积计算H/ln(8)，未知不入确定用途；已知功能面积比例不足50%不计算。与V2的POI熵是不同指标。

地块现状与问题

设计区已知功能面积仅21.2%；触及地块的29个200米图示单元中，只有10个有有效混合度值。低覆盖空值不能被解释为单一功能或缺乏活力。

区域协同关系

全域功能证据覆盖52.3%，周边环带为57.6%。应核查地块与周边居住、商业及公共服务之间的使用联系，避免因数据详略不同误判功能差距。

改善方向

开展首层用途、经营时间与人群活动调查，先补齐混合功能证据；再选择合适街道节点引入互补服务及可分时共享空间，不以提高熵值本身作为设计目标。

A3｜1:20,023.81｜EPSG:32651｜设计66.0948ha｜周边　研究区内500米环带；可达比例为步行路段长度，非人口覆盖。

来源沿用原图：© OpenStreetMap contributors / Overture；ESA、Copernicus、EC-JRC、USGS、WorldPop。三段说明区分现状证据与研究建议。

07 道路等级与交通结构

Road hierarchy and grade separation

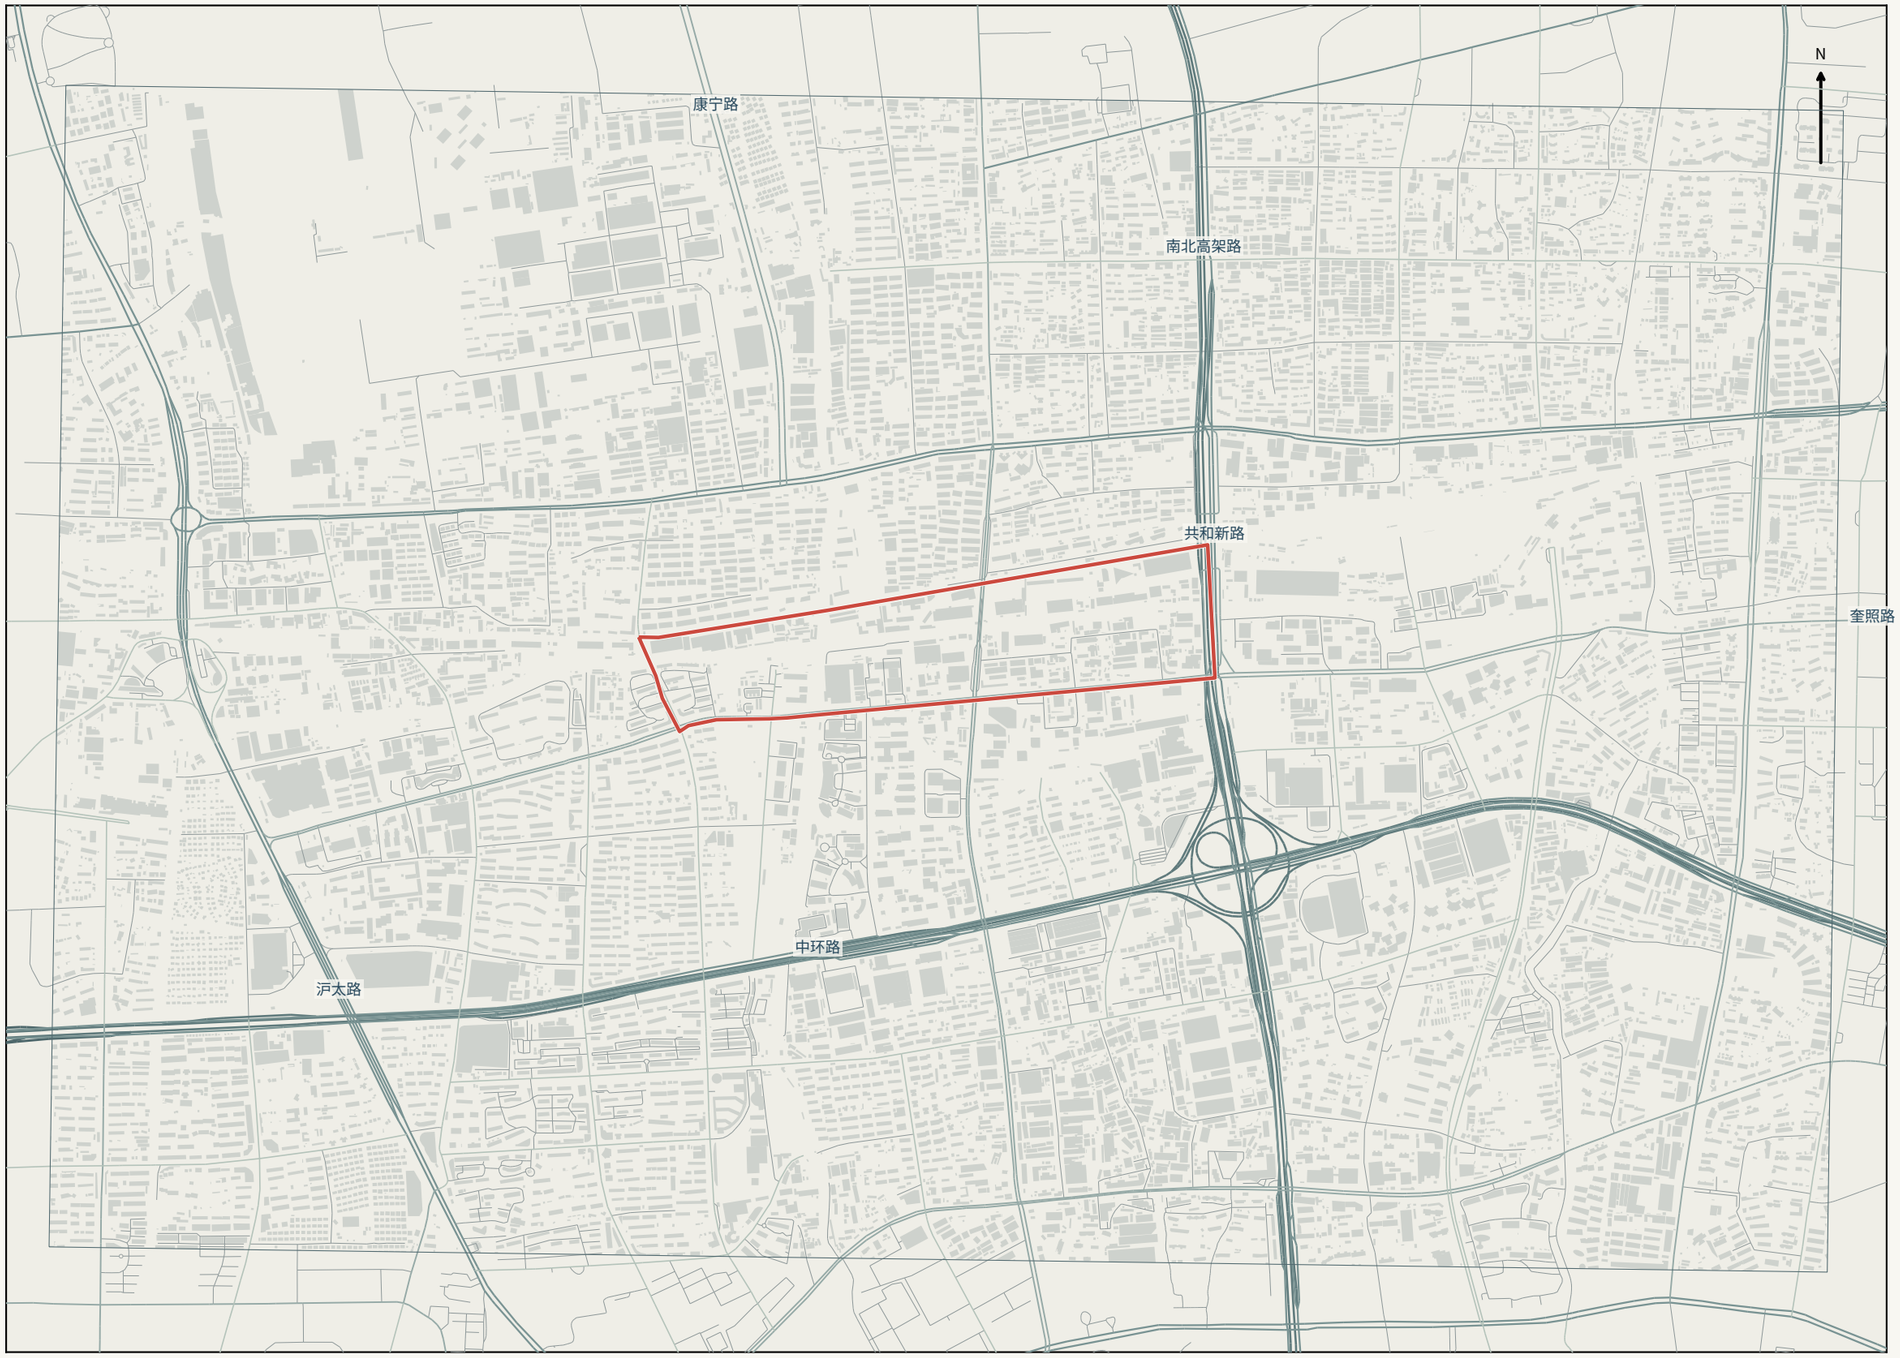

0 500 1000 m

图例 / LEGEND

- motorway
- trunk
- primary
- secondary
- tertiary
- 核心设计范围 / Design Site

主要发现 / FINDINGS

- 道路几何与等级标签沿用V2
- 层级、桥隧和真实节点拓扑保留

指标与方法 / METHOD

保留源等级、桥隧、层级和单行属性；几何相交不自动连通。不是官方道路行政等级。

地块现状与问题

设计区记录约9.19公里车行源线，包含江场西路、万荣路及南北高架路等层级。线网存在不等于地面步行可穿越，高架与主路界面是需优先核对的衔接位置。

区域协同关系

全域共和新路、场中路等承担跨片区联系；地块需区分区域通行、片区集散和内部到达，避免将区域道路负担简单转入内部生活空间。

改善方向

核实车流、出入口、过街条件与高架下空间，组织清晰的到达层级、连续人行与后勤路线；改善方向以安全接入和街道协同为先，不凭模型新增道路。

A3｜1:20,023.81｜EPSG:32651｜设计66.0948ha｜周边　研究区内500米环带；可达比例为步行路段长度，非人口覆盖。

来源沿用原图：© OpenStreetMap contributors / Overture；ESA、Copernicus、EC-JRC、USGS、WorldPop。三段说明区分现状证据与研究建议。

08 车行路网密度与节点连通

Mapped vehicle network density

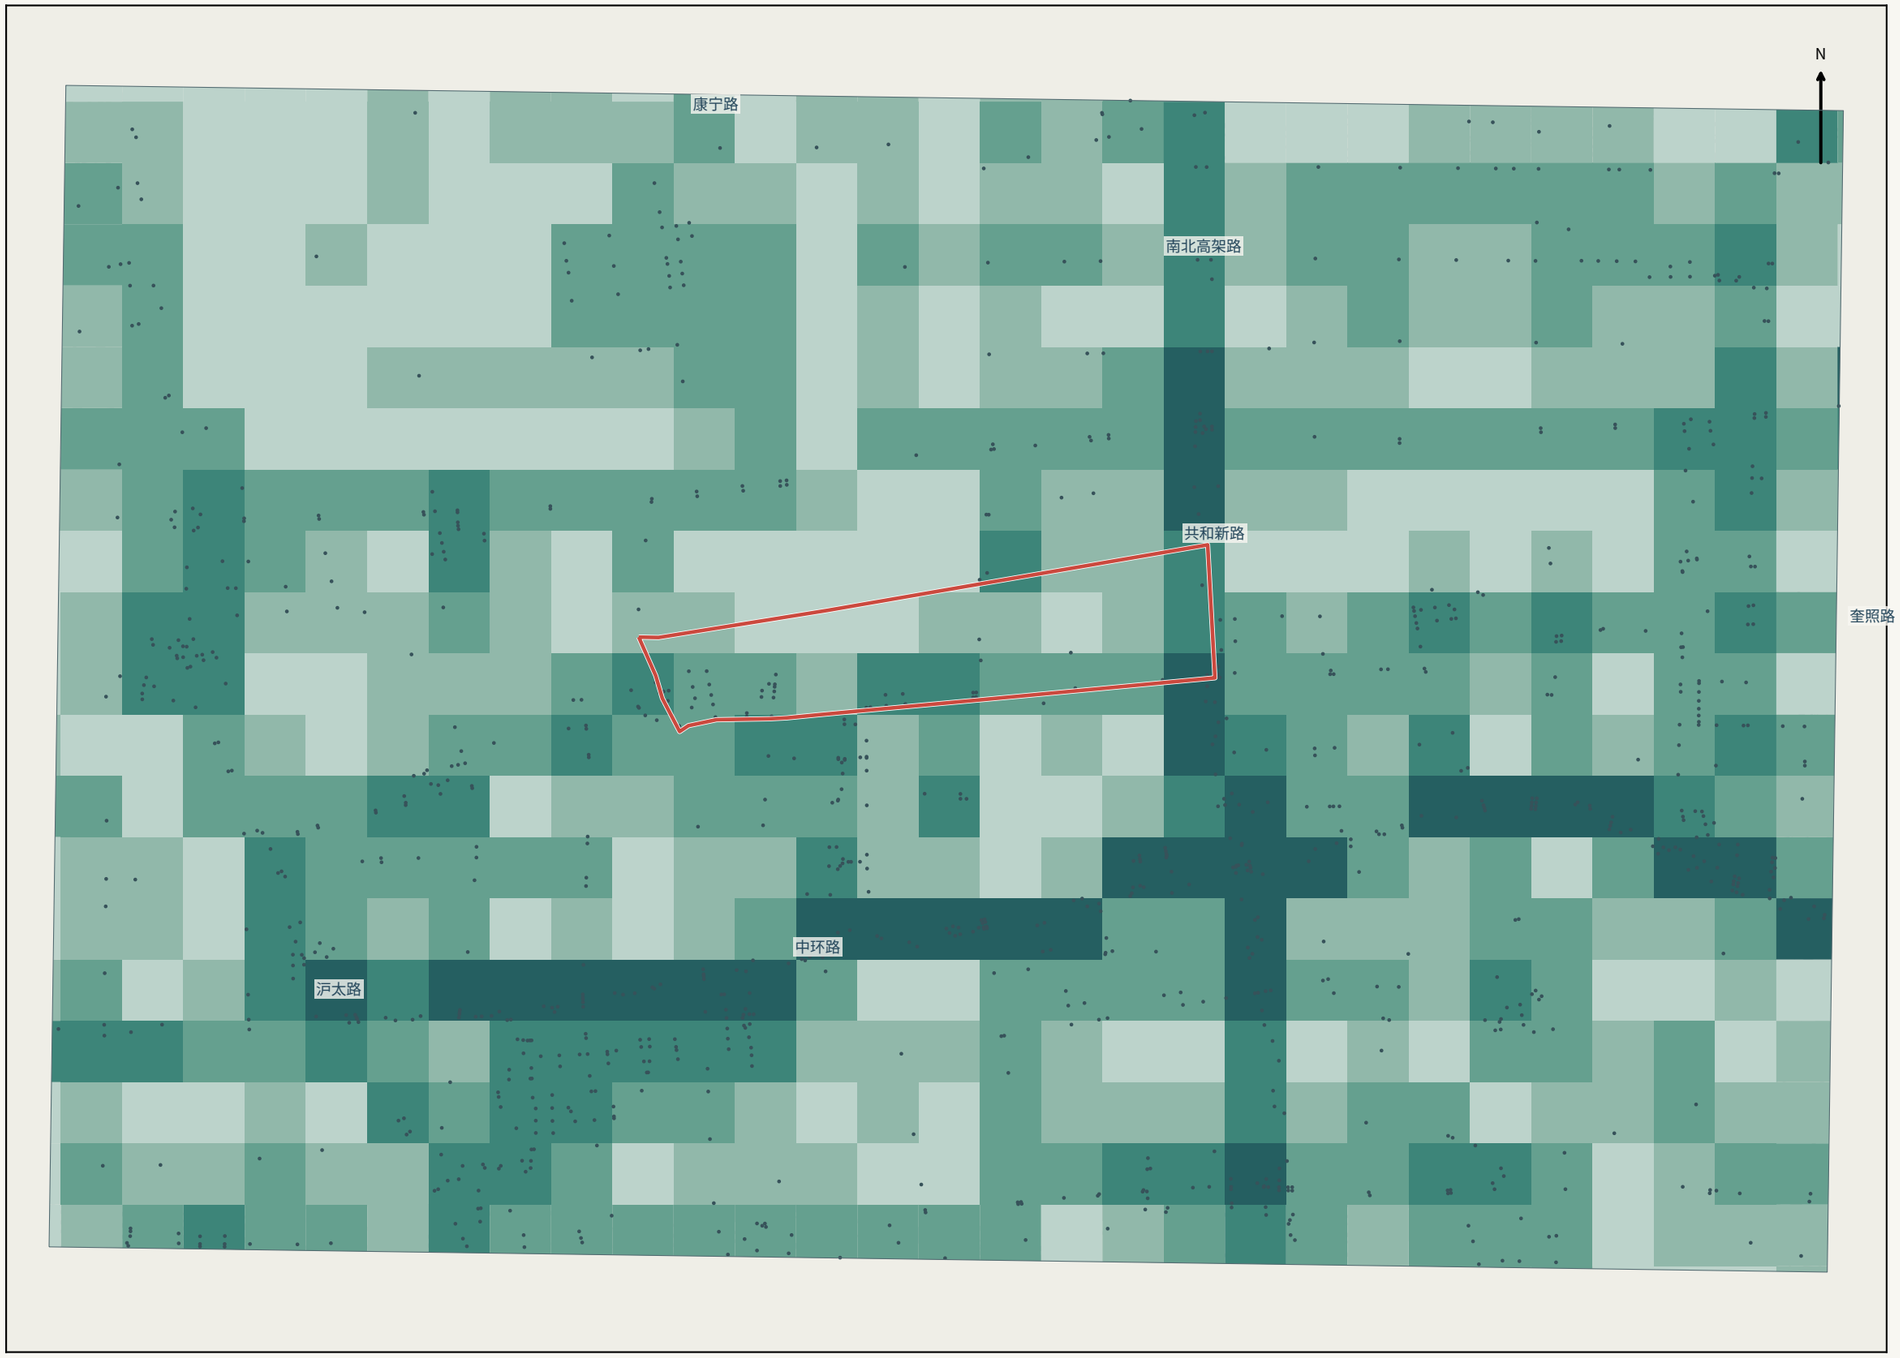

图例 / LEGEND

- 0 – 5
- 5 – 10
- 10 – 20
- 20 – 35
- 35 – 73
- 真实源节点车行度≥3
- 核心设计范围 / Design Site

0 500 1000 m

主要发现 / FINDINGS

- 200m真实几何统计；视图内600个单元
- 有效600；中位值9.48

指标与方法 / METHOD

km / km²，双幅源道路分计。200m；源线km/实际单元km²，双幅分计。叠加真实源节点度≥3的车行路口，桥隧几何交叉不增节点。

地块现状与问题

设计区车行源线密度13.90公里/平方公里、真实源节点48处；密度高于全域12.16，不能据此直接认定交通畅通或过街便捷。

区域协同关系

邻近环带密度12.31。区域与地块更需共同处理路口衔接、分层道路和边界通行，而非单纯追求更密集的中心线。

改善方向

围绕江场西路—万荣路等实际路口复核转向、行人等待与无障碍衔接，优先改善关键节点；新增连接需核实权属、交通影响及真实通行条件。

A3｜1:20,023.81｜EPSG:32651｜设计66.0948ha｜周边　研究区内500米环带；可达比例为步行路段长度，非人口覆盖。
来源沿用原图：© OpenStreetMap contributors / Overture；ESA、Copernicus、EC-JRC、USGS、WorldPop。三段说明区分现状证据与研究建议。

09 公共交通接入与步行网络覆盖

Transit access on mapped walk network

0 500 1000 m

图例 / LEGEND

- 15分钟已映射可达路段
- 10分钟已映射可达路段
- 5分钟已映射可达路段
- 核心设计范围 / Design Site

主要发现 / FINDINGS

- 复用V2真实源节点步行分析，4.5km/h
- 设施接入和门禁不确定性保留；非人口覆盖率

指标与方法 / METHOD

5/10/15分钟，4.5km/h最短路径。站台/出入口/停靠点记录不是独立车站或班次；仅合格接入点进入计算。

地块现状与问题

按已映射步行网络，设计区83.3%的路段长度可在5分钟内接入已记录公交节点，10分钟为99.9%。总体接入基础较好，不能将其写成居民覆盖率或运力充足结论。

区域协同关系

全域5分钟同口径为80.2%。可结合源标注的江场西路原平路等公交节点，组织由周边公共交通进入地块的连续步行界面，而不重复建设封闭接驳体系。

改善方向

实查站台、道路两侧过街、入口开放时间与无障碍设施，把“最后一段”接入纳入地块和道路的联合设计；班次、客流和站点承载另以运营资料校核。

A3｜1:20,023.81｜EPSG:32651｜设计66.0948ha｜周边　研究区内500米环带；可达比例为步行路段长度，非人口覆盖。

来源沿用原图：© OpenStreetMap contributors / Overture；ESA、Copernicus、EC-JRC、USGS、WorldPop。三段说明区分现状证据与研究建议。

10 日常服务慢行可达性

Daily-service walking reach

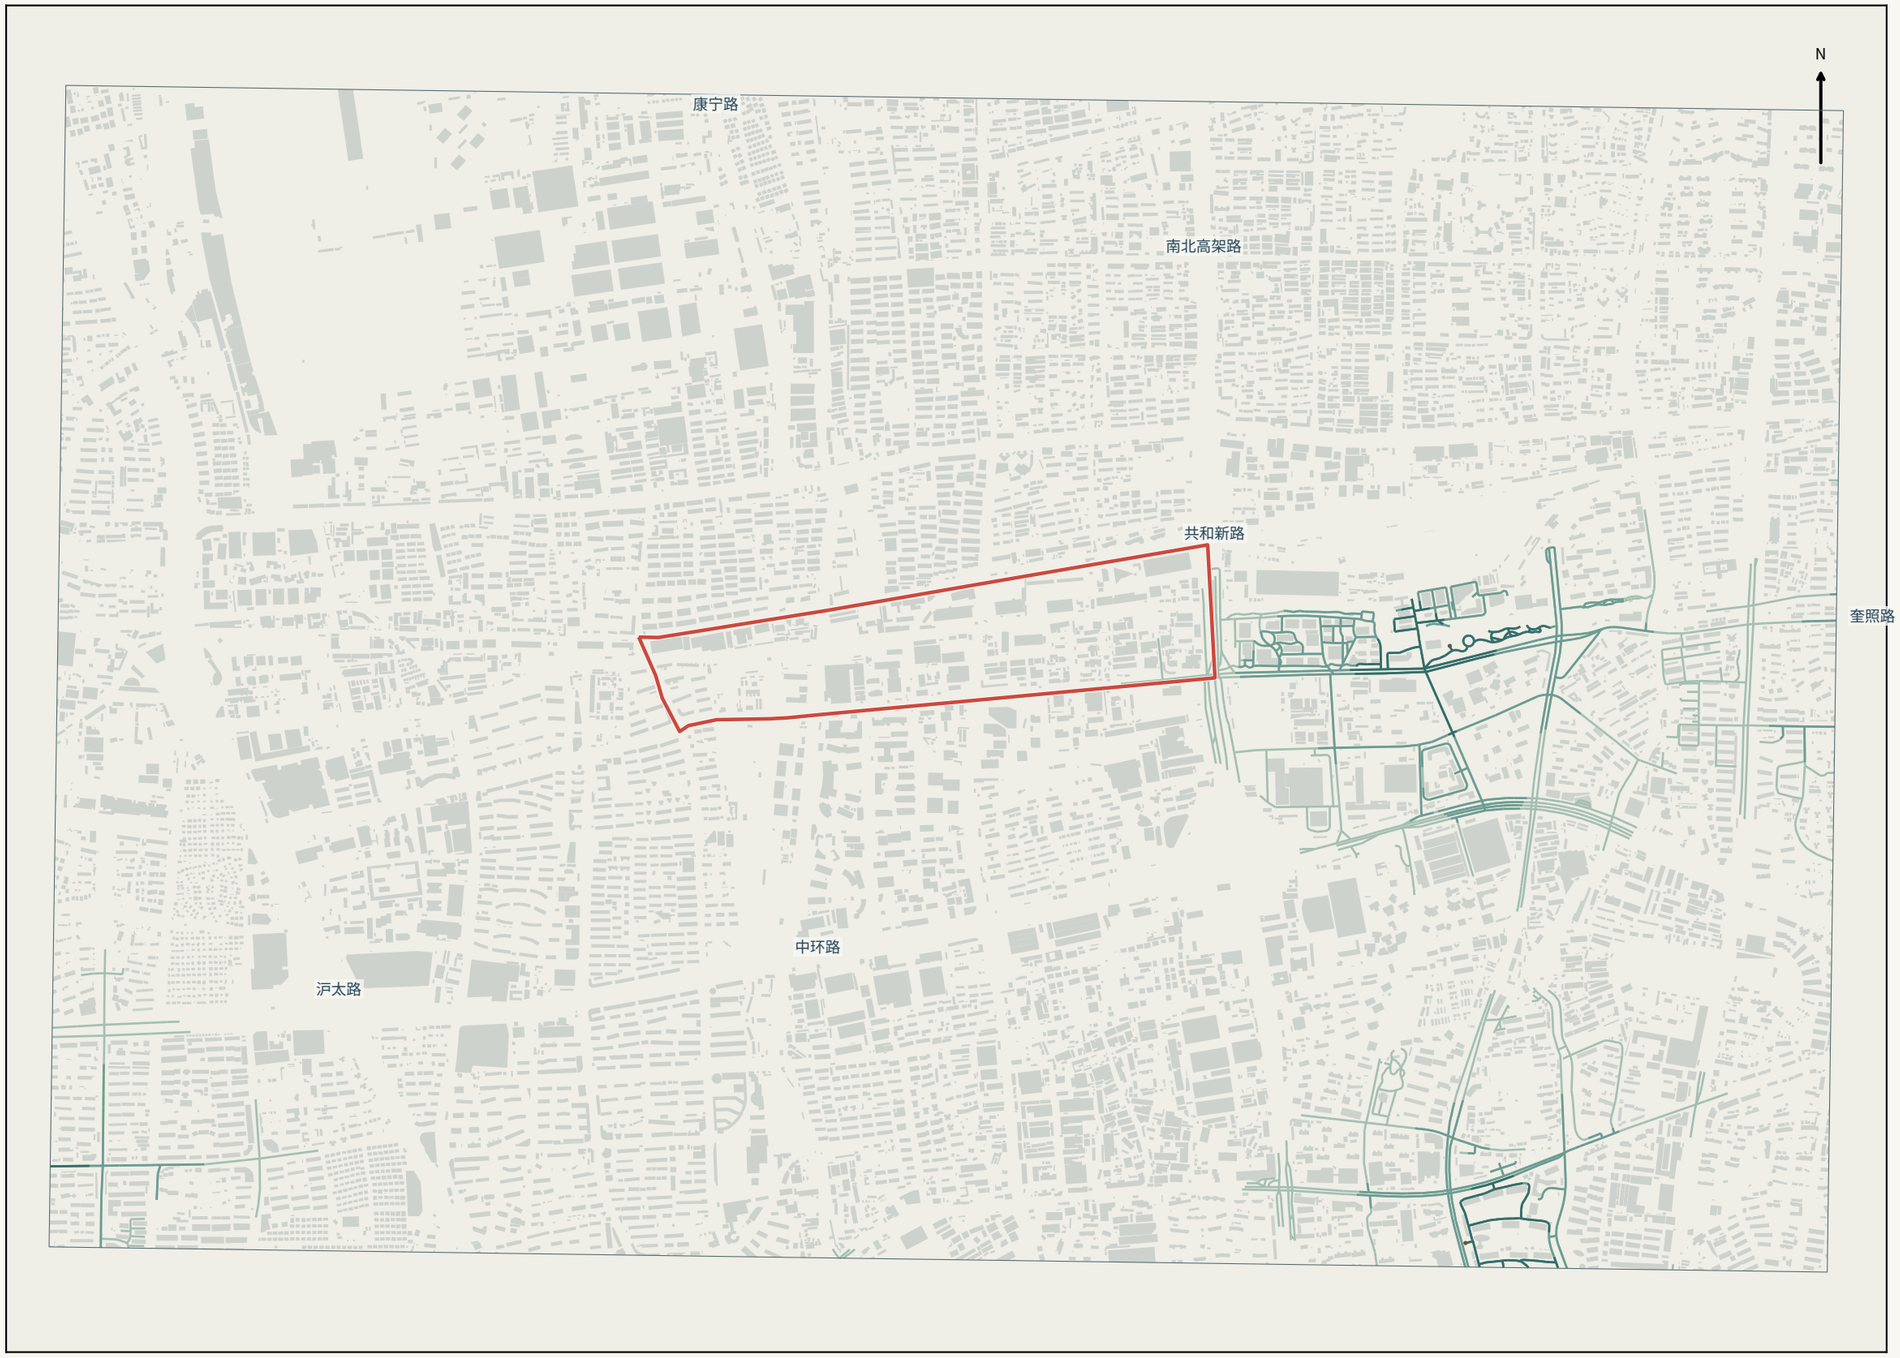

0 500 1000 m

图例 / LEGEND

- 15分钟已映射可达路段
- 10分钟已映射可达路段
- 5分钟已映射可达路段
- 核心设计范围 / Design Site

主要发现 / FINDINGS

- 复用V2真实源节点步行分析，4.5km/h
- 设施接入和门禁不确定性保留；非人口覆盖率

指标与方法 / METHOD

基于OSM步行节点和已映射设施，5/10/15分钟；结果为可达路段，不是欧氏圈或服务人口比例。

地块现状与问题

已记录日常服务的15分钟可达路段占设计区步行网10.1%，低于全域18.5%。但全域该类观察点仅29条，现图首先显示记录接入偏弱，不能证明真实服务缺失。

区域协同关系

应把地块与江场西路、万荣路及周边居住片区的服务网共同核对，区分“已有服务但入口难达”与“实际需求未被满足”，避免在红线内机械配齐全部功能。

改善方向

补查便利商业、餐饮及社区服务清单、开放时间和真实需求；若短板被证实，优先在公共路径交汇处配置可面向周边使用的小尺度服务，并同步改善步行接入。

A3｜1:20,023.81｜EPSG:32651｜设计66.0948ha｜周边　研究区内500米环带；可达比例为步行路段长度，非人口覆盖。
来源沿用原图：© OpenStreetMap contributors / Overture；ESA、Copernicus、EC-JRC、USGS、WorldPop。三段说明区分现状证据与研究建议。

11 商业POI观察密度

Mapped commercial POI observations

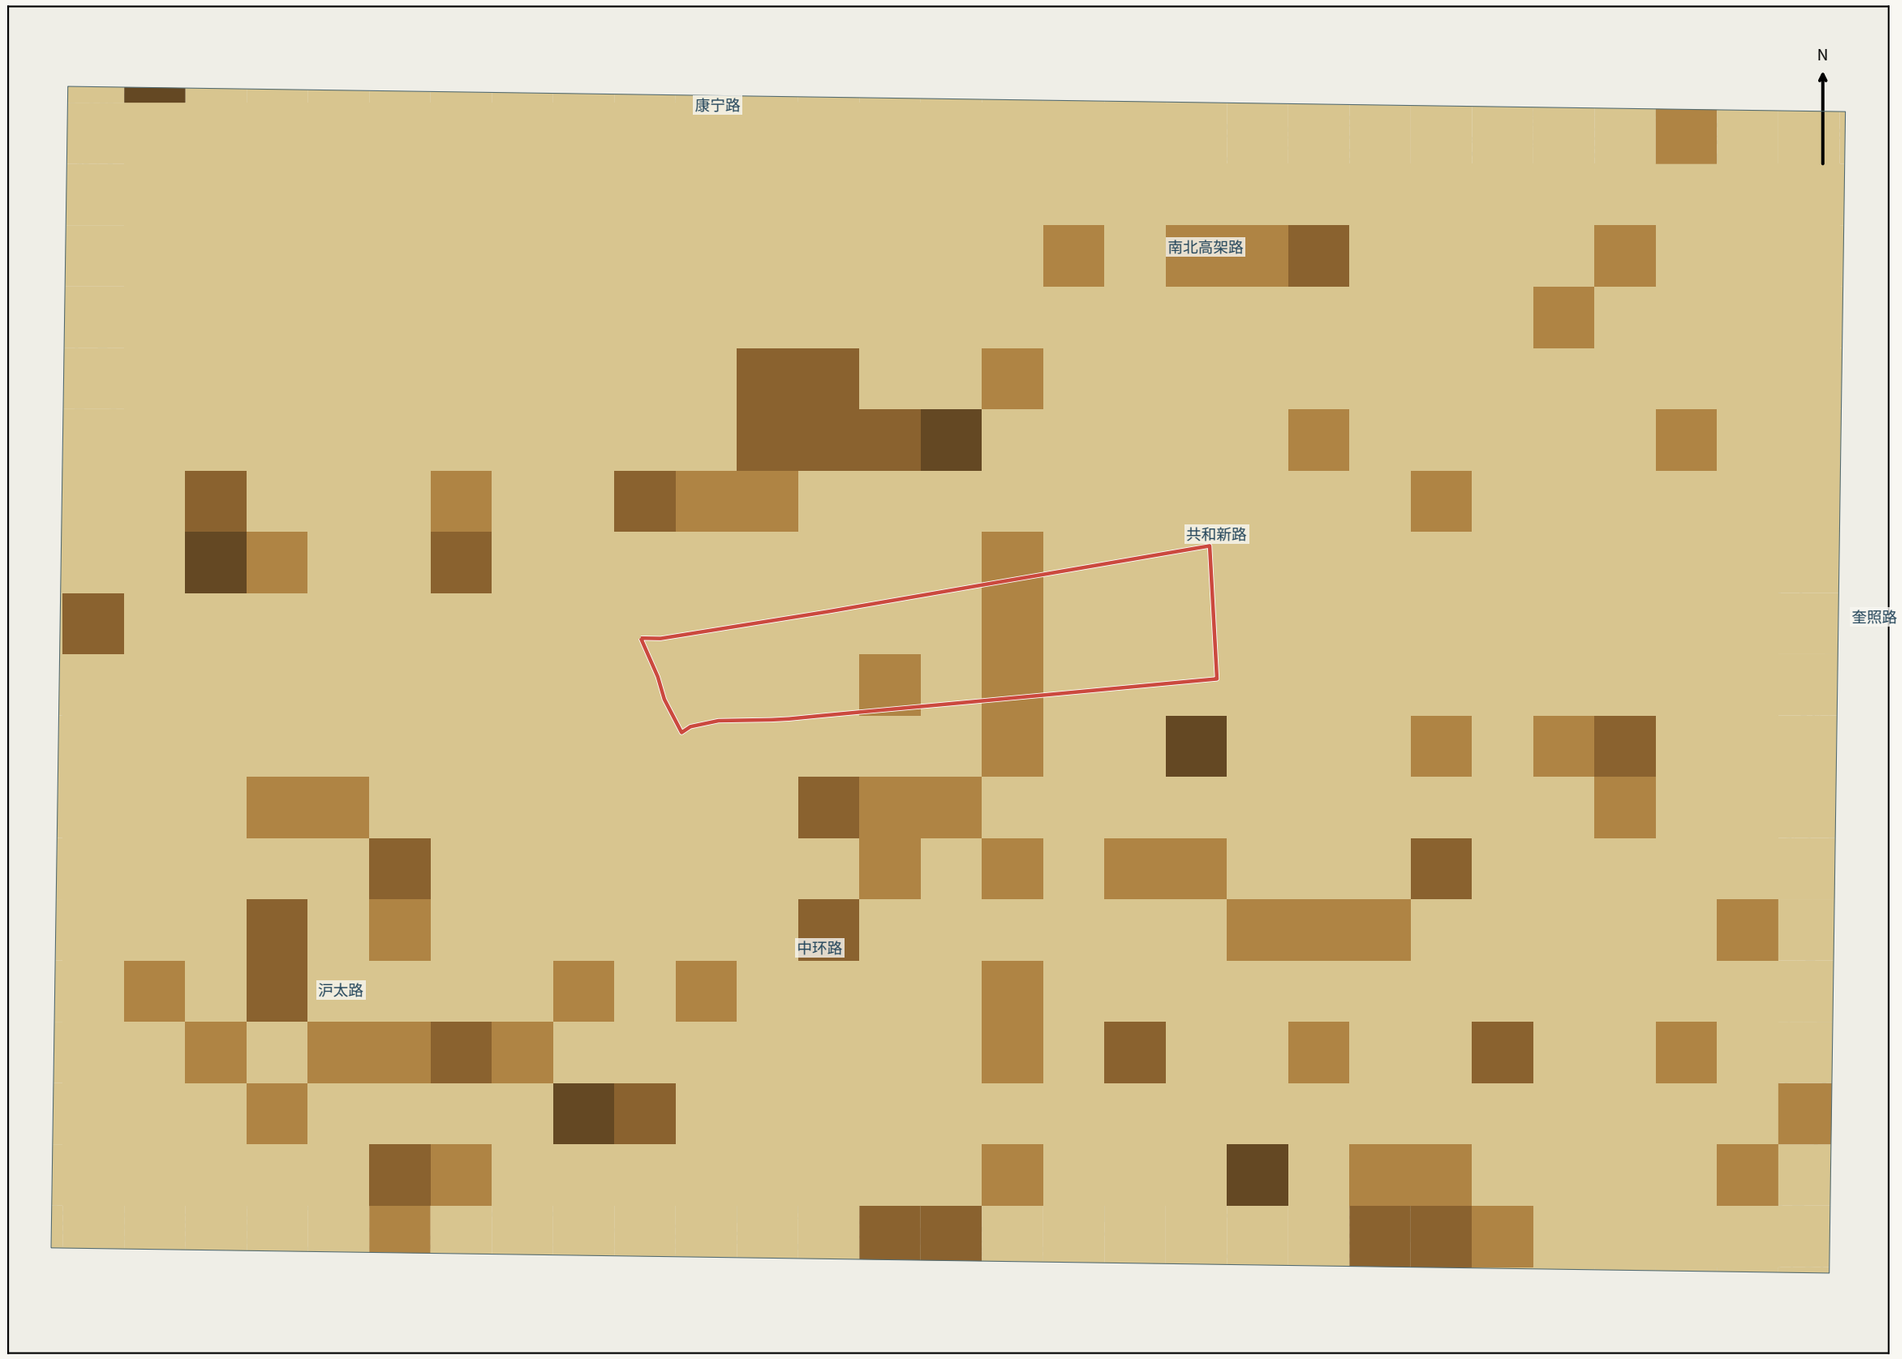

图例 / LEGEND

- 0 – 10
- 10 – 25
- 25 – 50
- 50 – 100
- 100 – 250
- 核心设计范围 / Design Site

主要发现 / FINDINGS

- 200m真实几何统计；视图内600个单元
- 有效600；中位值0

指标与方法 / METHOD

已映射商业POI / km^2；零值不表示无商业。200m网格；真实观测点数/裁切单元面积（POI/km^2），零值不表示无商业。KDE100/200/400m仅作敏感性对照，不代表客流。

0 500 1000 m

地块现状与问题

设计区只有2条商业观察点，周边500米环带有24条。记录稀疏不能解释为无商业、低消费需求或确定的商业空白地段。

区域协同关系

商业组织应结合江场西路与万荣路的人行联系、周边既有商业和居住需求，研究地块首层服务的互补角色，而非按POI热度复制区域商业中心。

改善方向

实查店铺、空置、营业时段与实际客流，识别可接续的服务街段；优先利用适宜的沿街首层和共享节点试点经营，规模及业态待需求和运营验证后确定。

A3｜1:20,023.81｜EPSG:32651｜设计66.0948ha｜周边　研究区内500米环带；可达比例为步行路段长度，非人口覆盖。

来源沿用原图：© OpenStreetMap contributors / Overture；ESA、Copernicus、EC-JRC、USGS、WorldPop。三段说明区分现状证据与研究建议。

12 已映射教育设施步行覆盖

Mapped education walking access

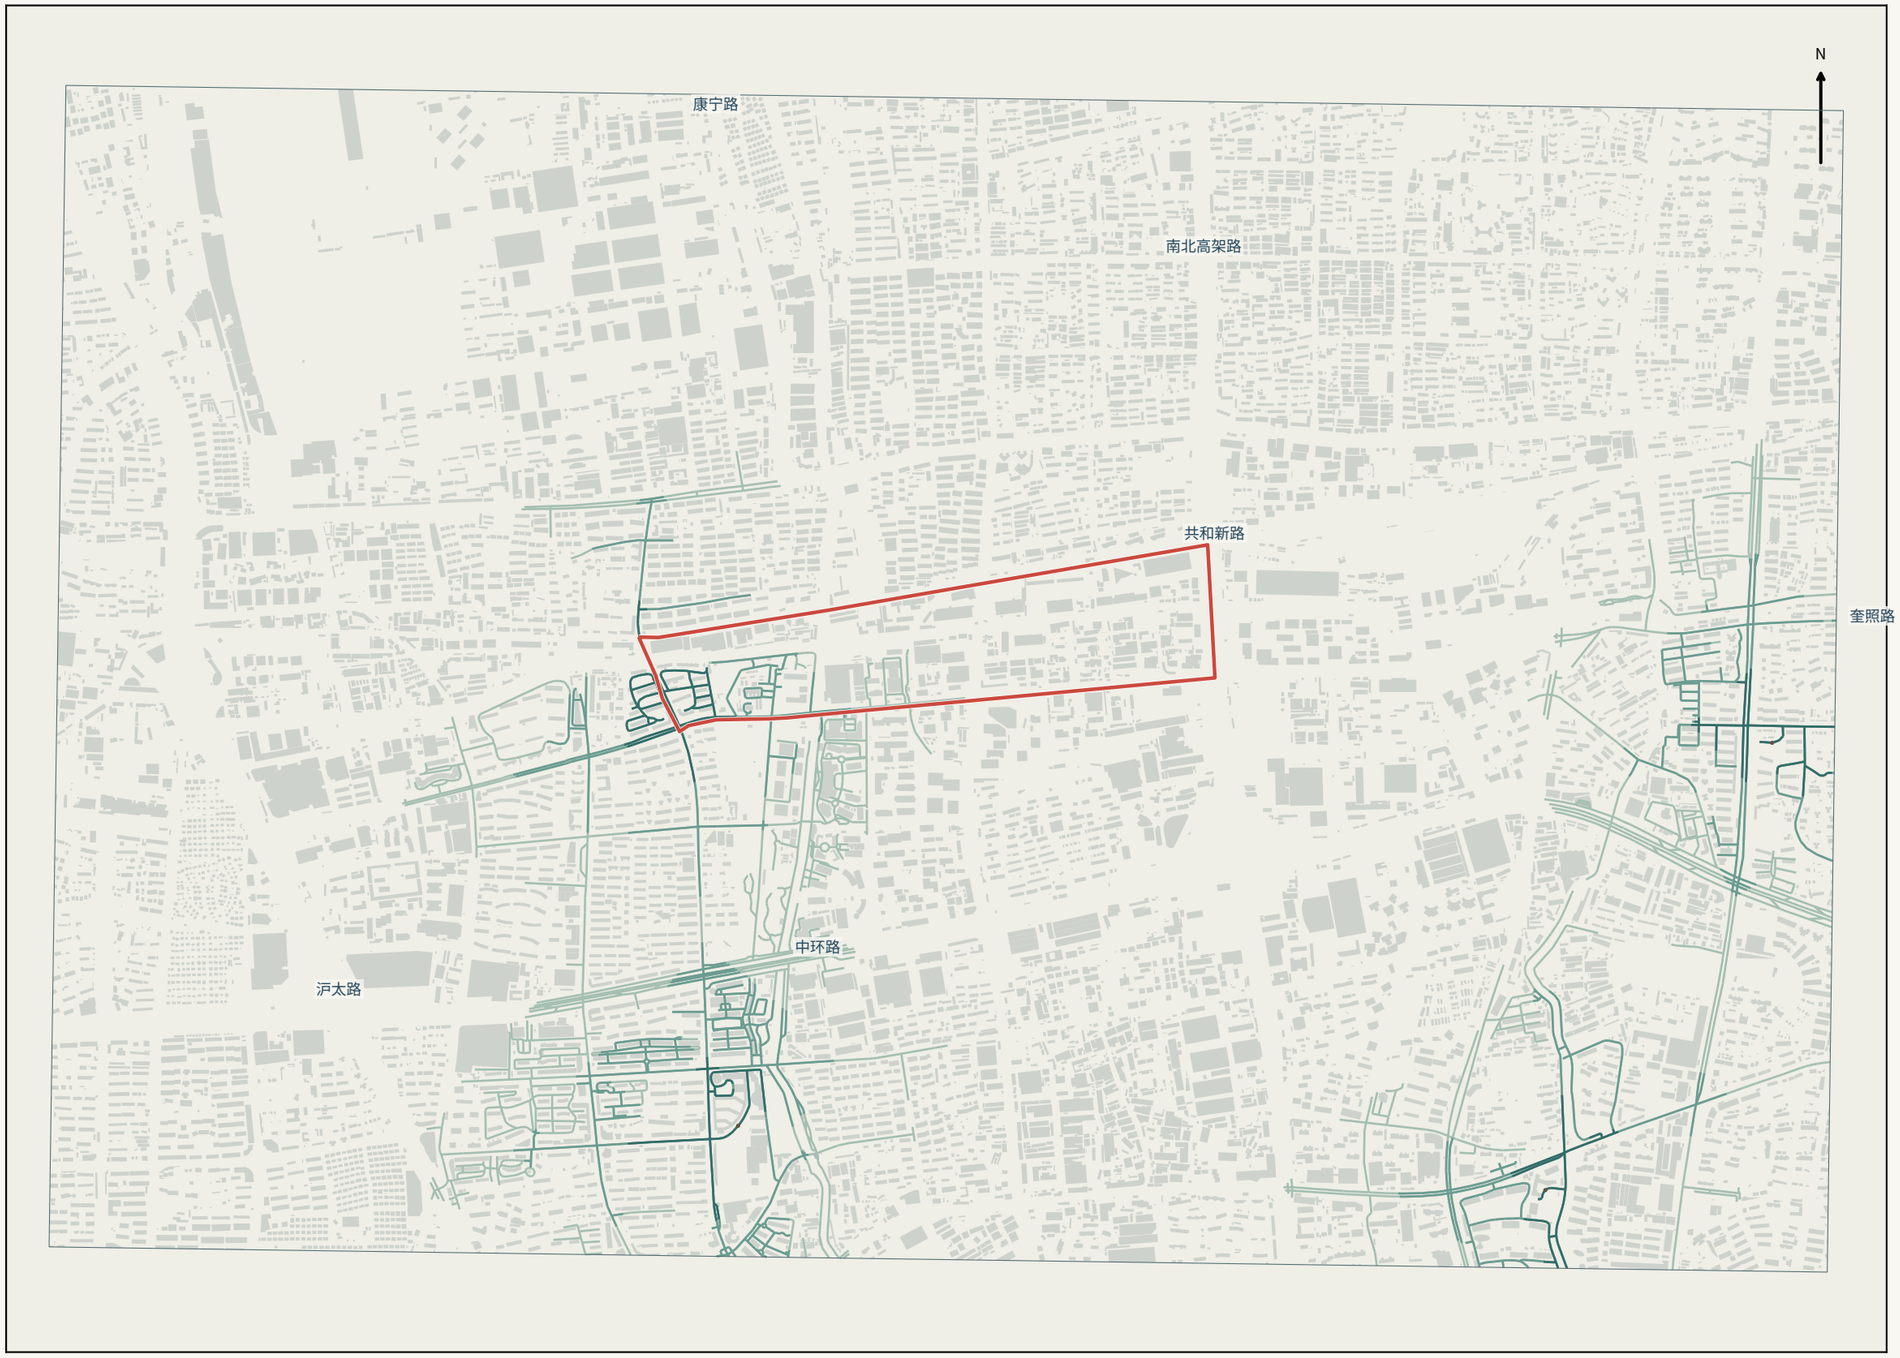

0 500 1000 m

图例 / LEGEND

- 15分钟已映射可达路段
- 10分钟已映射可达路段
- 5分钟已映射可达路段
- 核心设计范围 / Design Site

主要发现 / FINDINGS

- 复用V2真实源节点步行分析，4.5km/h
- 设施接入和门禁不确定性保留；非人口覆盖率

指标与方法 / METHOD

公共服务分项之一：教育。只计算能接入真实路网的设施；无床位、等级或容量推断。其它分项见数据库和覆盖表。

地块现状与问题

设计区没有教育POI记录，但已有教育节点的15分钟步行可达路段占比为51.1%。这表明不能以红线内点位为空就认定缺校，图中也不包含学位容量和入学资格。

区域协同关系

周边环带有8条教育设施记录，包括源标注的田家炳小学、永和小学等。地块可协调周边学校的接入环境，是否共享场地须由学校与管理条件确认。

改善方向

联合核查校门位置、接送流线、交通冲突、通学安全及设施容量，优先改善地块至周边教育资源的连续步行路线；不凭可达线网判断学位是否满足。

A3｜1:20,023.81｜EPSG:32651｜设计66.0948ha｜周边　研究区内500米环带；可达比例为步行路段长度，非人口覆盖。
来源沿用原图：© OpenStreetMap contributors / Overture；ESA、Copernicus、EC-JRC、USGS、WorldPop。三段说明区分现状证据与研究建议。

13 蓝绿空间现状网络

Mapped blue and green spaces

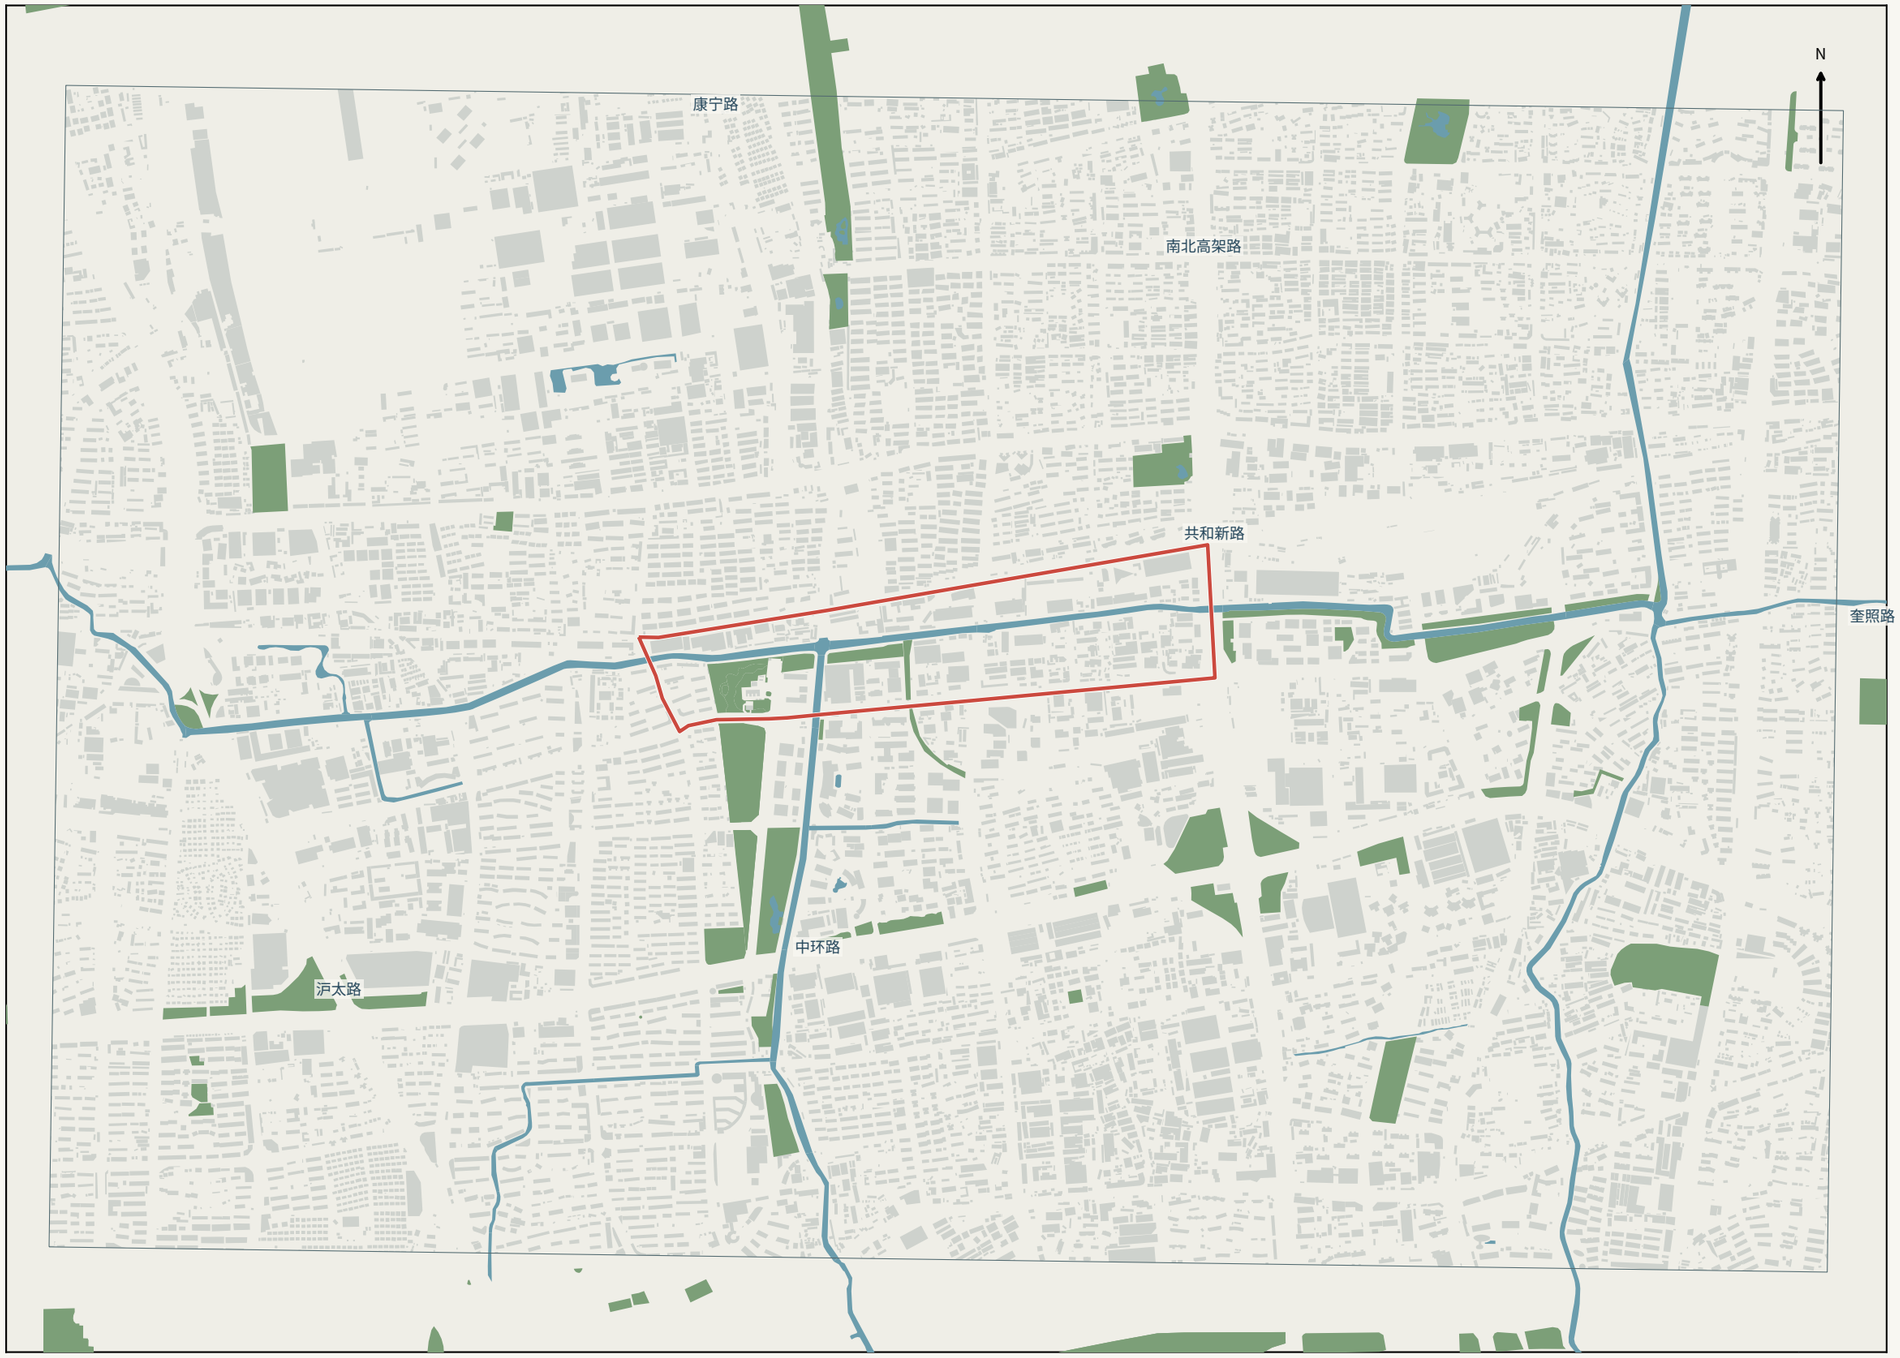

图例 / LEGEND

- 已映射绿色空间
- 已映射水面
- 核心设计范围 / Design Site

主要发现 / FINDINGS

- 开放性不等于绿量
- 不将已映射面积称为官方绿化率

指标与方法 / METHOD

绿地与水面为开放地图观察；不等同官方绿化覆盖率，不自动认定全部开放。

地块现状与问题

设计区已映射绿地约6.6%、水面约6.8%；全域同口径分别为2.9%和1.4%。资源相对集中，但图面不能证明岸线开放、生态质量或公共可用性。

区域协同关系

可把地块水绿界面与周边半里绿廊、彭浦公园及静安青年体育公园等资源作为协同研究对象，重点核查连续路径、入口和道路阻隔，而非把各绿块孤立布置。

改善方向

优先保护已有水绿资源，补查河道管理、岸线安全、绿地权属和开放时段；在条件允许处接续遮荫步道、街角绿地与滨水节点，形成对周边居民可用的空间网络。

A3｜1:20,023.81｜EPSG:32651｜设计66.0948ha｜周边　研究区内500米环带；可达比例为步行路段长度，非人口覆盖。

来源沿用原图：© OpenStreetMap contributors / Overture；ESA、Copernicus、EC-JRC、USGS、WorldPop。三段说明区分现状证据与研究建议。

14 公园绿地网络可达性

Park access on mapped walking network

图例 / LEGEND

- 15分钟已映射可达路段
- 10分钟已映射可达路段
- 5分钟已映射可达路段
- 核心设计范围 / Design Site

0 500 1000 m

主要发现 / FINDINGS

- 复用V2真实源节点步行分析，4.5km/h
- 设施接入和门禁不确定性保留；非人口覆盖率

指标与方法 / METHOD

源步道真实穿越公园边界处的近似接入（端点≤20m），排除明确私有/禁入；开放时间和门禁未实地核实。

地块现状与问题

已映射公园节点5分钟可达路段占设计区步行网53.3%，10分钟为99.7%。接近绿地的优势较明显，但图中不反映入口真实性、场地容量、开放时段与活动设施质量。

区域协同关系

全域5分钟同口径为24.9%，邻近环带为44.3%。地块可作为衔接周边公园与街区的节点，发挥资源协同作用，而非只增加内部绿化面积。

改善方向

核实彭浦公园、青年体育公园及近邻绿廊的真实接入口，接续可公开通行的步道；根据实际人群需求补充休憩、健身和无障碍设施，避免重复设置同质空间。

A3｜1:20,023.81｜EPSG:32651｜设计66.0948ha｜周边　研究区内500米环带；可达比例为步行路段长度，非人口覆盖。

来源沿用原图：© OpenStreetMap contributors / Overture；ESA、Copernicus、EC-JRC、USGS、WorldPop。三段说明区分现状证据与研究建议。

15 公共环境改善机会研究初筛

Research screening for amenity improvement

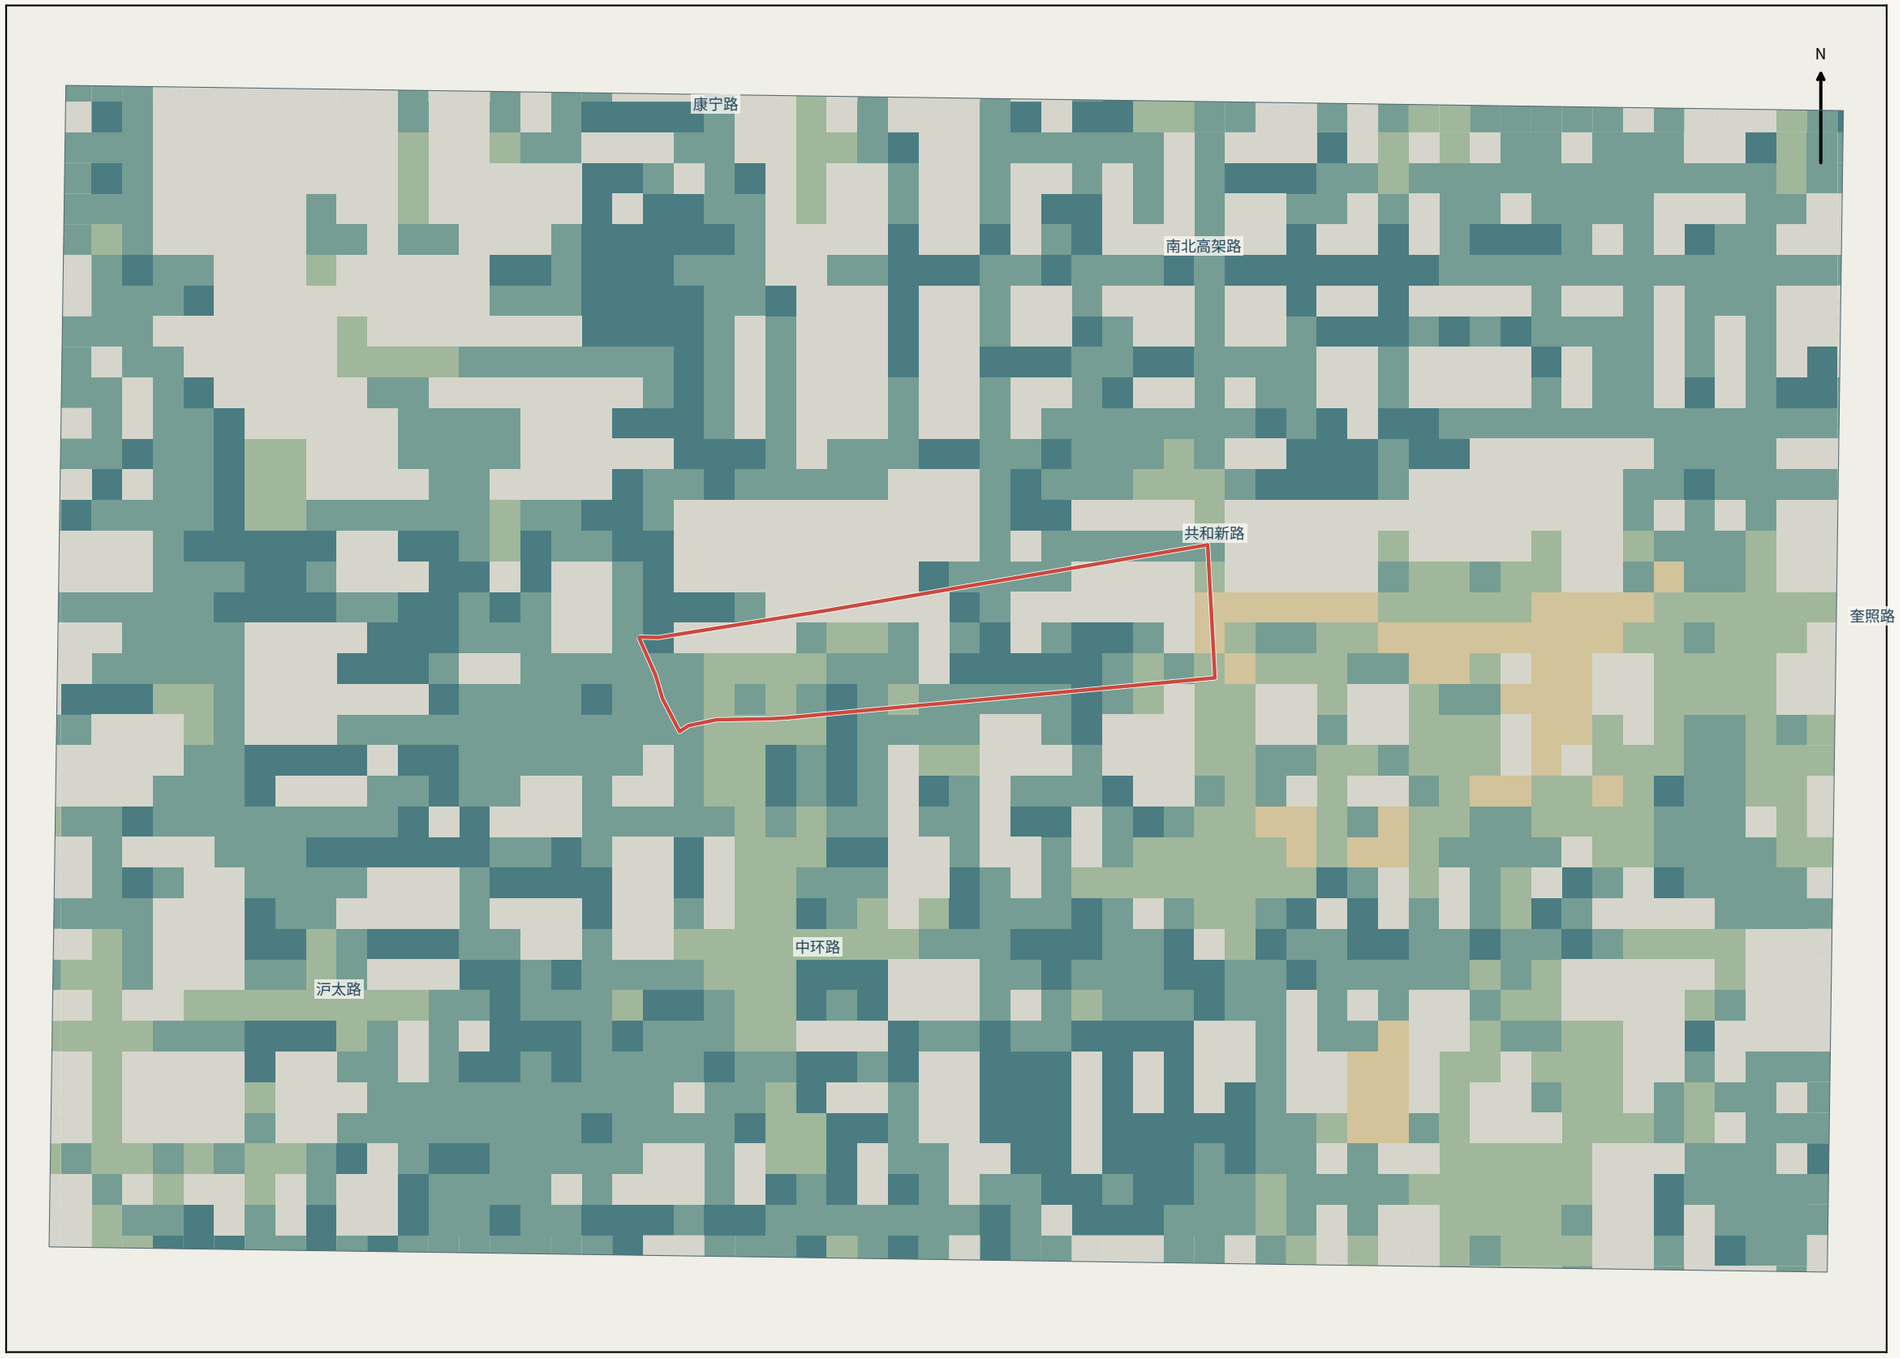

图例 / LEGEND

- 0 – 0.2
- 0.2 – 0.4
- 0.4 – 0.6
- 0.6 – 0.8
- 0.8 – 1
- 资料/有效覆盖不足，未计算
- 核心设计范围 / Design Site

0 500 1000 m

主要发现 / FINDINGS

- 100m真实几何统计；视图内2300个单元
- 有效1487；中位值0.499

指标与方法 / METHOD

三项等权百分位均值，非法定更新风险。等权：建筑密度百分位、已映射绿地不足百分位、日常服务可达路段不足百分位。仅研究初筛，不是旧改/拆迁名单。 V3改为100m真实相交重算；设计线仅标注，不改变全域统计口径。

地块现状与问题

设计区有效部分的公共环境初筛均值0.477，与全域0.485接近；地块约68.7%面积有有效值，不能据此把整块定为全域最紧迫对象。

区域协同关系

应将局部高值与周边街道、绿地及服务接入共同核对。密度、已映射绿地不足和服务接入三项等权指标，只支持调研排序，不代表真实需求、公共投资收益或既定项目清单。

改善方向

优先实查高值单元的通行、遮荫、休憩和服务接入口，选择能同时改善地块与相邻街区的小尺度工程；补充权属、使用人群及实施成本后再确定项目顺序。

A3 | 1:20,023.81 | EPSG:32651 | 设计66.0948ha | 周边　研究区内500米环带；可达比例为步行路段长度，非人口覆盖。

来源沿用原图：© OpenStreetMap contributors / Overture；ESA、Copernicus、EC-JRC、USGS、WorldPop。三段说明区分现状证据与研究建议。

16 现状数据问题与改善机会

Evidence gaps and amenity priorities

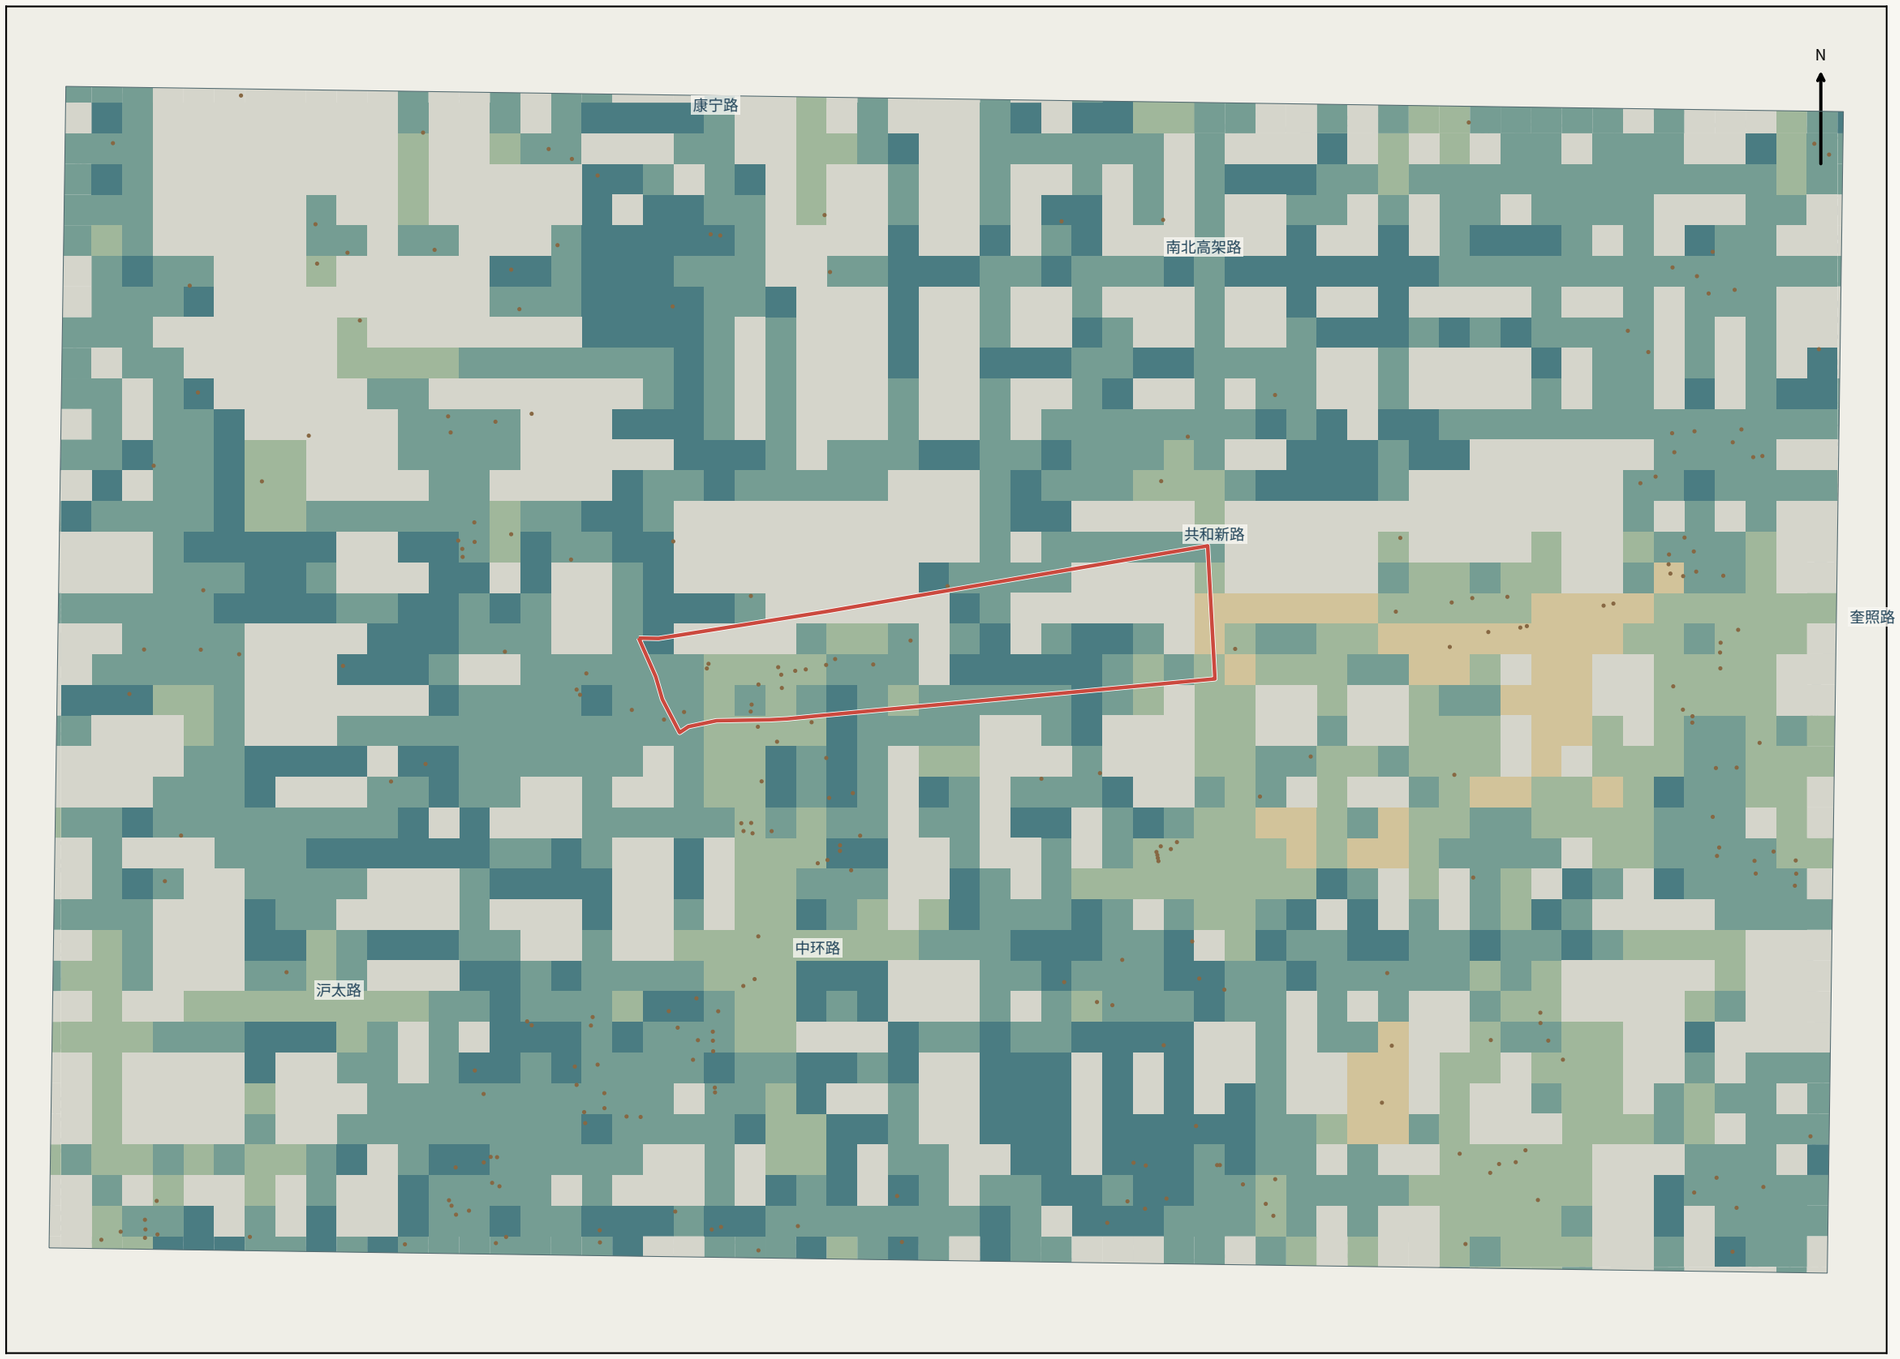

0 500 1000 m

图例 / LEGEND

- 0 – 0.2
- 0.2 – 0.4
- 0.4 – 0.6
- 0.6 – 0.8
- 0.8 – 1
- 资料/有效覆盖不足，未计算
- 原端点复核位置（非确认错误）
- 核心设计范围 / Design Site

主要发现 / FINDINGS

- 100m真实几何统计；视图内2300个单元
- 有效1487；中位值0.499

指标与方法 / METHOD

三项等权百分位均值，非法定更新风险。底色为透明初筛分数；叠加旧模型267端点复核位置，端点不自动视为错误。未分类地功能仍需补证。 V3改为100m真实相交重算；设计线仅标注，不改变全域统计口径。

地块现状与问题

设计区有15处源网络端点复核位置、2处道路面与建筑叠置记录。这些可能来自数据缺口、估算路宽或真实边界条件，不能直接认定断头路或实体冲突。

区域协同关系

问题核查应沿设计边界向周边道路延伸，关注江场西路、万荣路和高架界面的入口与分层关系；仅在红线内修图，可能掩盖跨边界的真实衔接条件。

改善方向

建立现场复核清单，逐项记录能否通行、道路实宽、建筑边界和门禁；证实后再完善慢行接续或路口组织。示意坡度记录不作为地形、排水或工程整改依据。

A3｜1:20,023.81｜EPSG:32651｜设计66.0948ha｜周边　研究区内500米环带；可达比例为步行路段长度，非人口覆盖。
来源沿用原图：© OpenStreetMap contributors / Overture；ESA、Copernicus、EC-JRC、USGS、WorldPop。三段说明区分现状证据与研究建议。

17 模型人口密度｜2020年100米

GHSL model population 2020

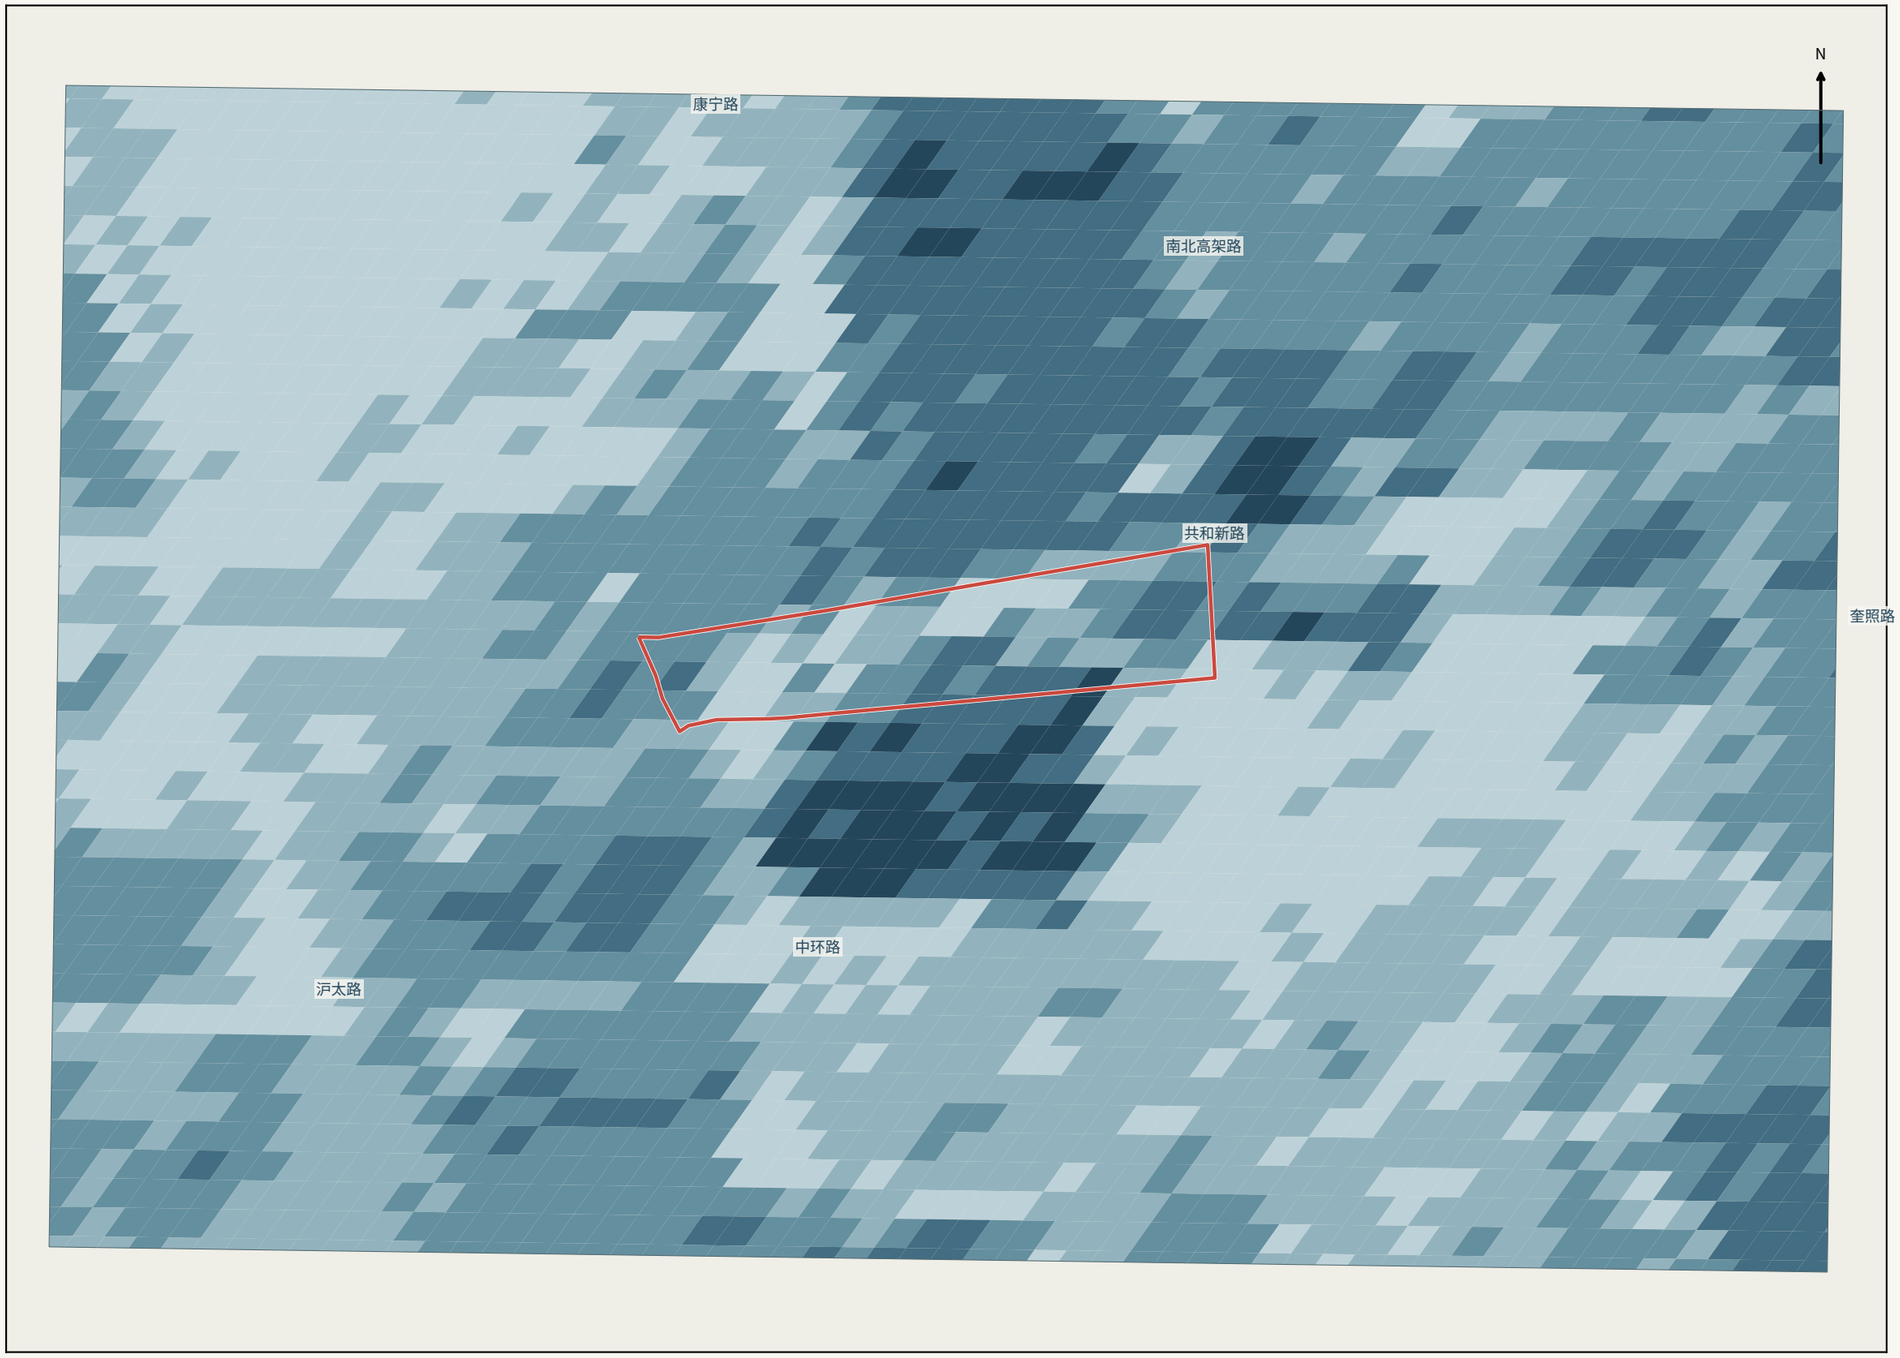

图例 / LEGEND

- 0 – 1e+04
- 1e+04 – 2e+04
- 2e+04 – 4e+04
- 4e+04 – 8e+04
- 8e+04 – 1.72e+05
- 核心设计范围 / Design Site

0 500 1000 m

主要发现 / FINDINGS

• 原生模型：2336个AOI裁切格网

• 2025约1km /
2020约100m；不重新细分

指标与方法 / METHOD

模型人 /
km^2；两年份产品不可直接作人口变化。GHSL R2023A 2020原生100m格网，边界按像元面积比例裁切。模型不是普查街坊实测人口。

地块现状与问题

2020年模型人口密度在设计区的面积加权均值约2.65万人/平方公里；周边环带约3.97万。周边模型密度更高，提示公共空间可能承接跨边界需求，而非仅服务地块内。

区域协同关系

全域同口径约2.37万人/平方公里。应结合较密集的近邻居住区组织服务与步行联系，但历史模型不能确定当前常住、就业、昼夜或流动人口。

改善方向

补充现况人口与实际活动调查，按人群和时段校核休憩、通学及日常服务容量；研究对周边开放的空间和设施，避免把模型数值直接换算成确定的建设规模。

A3｜1:20,023.81｜EPSG:32651｜设计66.0948ha｜周边　研究区内500米环带；可达比例为步行路段长度，非人口覆盖。

来源沿用原图：© OpenStreetMap contributors / Overture；ESA、Copernicus、EC-JRC、USGS、WorldPop。三段说明区分现状证据与研究建议。

18 模型人口密度｜2025年约1公里

WorldPop ALPHA model population 2025

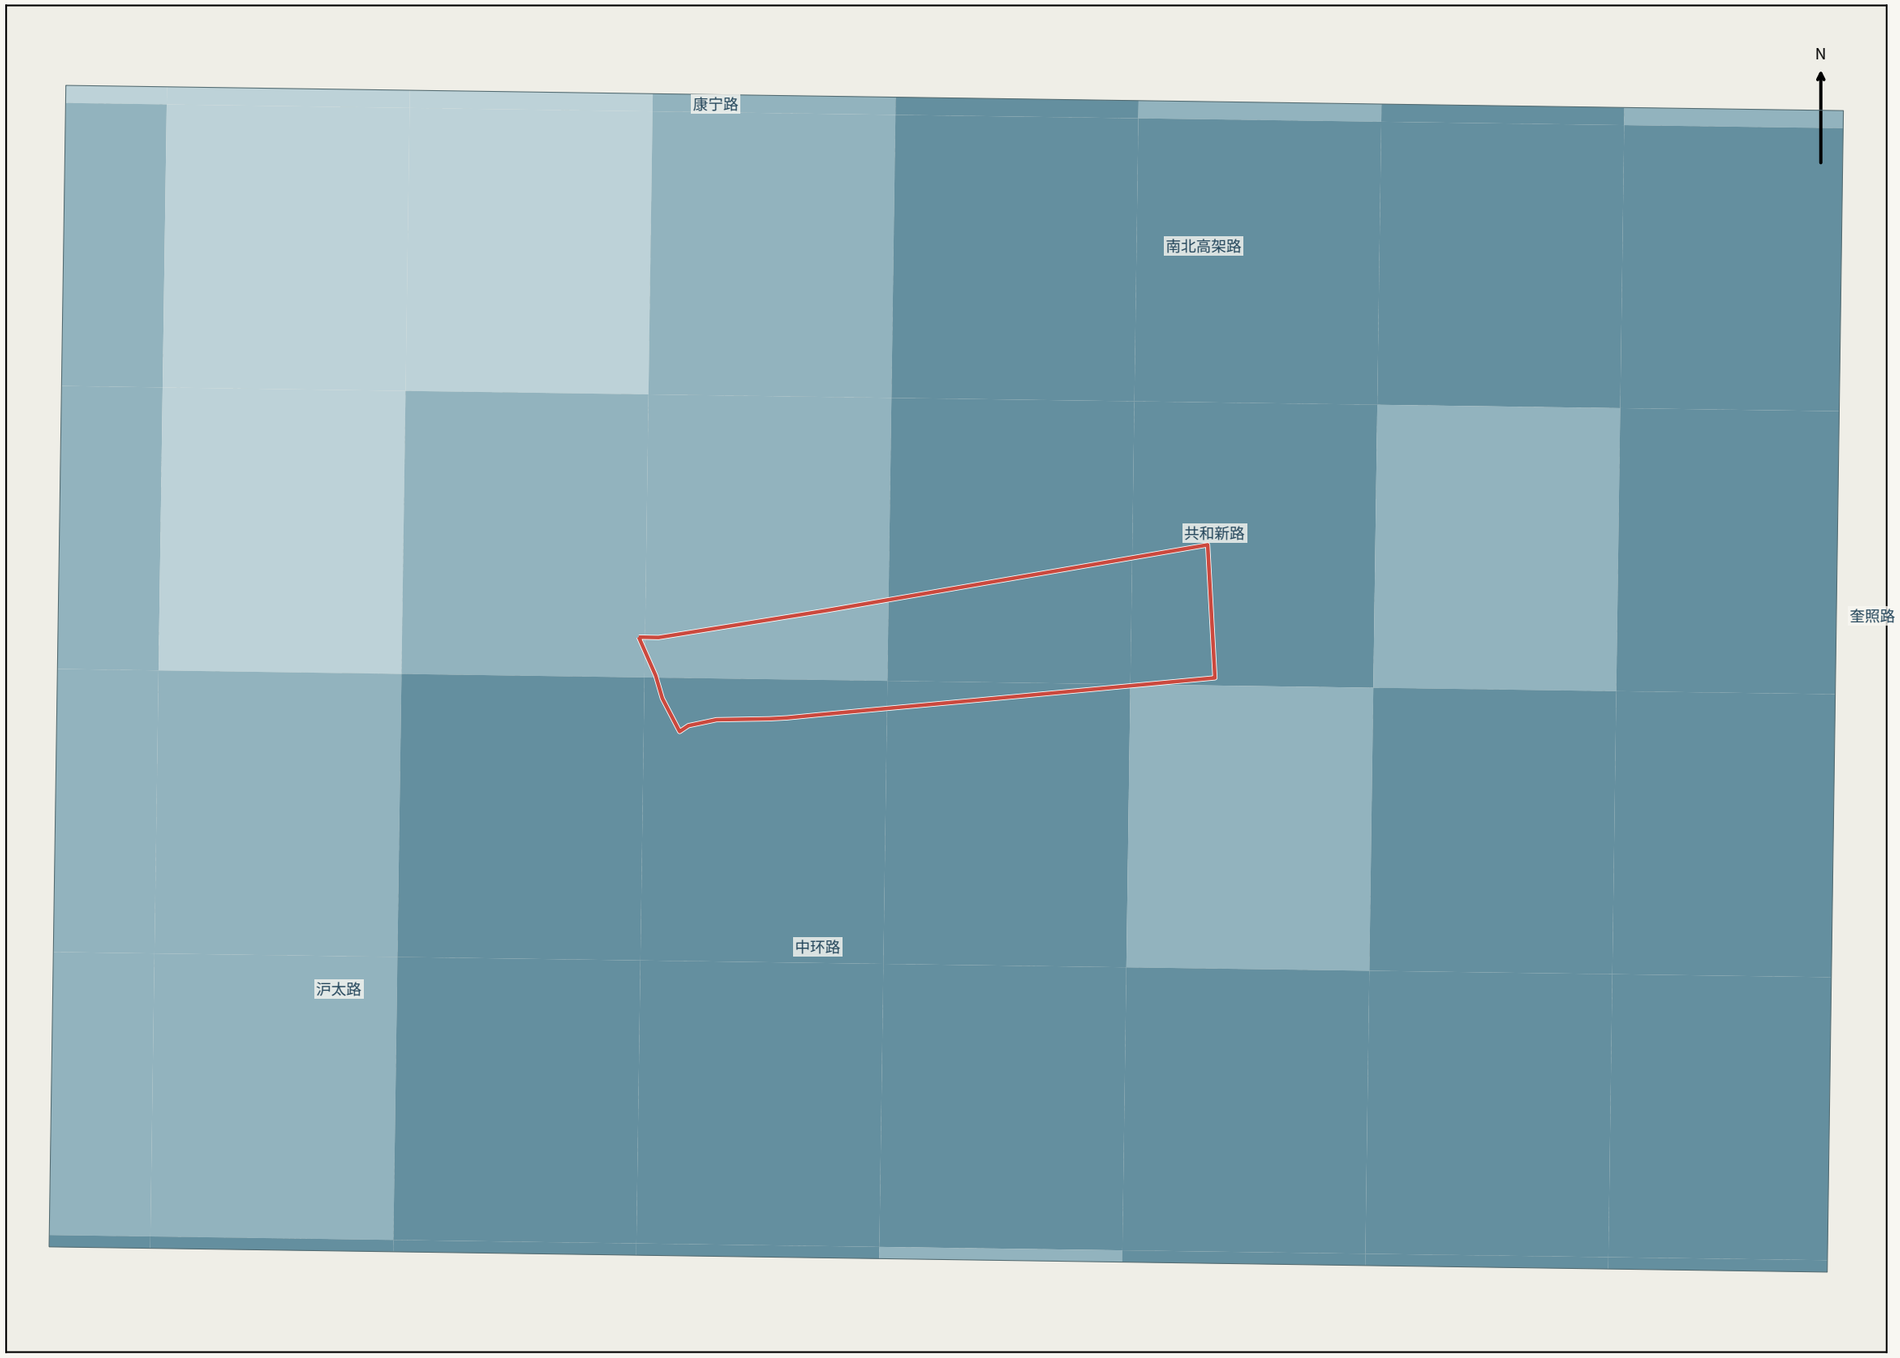

图例 / LEGEND

- 0 – 1e+04
- 1e+04 – 2e+04
- 2e+04 – 4e+04
- 4e+04 – 8e+04
- 8e+04 – 1.72e+05
- 核心设计范围 / Design Site

0 500 1000 m

主要发现 / FINDINGS

• 原生模型：48个AOI裁切格网

• 2025约1km /
2020约100m；不重新细分

指标与方法 / METHOD

模型人 / km²；两年份产品不可直接作人口变化。
保持WorldPop2025 ALPHA原生约1k
m的48个裁切单元；不插值到100m。与2020不
同模型不可解释为人口真实变化。

地块现状与问题

2025年人口模型在设计区的面积加权均值约2.10万人/平方公里，触及7个原生约1公里单元。像元大于多数设计细部，不能据图定位具体楼栋或街角需求。

区域协同关系

全域同口径约2.07万人/平方公里，与地块总体接近。宜用于片区服务协同的背景判断；与2020年产品来源和尺度不同，不作人口增减结论。

改善方向

按现况居民、就业者和到访者补查活动分布，再协调周边服务、通行与公共空间容量；保留原生模型单元，不把公里级数值拆细成看似精确的设计指标。

A3｜1:20,023.81｜EPSG:32651｜设计66.0948ha｜周边　研究区内500米环带；可达比例为步行路段长度，非人口覆盖。
来源沿用原图：© OpenStreetMap contributors / Overture；ESA、Copernicus、EC-JRC、USGS、WorldPop。三段说明区分现状证据与研究建议。

19 物理地表覆盖｜2021年

worldcover2021_10m

0 500 1000 m

图例 / LEGEND

- 树木
- 草地
- 耕地
- 建成覆盖
- 裸地
- 水体
- 核心设计范围 / Design Site

主要发现 / FINDINGS

- 有效像元220,113；中位数50
- 源栅格复用，不改分辨率或数据值

指标与方法 / METHOD

ESA WorldCover v200
10m物理覆盖，非功能/法定用地。

地块现状与问题

2021年10米地表覆盖产品中，建成类占设计区有效面积85.0%，高于全域81.4%。它说明建成背景突出，不能区分具体屋顶、道路与透水铺装。

区域协同关系

地块与周边均处于连续建成环境，蓝绿改善应跨街区接续。分类中的水面、植被与现状矢量存在尺度差异，不能仅据10米类别决定岸线和小绿地边界。

改善方向

结合现场铺装、树冠和水面核查，优先在可实施的硬化界面增设遮荫、透水及雨水调蓄设施；把地块改造与周边道路绿化衔接，具体工程参数另行勘察。

A3｜1:20,023.81｜EPSG:32651｜设计66.0948ha｜周边　研究区内500米环带；可达比例为步行路段长度，非人口覆盖。
来源沿用原图：© OpenStreetMap contributors / Overture；ESA、Copernicus、EC-JRC、USGS、WorldPop。三段说明区分现状证据与研究建议。

20 夏季植被指数｜2026年9月14日

ndvi_summer2026_10m

图例 / LEGEND

核心设计范围 / Design Site

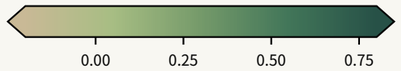

主要发现 / FINDINGS

- 有效像元209,229；中位数0.275
- 源栅格复用，不改分辨率或数据值

指标与方法 / METHOD

原始分辨率与单位见方法。Sentinel-2 10m NDVI；排除SCL云阴影。已逐波段同景镜像交叉核验1000DN差并避免重复扣offset。

0 500 1000 m

地块现状与问题

2026年9月14日夏季NDVI面积加权均值：设计区0.272、全域0.316；地块有效像元覆盖83.3%。地块植被光谱信号偏弱，空值不能当作裸地。

区域协同关系

周边环带同景均值0.305。宜将地块绿化与周边街道树冠和绿廊连续研究，避免只在局部集中植绿而沿步行路径仍缺少遮荫。

改善方向

现场核查树冠、种植条件和缺绿界面，优先接续江场西路—万荣路等公共路径的遮荫；保护既有植被并选择适地补植，不以单景NDVI直接认定绿化率或植物健康。

A3｜1:20,023.81｜EPSG:32651｜设计66.0948ha｜周边　研究区内500米环带；可达比例为步行路段长度，非人口覆盖。

来源沿用原图：© OpenStreetMap contributors / Overture；ESA、Copernicus、EC-JRC、USGS、WorldPop。三段说明区分现状证据与研究建议。

21 冬季植被指数｜2026年2月21日

ndvi_winter2026_10m

0 500 1000 m

图例 / LEGEND

核心设计范围 / Design Site

0.00 0.25 0.50 0.75

主要发现 / FINDINGS

- 有效像元220,090；中位数0.216
- 源栅格复用，不改分辨率或数据值

指标与方法 / METHOD

原始分辨率与单位见方法。Sentinel-2 10m NDVI；冬夏植被差异含季节、太阳高度和物候影响，非绿化退化结论。

地块现状与问题

2026年2月21日冬季NDVI均值为设计区0.202、周边环带0.271、全域0.262。地块冬季光谱绿量相对较弱，但不能从指数直接识别树种或确定养护问题。

区域协同关系

冬季环境品质应沿公共路径与邻近绿廊共同考虑。地块内部种植与周边街道绿化宜在季相、视线、采光和步行舒适性上协调，而非只追求夏季效果。

改善方向

调查现有常绿和落叶树种、树冠及冬季日照，因地制宜配置混合植被与挡风休憩点；保留冬季采光通道，避免在需要日照的界面机械加密常绿植物。

A3｜1:20,023.81｜EPSG:32651｜设计66.0948ha｜周边　研究区内500米环带；可达比例为步行路段长度，非人口覆盖。

来源沿用原图：© OpenStreetMap contributors / Overture；ESA、Copernicus、EC-JRC、USGS、WorldPop。三段说明区分现状证据与研究建议。

22 夏季卫星地表温度｜2026年8月1日

lst_summer2026_effective100m

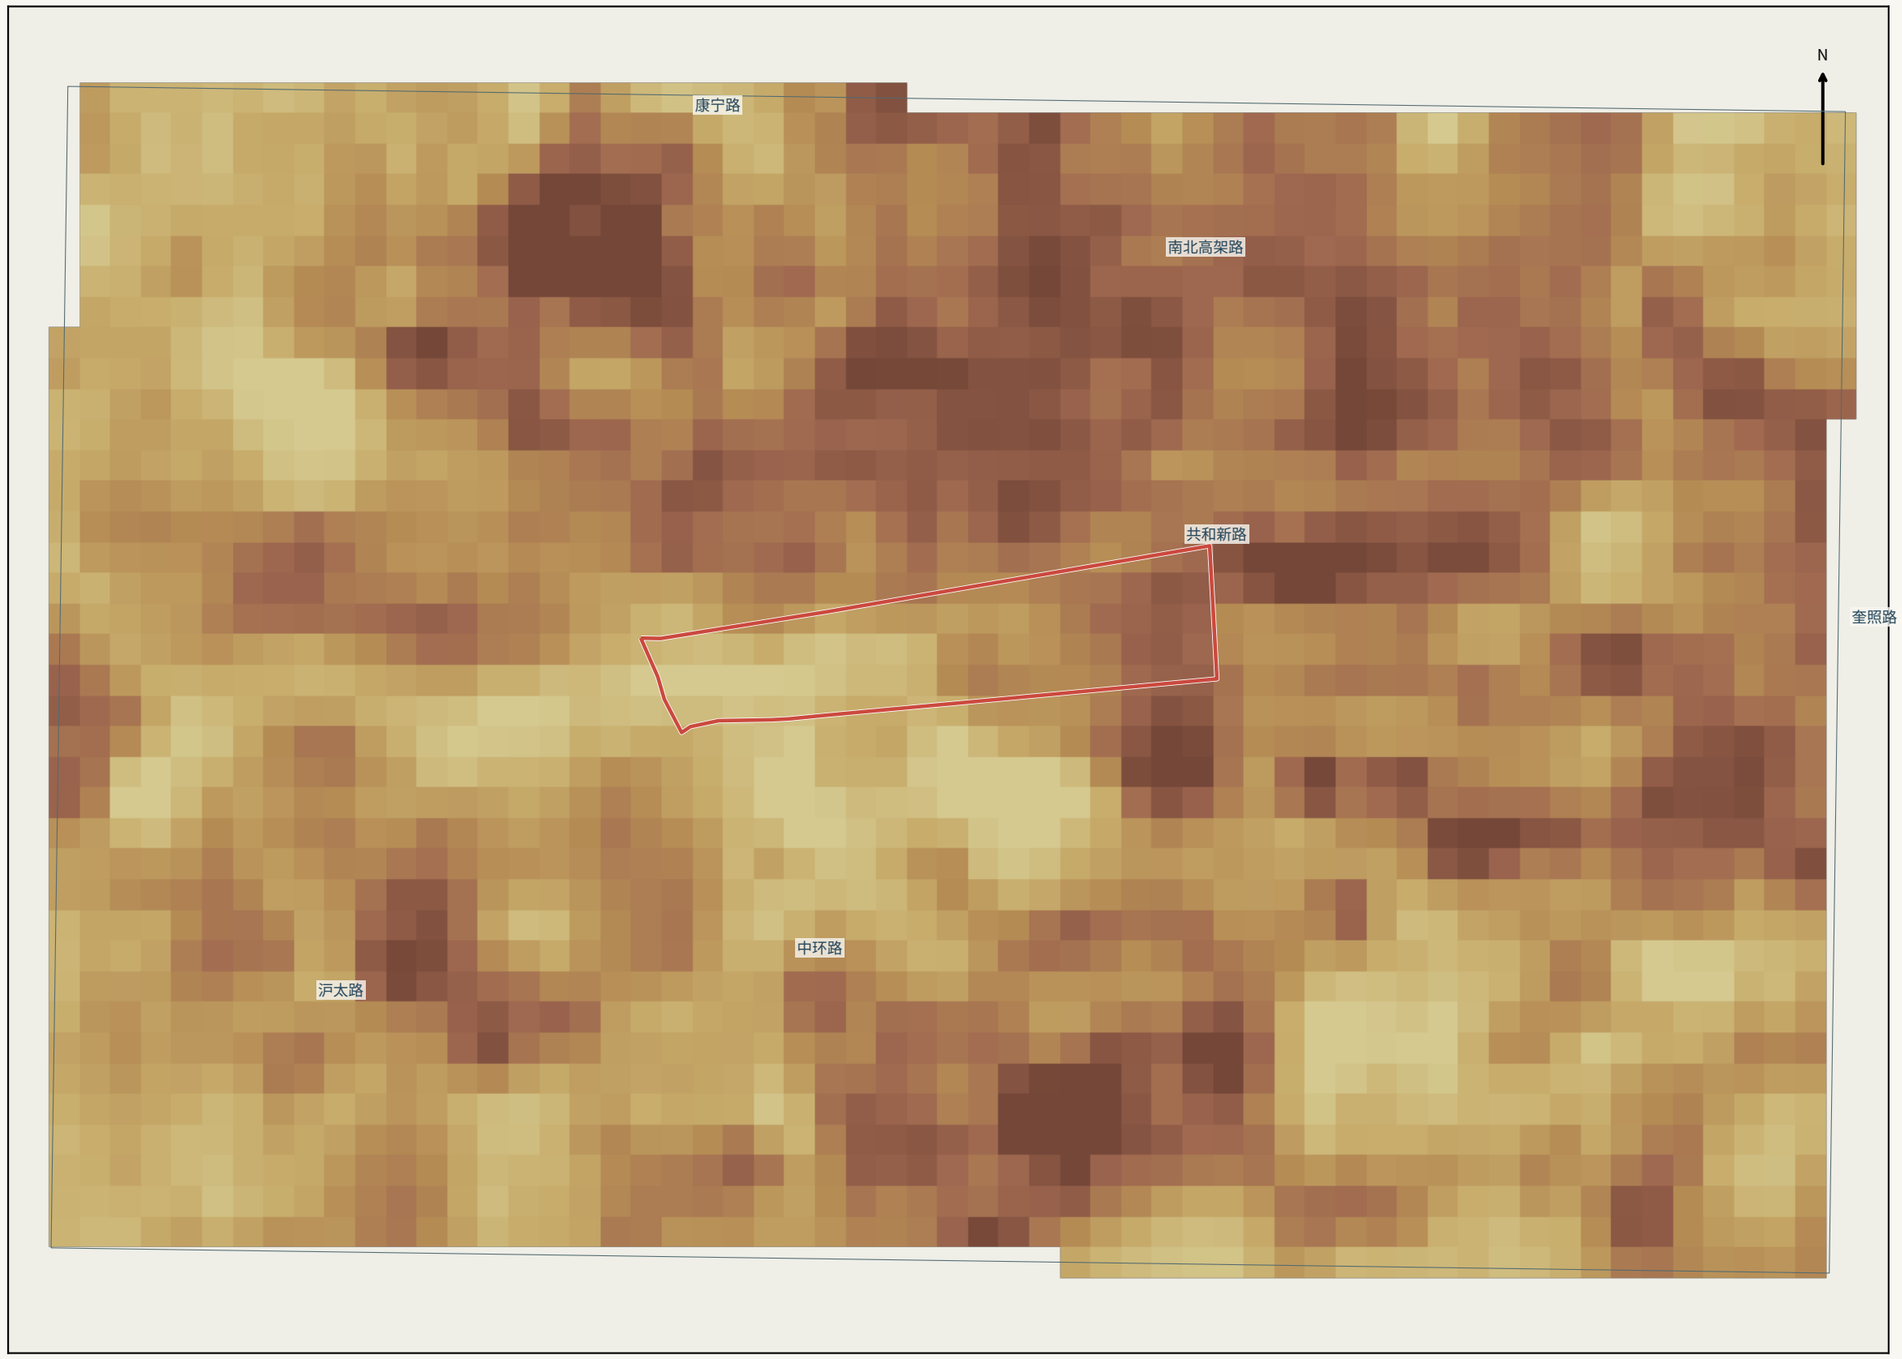

图例 / LEGEND

核心设计范围 / Design Site

45 50

0 500 1000 m

主要发现 / FINDINGS

- 有效像元2,201；中位数49.6
- 源栅格复用，不改分辨率或数据值

指标与方法 / METHOD

原始分辨率与单位见方法。Landsat L2 ST 温度°C；原始30m产品聚合到热红外有效100m。云掩膜后单景地表温度，不是实测气温。

地块现状与问题

2026年8月1日单景地表温度均值：设计区48.6°C、周边49.6°C、全域49.6°C。地块并非整体更热；该值是100米尺度地表温度，不是人体感受的气温。

区域协同关系

地块的水绿资源可作为与周边建成街区协同改善热环境的研究基础，但单次观测不能证明降温因果、热岛强度或每个街角的舒适度。

改善方向

优先实测重要步行路径的遮荫、辐射、风和使用时段，再安排树荫休憩、适宜铺装与可安全使用的水绿界面；把降温路径向周边连续衔接，避免用单景温度规定工程指标。

A3｜1:20,023.81｜EPSG:32651｜设计66.0948ha｜周边　研究区内500米环带；可达比例为步行路段长度，非人口覆盖。

来源沿用原图：© OpenStreetMap contributors / Overture；ESA、Copernicus、EC-JRC、USGS、WorldPop。三段说明区分现状证据与研究建议。

23 表面高程｜2021年约30米

dsm_copernicus2021_30m

图例 / LEGEND

核心设计范围 / Design Site

5 10

主要发现 / FINDINGS

- 有效像元24,448；中位数5.45
- 源栅格复用，不改分辨率或数据值

指标与方法 / METHOD

原始分辨率与单位见方法。Copernicus GLO30 DSM，含建筑和树冠；不是裸地DTM、道路实测高程或洪水淹没面。

地块现状与问题

30米表面高程产品在设计区的均值约5.65米，与周边5.67米接近。它含屋顶和植被影响，不能把图中微小起伏直接当作裸地地形或积水洼地。

区域协同关系

地块排水、滨水高程和道路衔接必须与周边管网、河道及控制标高统筹。当前DSM只能作为区域表面形态参照，不能判定跨边界汇流方向或防洪安全。

改善方向

补充地形测量、入口与道路高程、河道水位及排水资料后，再设计竖向、无障碍和雨水系统；保留现有基准，不依据粗DSM编造微地形或工程坡度。

A3｜1:20,023.81｜EPSG:32651｜设计66.0948ha｜周边　研究区内500米环带；可达比例为步行路段长度，非人口覆盖。

来源沿用原图：© OpenStreetMap contributors / Overture；ESA、Copernicus、EC-JRC、USGS、WorldPop。三段说明区分现状证据与研究建议。

24 夏季水体光谱指数

ndwi_summer2026_10m

0 500 1000 m

图例 / LEGEND

核心设计范围 / Design Site

-0.5 0.0 0.5

主要发现 / FINDINGS

- 有效像元209,229；中位数-0.278
- 源栅格复用，不改分辨率或数据值

指标与方法 / METHOD

原始分辨率与单位见方法。Sentinel-2 NDWI=(绿光−近红外)/(绿光+近红外)，10m；不能直接等同真实水边界。

地块现状与问题

夏季NDWI均值为设计区-0.256、全域-0.300；设计区有效覆盖83.3%。负均值不表示无水，窄河道、阴影和混合像元均影响表达。

区域协同关系

图示光谱与矢量水面应交叉核对，关注地块水系与区域蓝绿通道的连续关系。不能用单一指数确定岸线开放程度、水质或水生态状况。

改善方向

先核查真实岸线、水面与桥下空间，结合管理和安全条件接续滨水步行及生态缓冲；水质、流量和水位另行监测，不按指数颜色直接安排水系改造。

A3｜1:20,023.81｜EPSG:32651｜设计66.0948ha｜周边　研究区内500米环带；可达比例为步行路段长度，非人口覆盖。

来源沿用原图：© OpenStreetMap contributors / Overture；ESA、Copernicus、EC-JRC、USGS、WorldPop。三段说明区分现状证据与研究建议。

25 夏季建成光谱指数

ndbi_summer2026_20m

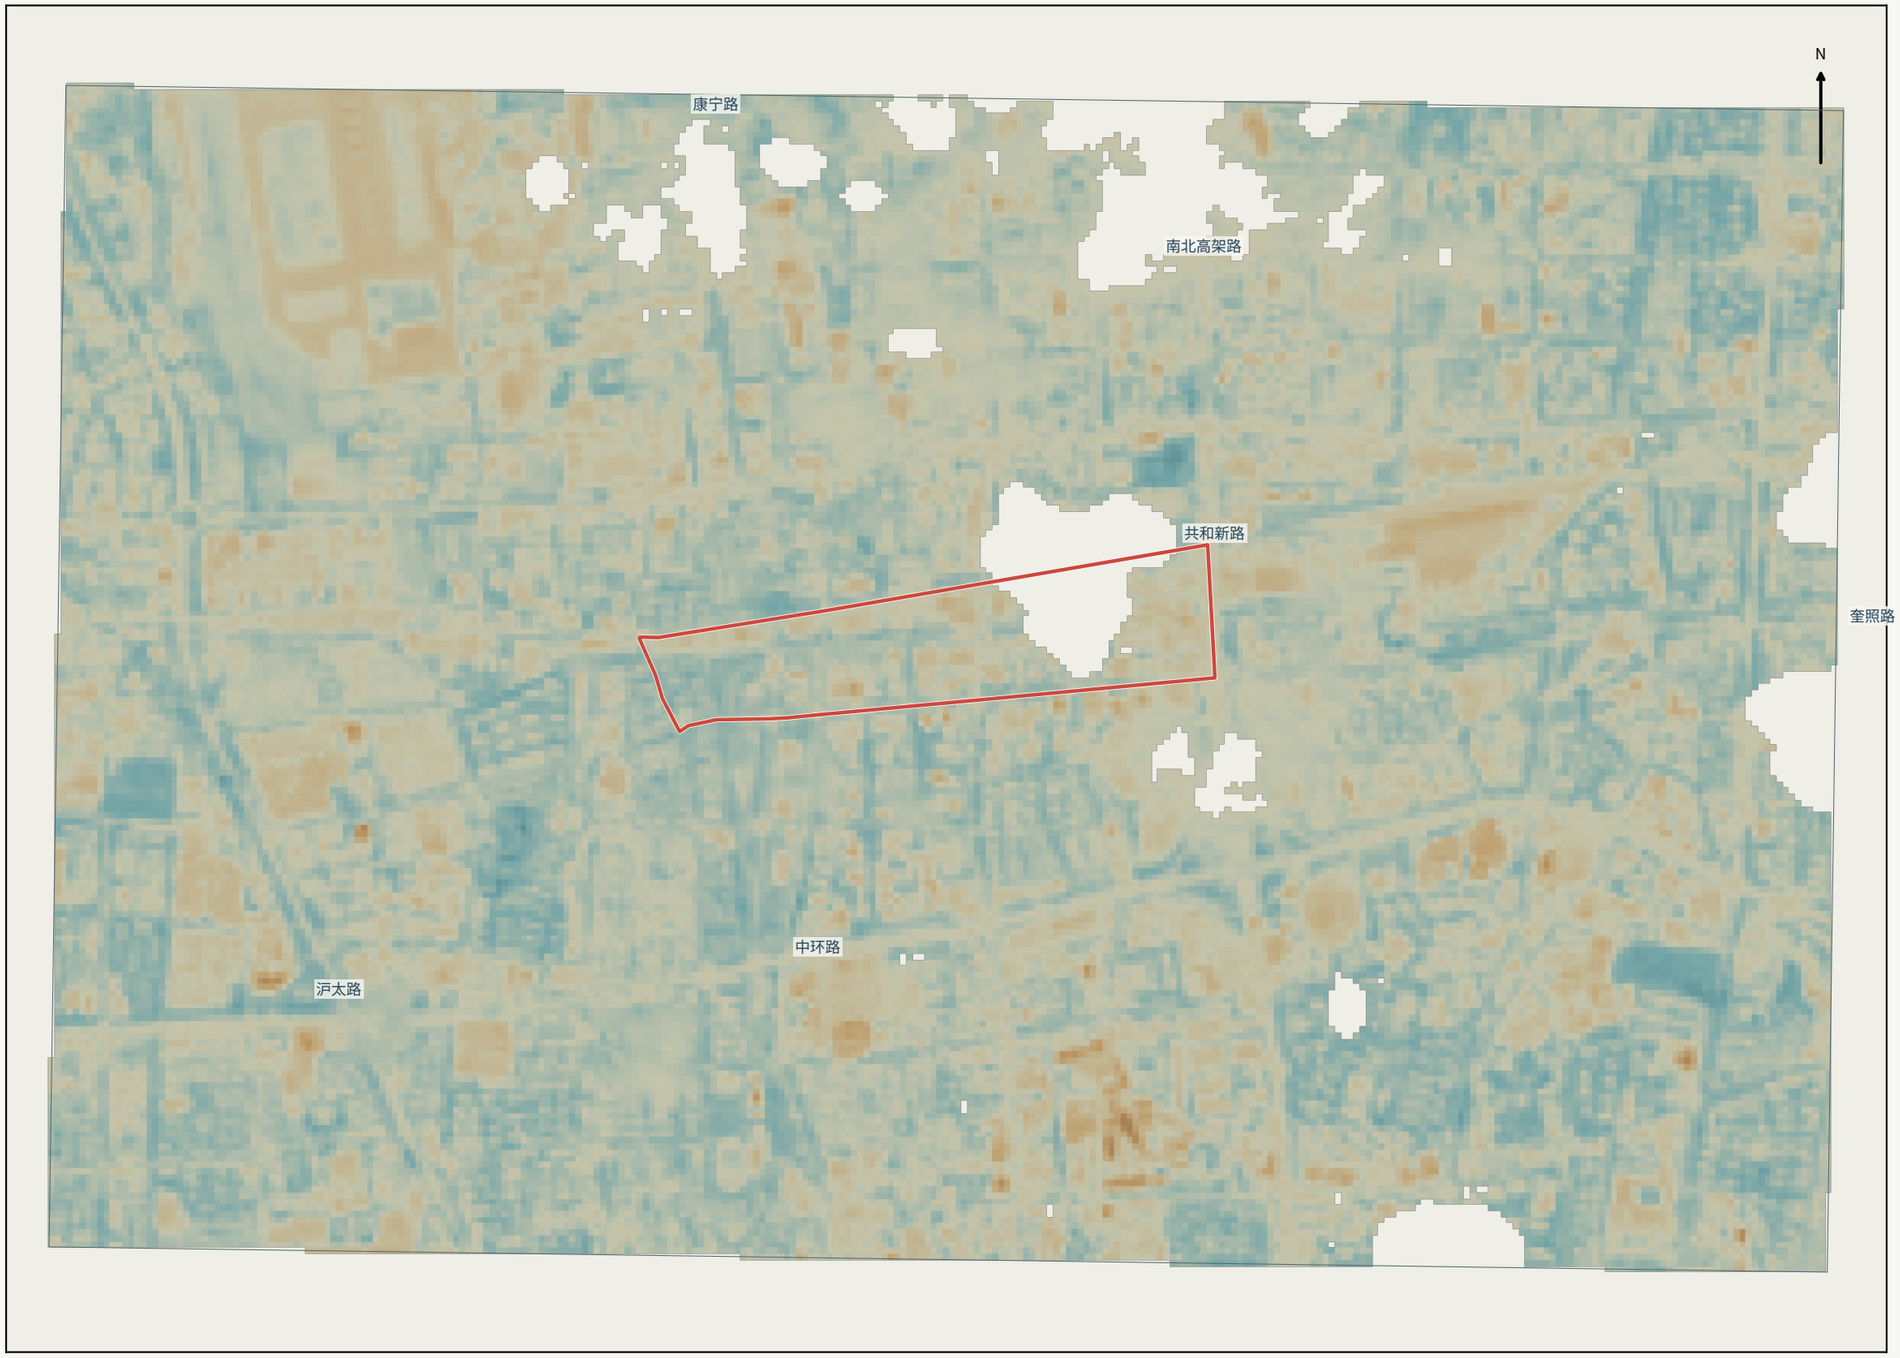

图例 / LEGEND

核心设计范围 / Design Site

-0.5 0.0 0.5

主要发现 / FINDINGS

- 有效像元52,313；中位数-0.062
- 源栅格复用，不改分辨率或数据值

指标与方法 / METHOD

原始分辨率与单位见方法。Sentinel-2 NDBI=(SWIR−NIR)/(SWIR+NIR)，20m；裸地等可混淆，不是法定建设用地。

0 500 1000 m

地块现状与问题

夏季NDBI均值为设计区-0.039、周边-0.077、全域-0.067。设计区相对偏高，但负值不能解释为非建成区，指数也不是建筑密度或透水率。

区域协同关系

应把地块与周边连续建成街区一并检查，结合建筑轮廓、植被和温度判断具体硬化界面；不同指标的分辨率与含义不同，不作直接一一对应。

改善方向

核实道路、屋顶与场地铺装后，优先改善公共路径的遮荫和可透水空间，并向相邻街段接续；不以NDBI高低直接划定拆改或新增建设范围。

A3｜1:20,023.81｜EPSG:32651｜设计66.0948ha｜周边　研究区内500米环带；可达比例为步行路段长度，非人口覆盖。
来源沿用原图：© OpenStreetMap contributors / Overture；ESA、Copernicus、EC-JRC、USGS、WorldPop。三段说明区分现状证据与研究建议。

26 历史物理地表覆盖｜2019年

CLCD historical physical land cover 2019

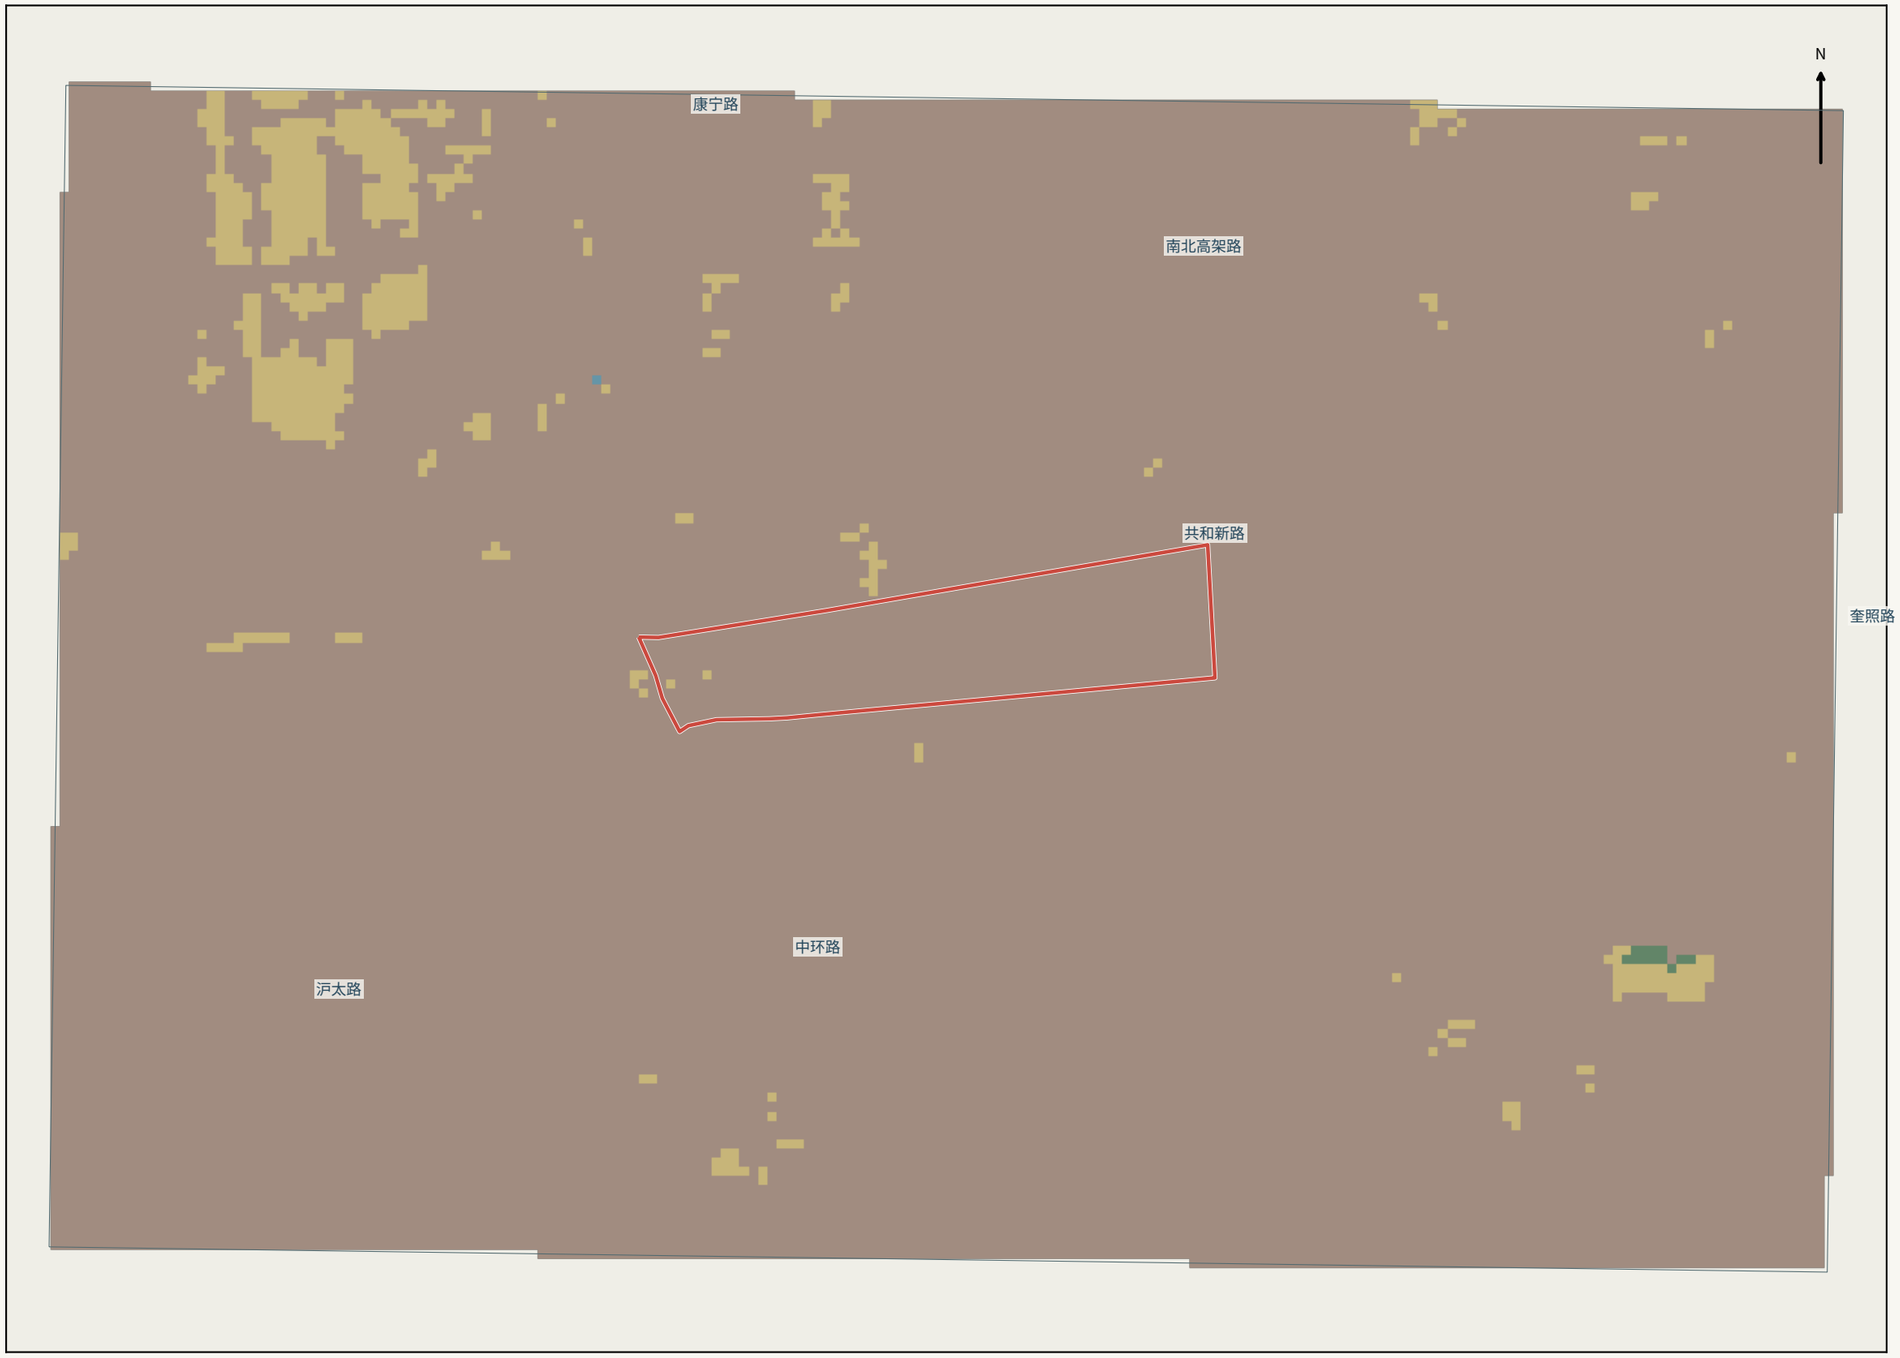

0 500 1000 m

图例 / LEGEND

- 耕地
- 林地
- 水体
- 不透水
- 核心设计范围 / Design Site

主要发现 / FINDINGS

- 有效像元24,451；中位数8
- 源栅格复用，不改分辨率或数据值

指标与方法 / METHOD

CLCD2019原生约30米；仅选取压缩扫描行局部解码。与WorldCover2021年份/方法不同，不能直接把差异当真实变化。

地块现状与问题

2019年30米CLCD将设计区有效面积99.7%标为不透水类，全域为97.2%。粗分类说明历史建成背景，不能替代现状小尺度铺装调查。

区域协同关系

该图与2021年WorldCover的分类体系及精度不同，不能把差异解释为两年间绿地或水面变化。地块应在区域存量建成格局中研究修补，而非套用历史像元边界。

改善方向

对照现况资料确认仍然存在的硬化界面，联动周边道路与公共空间开展适度透水、植绿和连通优化；土地用途、工程透水率与实施范围均需另行核定。

A3｜1:20,023.81｜EPSG:32651｜设计66.0948ha｜周边　研究区内500米环带；可达比例为步行路段长度，非人口覆盖。

来源沿用原图：© OpenStreetMap contributors / Overture；ESA、Copernicus、EC-JRC、USGS、WorldPop。三段说明区分现状证据与研究建议。

27 历史水面观测频率｜1984—2021

Historical water observation occurrence

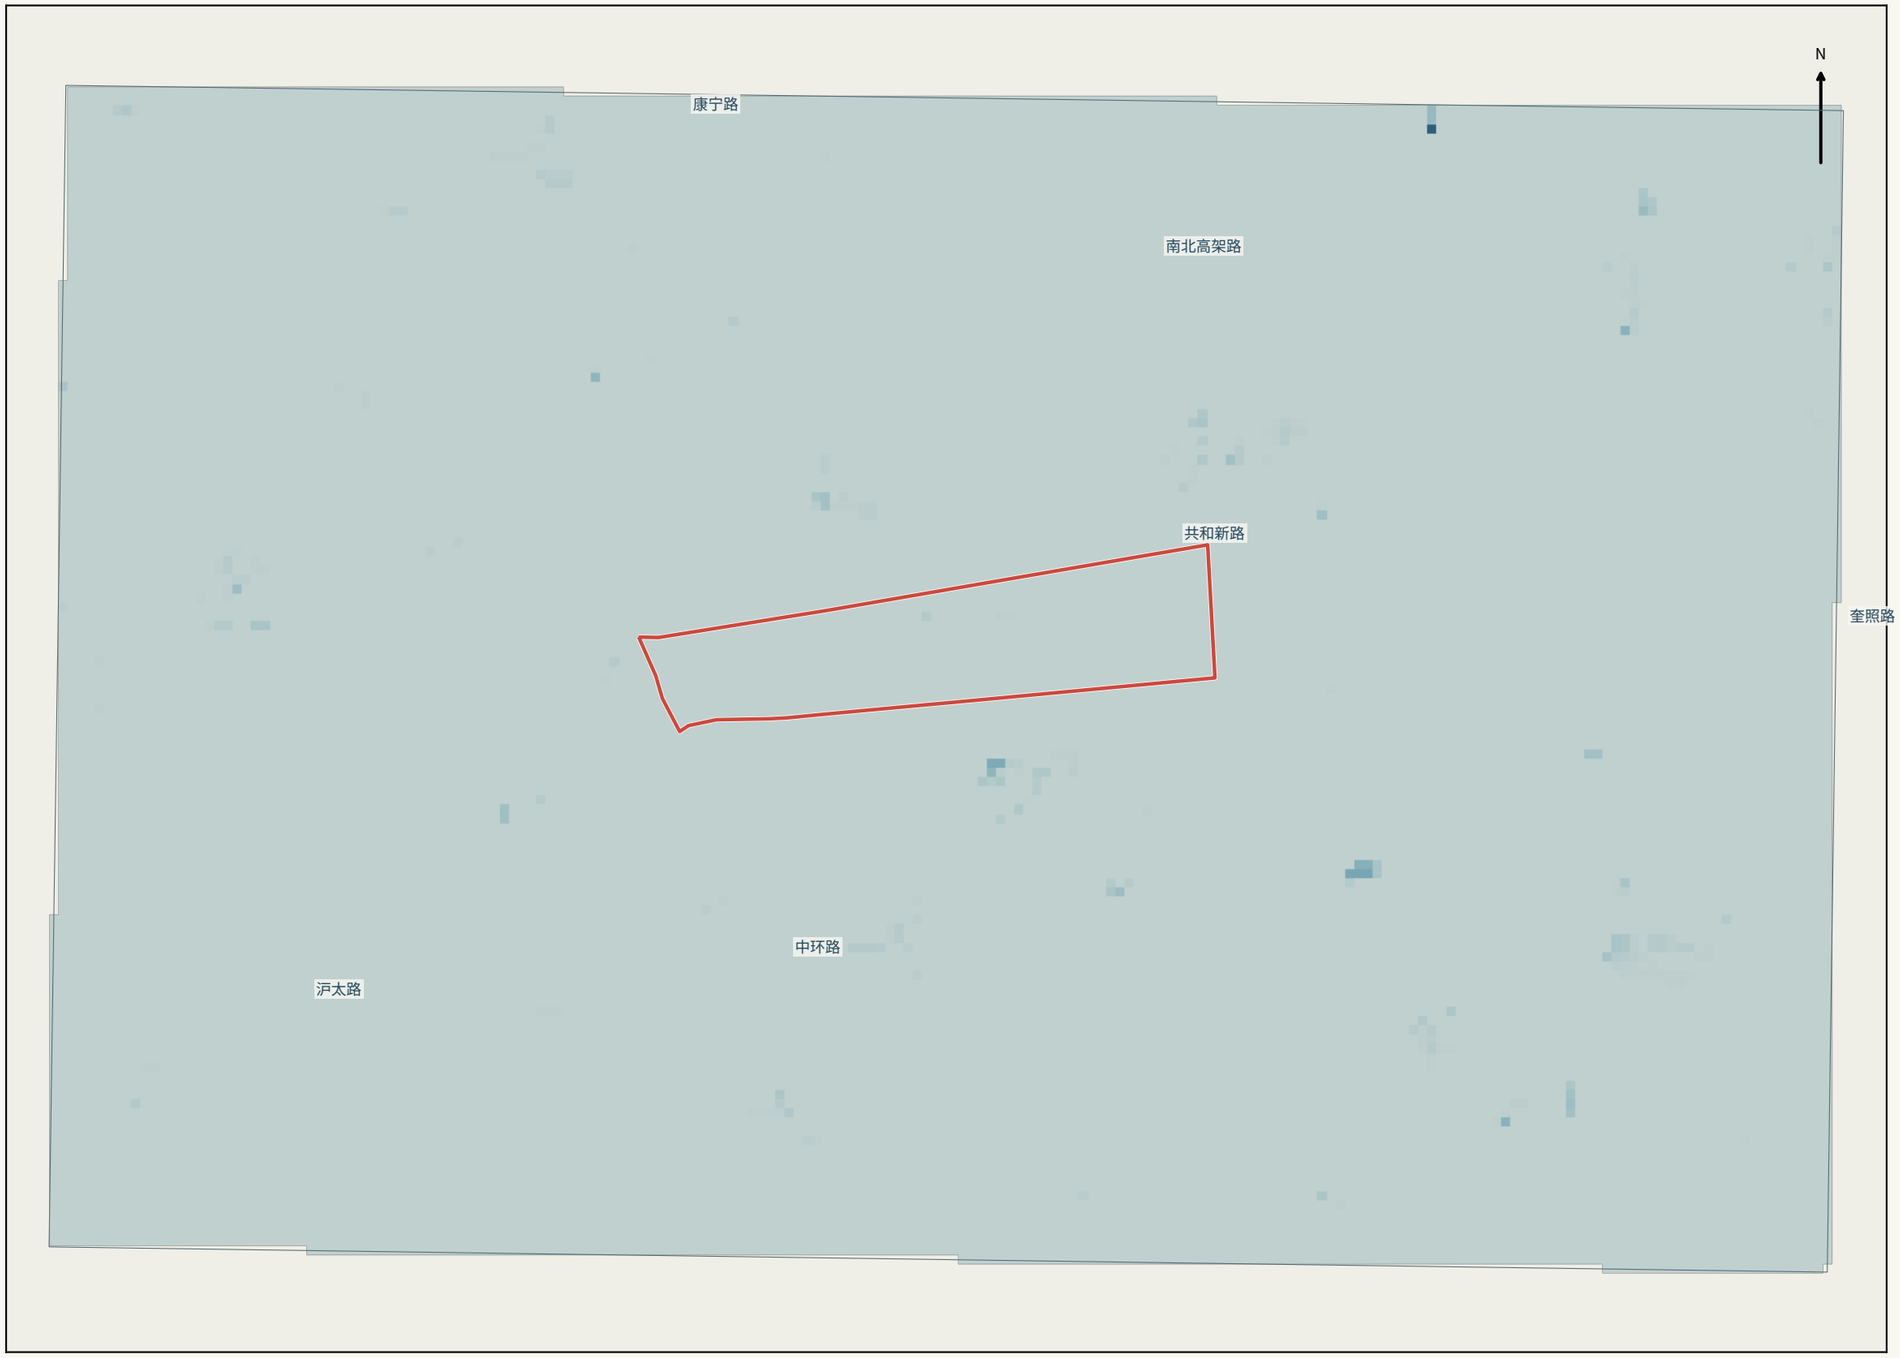

图例 / LEGEND

核心设计范围 / Design Site

0 20 40

主要发现 / FINDINGS

- 有效像元24,467；中位数0
- 源栅格复用，不改分辨率或数据值

指标与方法 / METHOD

原始分辨率与单位见方法。EC JRC GSW v1.4历史水面观测频率%；仅局部六瓦片压缩约20KB。不是2026水边界、洪水概率或法定蓝线。

0 500 1000 m

地块现状与问题

历史30米水面观测频率在设计区的面积加权均值接近0，而现状矢量水面占6.8%。这种明显不一致提示窄水道、时间范围或分类识别差异，不能判断水面消失、填埋或新增。

区域协同关系

地块水系必须放入周边真实河网、桥梁及管网关系中核查。历史水面频率不反映当前水位、河道连通、岸线可达性或内涝风险。

改善方向

以现况岸线和水务资料为主核对水系，保留可确认的蓝绿联系；在权属、防洪和水生态条件明确后研究连续岸线及步行节点，不依据低频像元削减水系空间。

A3｜1:20,023.81｜EPSG:32651｜设计66.0948ha｜周边　研究区内500米环带；可达比例为步行路段长度，非人口覆盖。
来源沿用原图：© OpenStreetMap contributors / Overture；ESA、Copernicus、EC-JRC、USGS、WorldPop。三段说明区分现状证据与研究建议。

28 冬夏植被指数季节差｜2026年

Summer minus winter NDVI on joint valid pixels

图例 / LEGEND

核心设计范围 / Design Site

-0.50 -0.25 0.00 0.25 0.50

0 500 1000 m

主要发现 / FINDINGS

- 有效像元209,221；中位数0.0384
- 源栅格复用，不改分辨率或数据值

指标与方法 / METHOD

原始分辨率与单位见方法。9月14日NDVI减2月21日NDVI；只用双方有效像元10m。含物候、太阳角度与季节影响，不是永久绿化变化。

地块现状与问题

2026年冬夏共同有效像元内，设计区NDVI季节差均值0.065，周边0.036。地块可见一定季相差异，但两景差值不代表年度增绿或植被退化。

区域协同关系

区域绿化协调应同时考虑地块与周边街道在不同季节的遮荫、采光和景观连续性。天气、物候、阴影和有效像元缺失均会影响图示差异。

改善方向

调查树种与季节使用需求，沿公共路径优化常绿—落叶搭配、林下休憩及冬季采光；用多时相观测和养护记录检验效果，不把单次差值直接转为种植数量目标。

A3｜1:20,023.81｜EPSG:32651｜设计66.0948ha｜周边　研究区内500米环带；可达比例为步行路段长度，非人口覆盖。
来源沿用原图：© OpenStreetMap contributors / Overture；ESA、Copernicus、EC-JRC、USGS、WorldPop。三段说明区分现状证据与研究建议。

R01 建筑基底覆盖率｜100米

Building footprint coverage

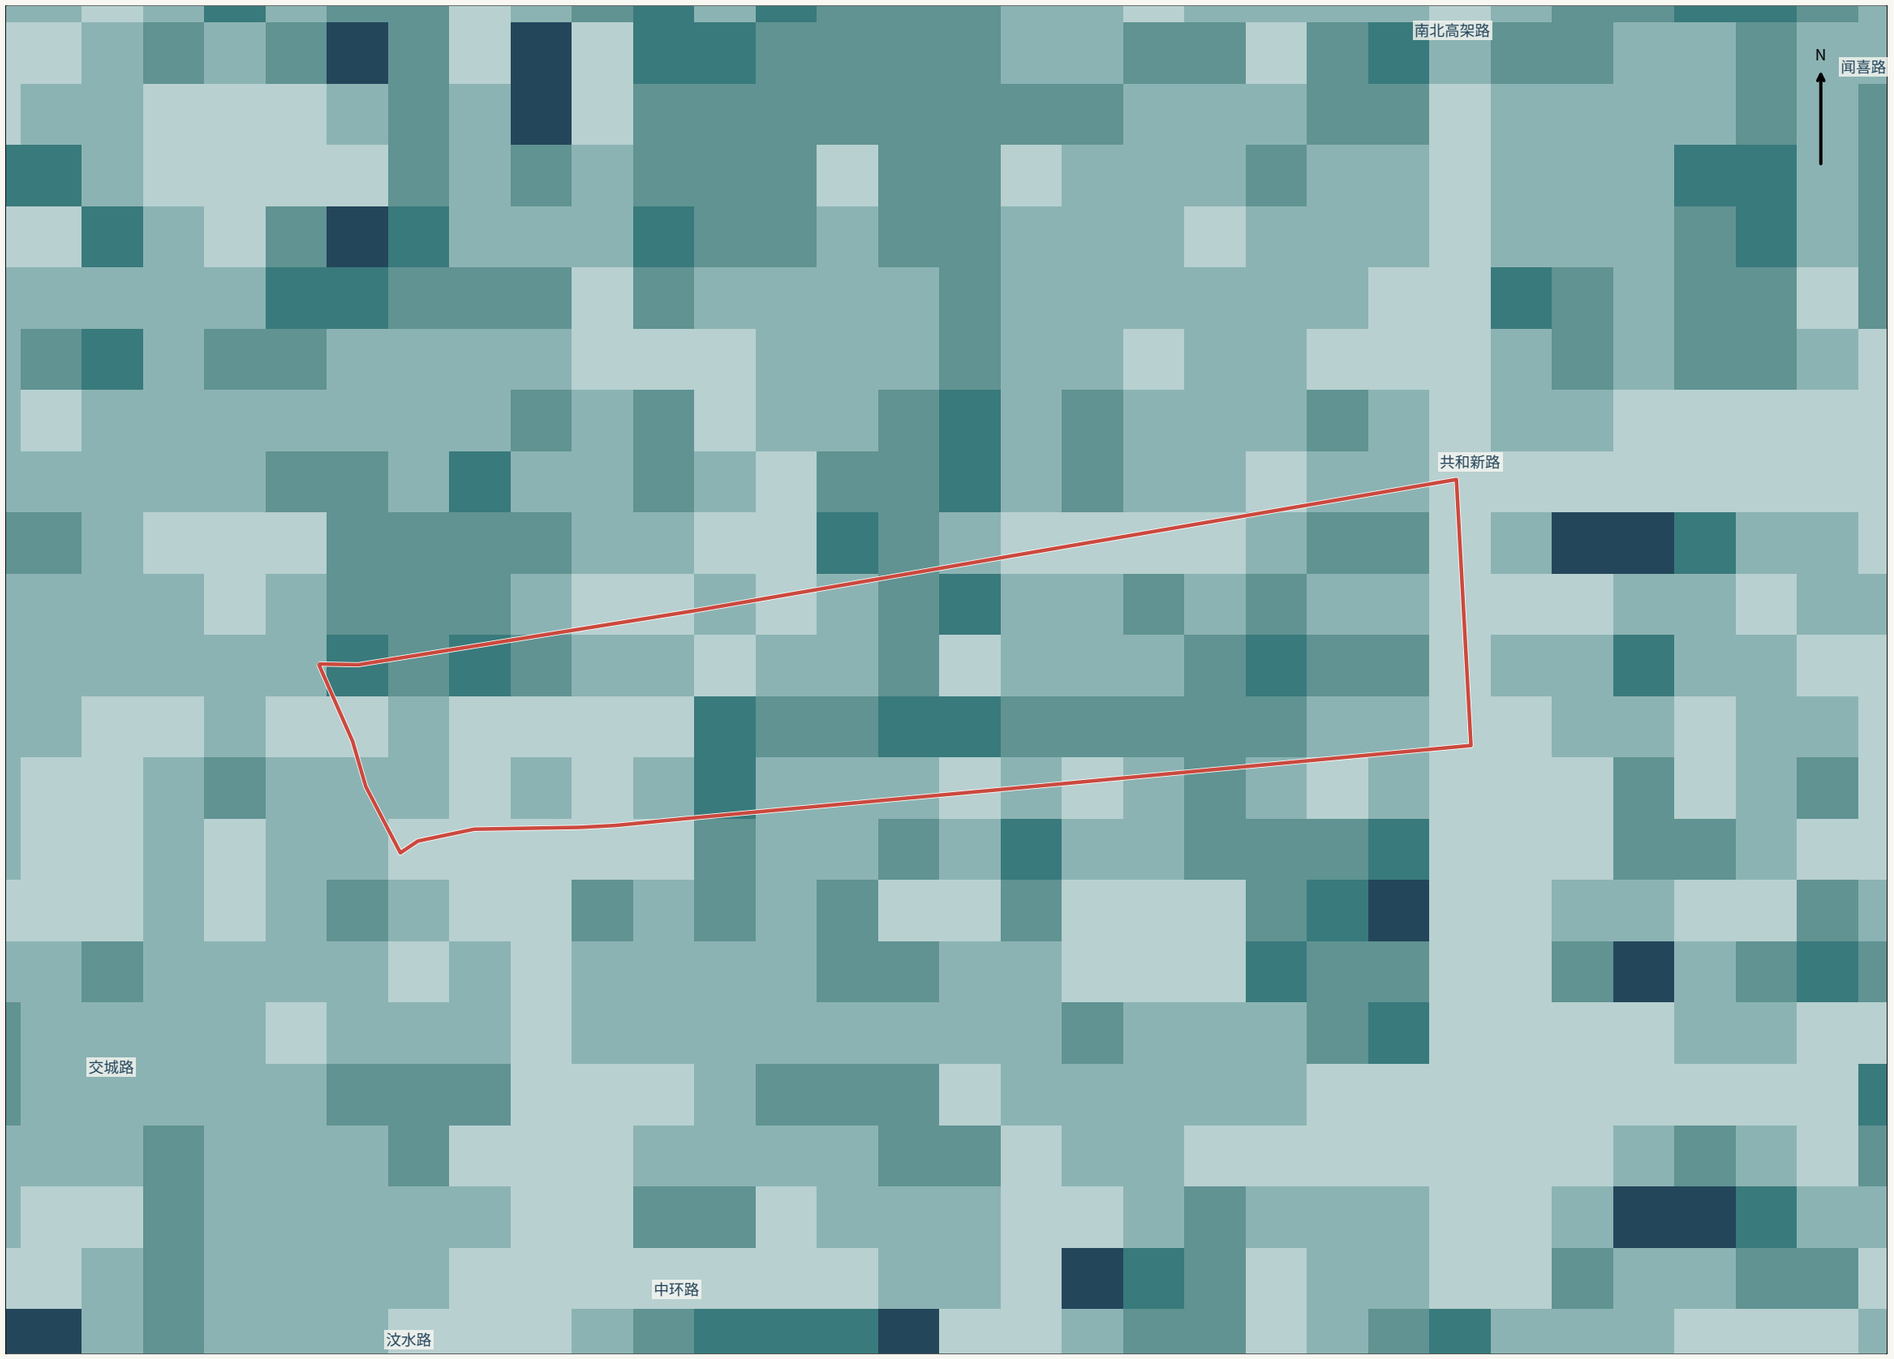

图例 / LEGEND

- 0 – 0.15
- 0.15 – 0.3
- 0.3 – 0.45
- 0.45 – 0.6
- 0.6 – 1
- 核心设计范围 / Design Site

主要发现 / FINDINGS

- 100m真实几何统计；视图内736个单元
- 有效736；中位值0.229

指标与方法 / METHOD

建筑占地并集 / 实际单元面积。采用与全域相同固定分级；只是局部放大视图，不将设计线变成强制统计裁切。 50m真实相交结果另存，100m为正式表达。

地块现状与问题

设计区基底覆盖26.6%；图示100米单元中≥45%高值与低值空间并存，重点不是全区一律疏解，而是辨明密集建筑边缘的通行、日照和院落是否受限。

区域协同关系

邻近环带覆盖22.5%。局部改善宜沿江场西路和万荣路衔接相邻街区，避免只在内部形成可见但不可进入的开敞空间。

改善方向

对高覆盖单元逐处调查入口、后勤和消防，争取合法开放的连通院落、街角退让与连续人行；细部以建筑和权属实测为准，100米格网不作为项目边界。

A3｜1:10,011.90｜EPSG:32651｜设计66.0948ha｜周边　研究区内500米环带；可达比例为步行路段长度，非人口覆盖。

来源沿用原图：© OpenStreetMap contributors / Overture；ESA、Copernicus、EC-JRC、USGS、WorldPop。三段说明区分现状证据与研究建议。

R02 估高建筑体量代理｜100米

Estimated volume proxy

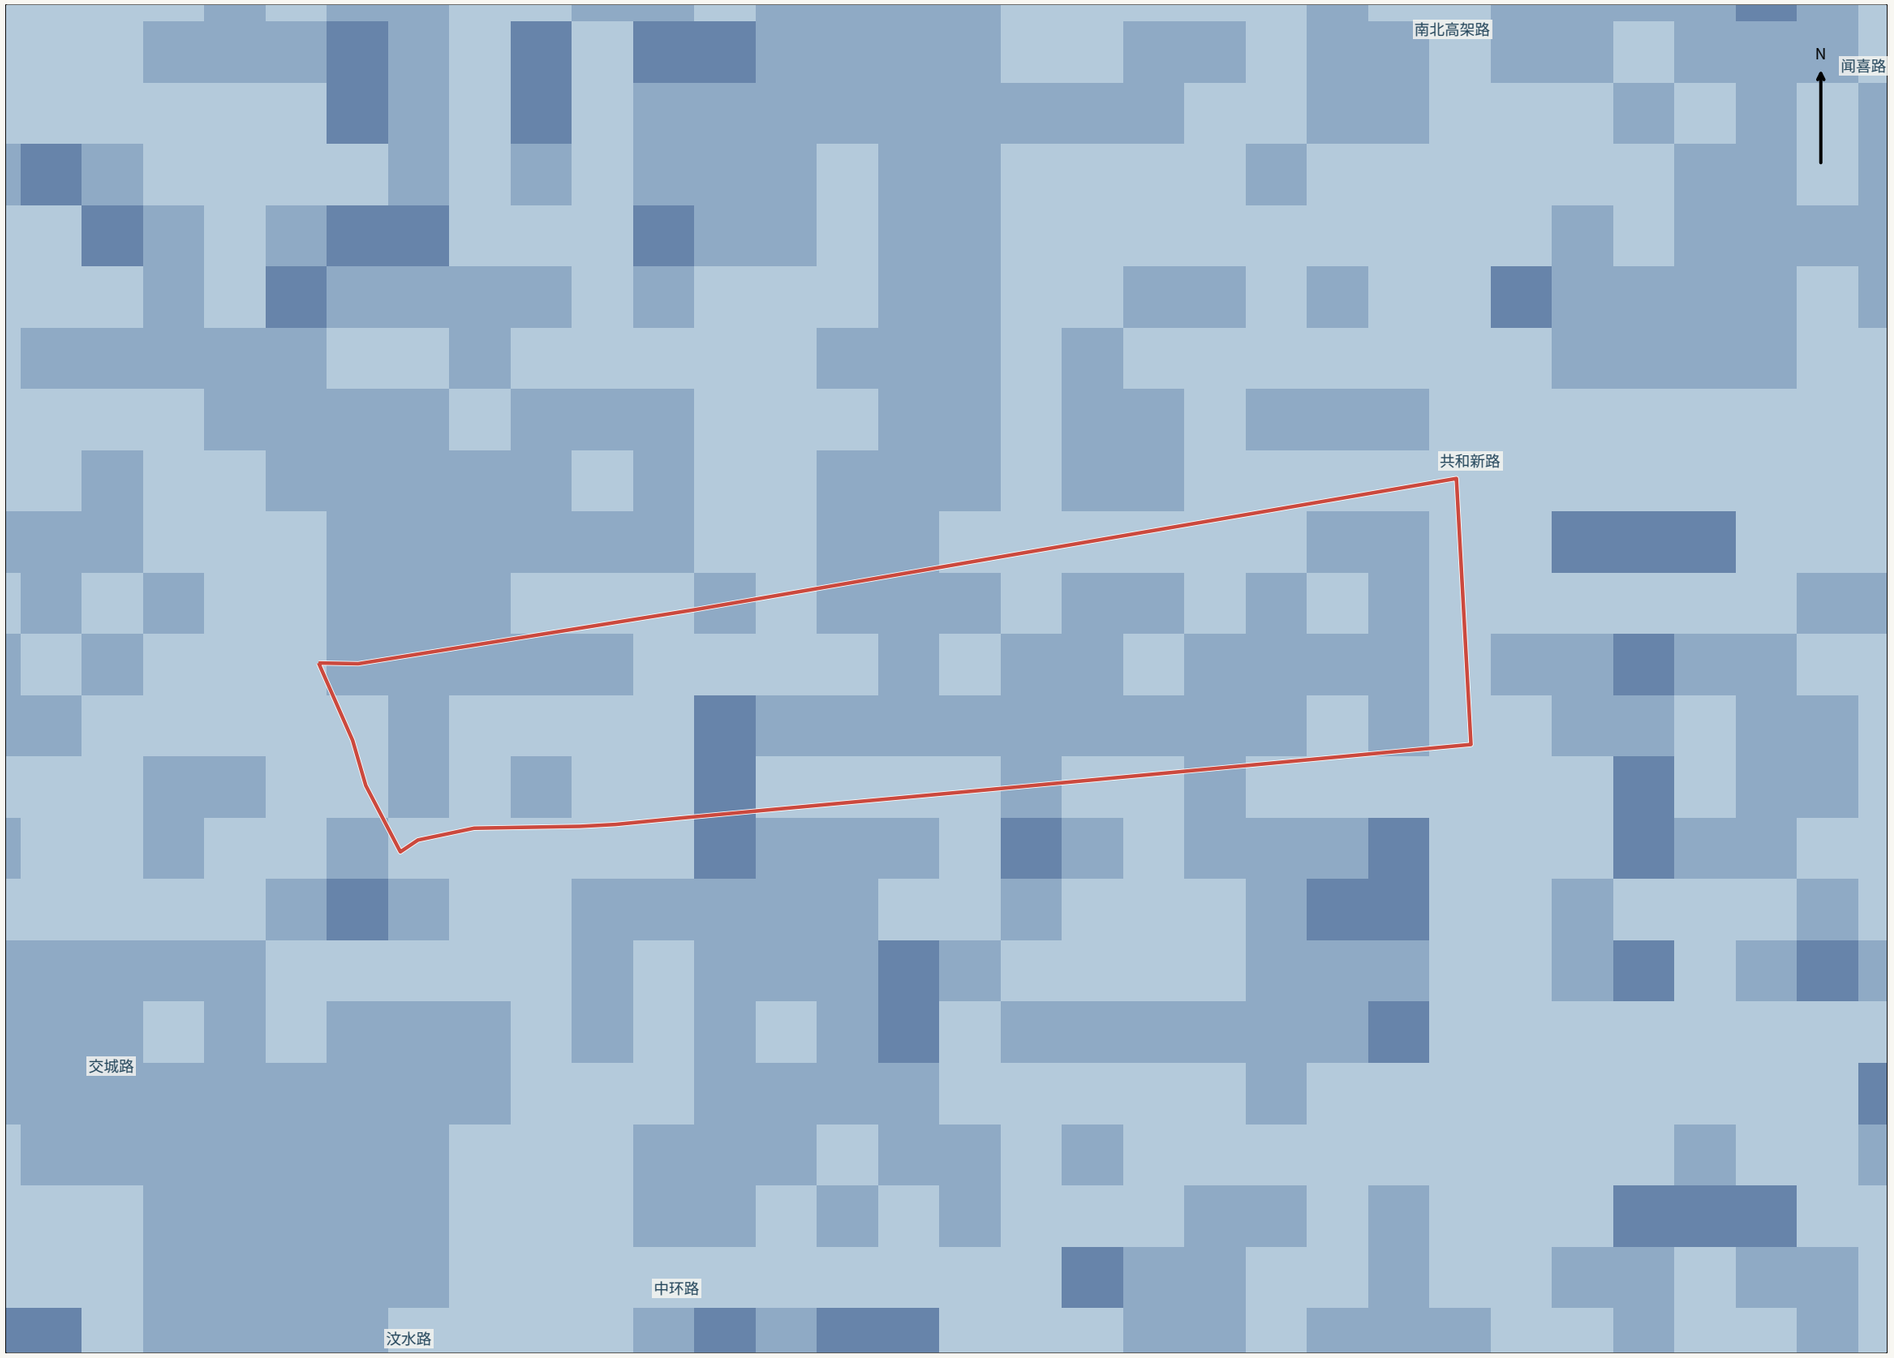

图例 / LEGEND

- 0 – 3
- 3 – 6
- 6 – 12
- 12 – 24
- 24 – 48
- 核心设计范围 / Design Site

主要发现 / FINDINGS

- 100m真实几何统计；视图内736个单元
- 有效736；中位值2.97

指标与方法 / METHOD

m^3/m^2，估高体量代理，非容积率。采用与全域相同固定分级；只是局部放大视图，不将设计线变成强制统计裁切。 m^3/m^2；所有高度均非测绘，非容积率。

地块现状与问题

设计区估高体量代理3.25米³/米²，周边2.95。局部高值可能主要由建筑基底占用造成，现有估高不足以支持真实高度梯度或容积率判断。

区域协同关系

应把地块建筑边缘、主街界面和近邻开敞空间一起研究，避免将粗略体量图直接转化为单侧增高或压低的设计要求。

改善方向

补测层数、面积、结构及现状用途，比较存量利用、界面修补与公共空间释放方案；以日照、通行和周边承载校核体量安排，不沿模型高值线直接划分建设任务。

A3｜1:10,011.90｜EPSG:32651｜设计66.0948ha｜周边　研究区内500米环带；可达比例为步行路段长度，非人口覆盖。

来源沿用原图：© OpenStreetMap contributors / Overture；ESA、Copernicus、EC-JRC、USGS、WorldPop。三段说明区分现状证据与研究建议。

R03 已映射土地功能混合｜200米

Mapped land-function area diversity

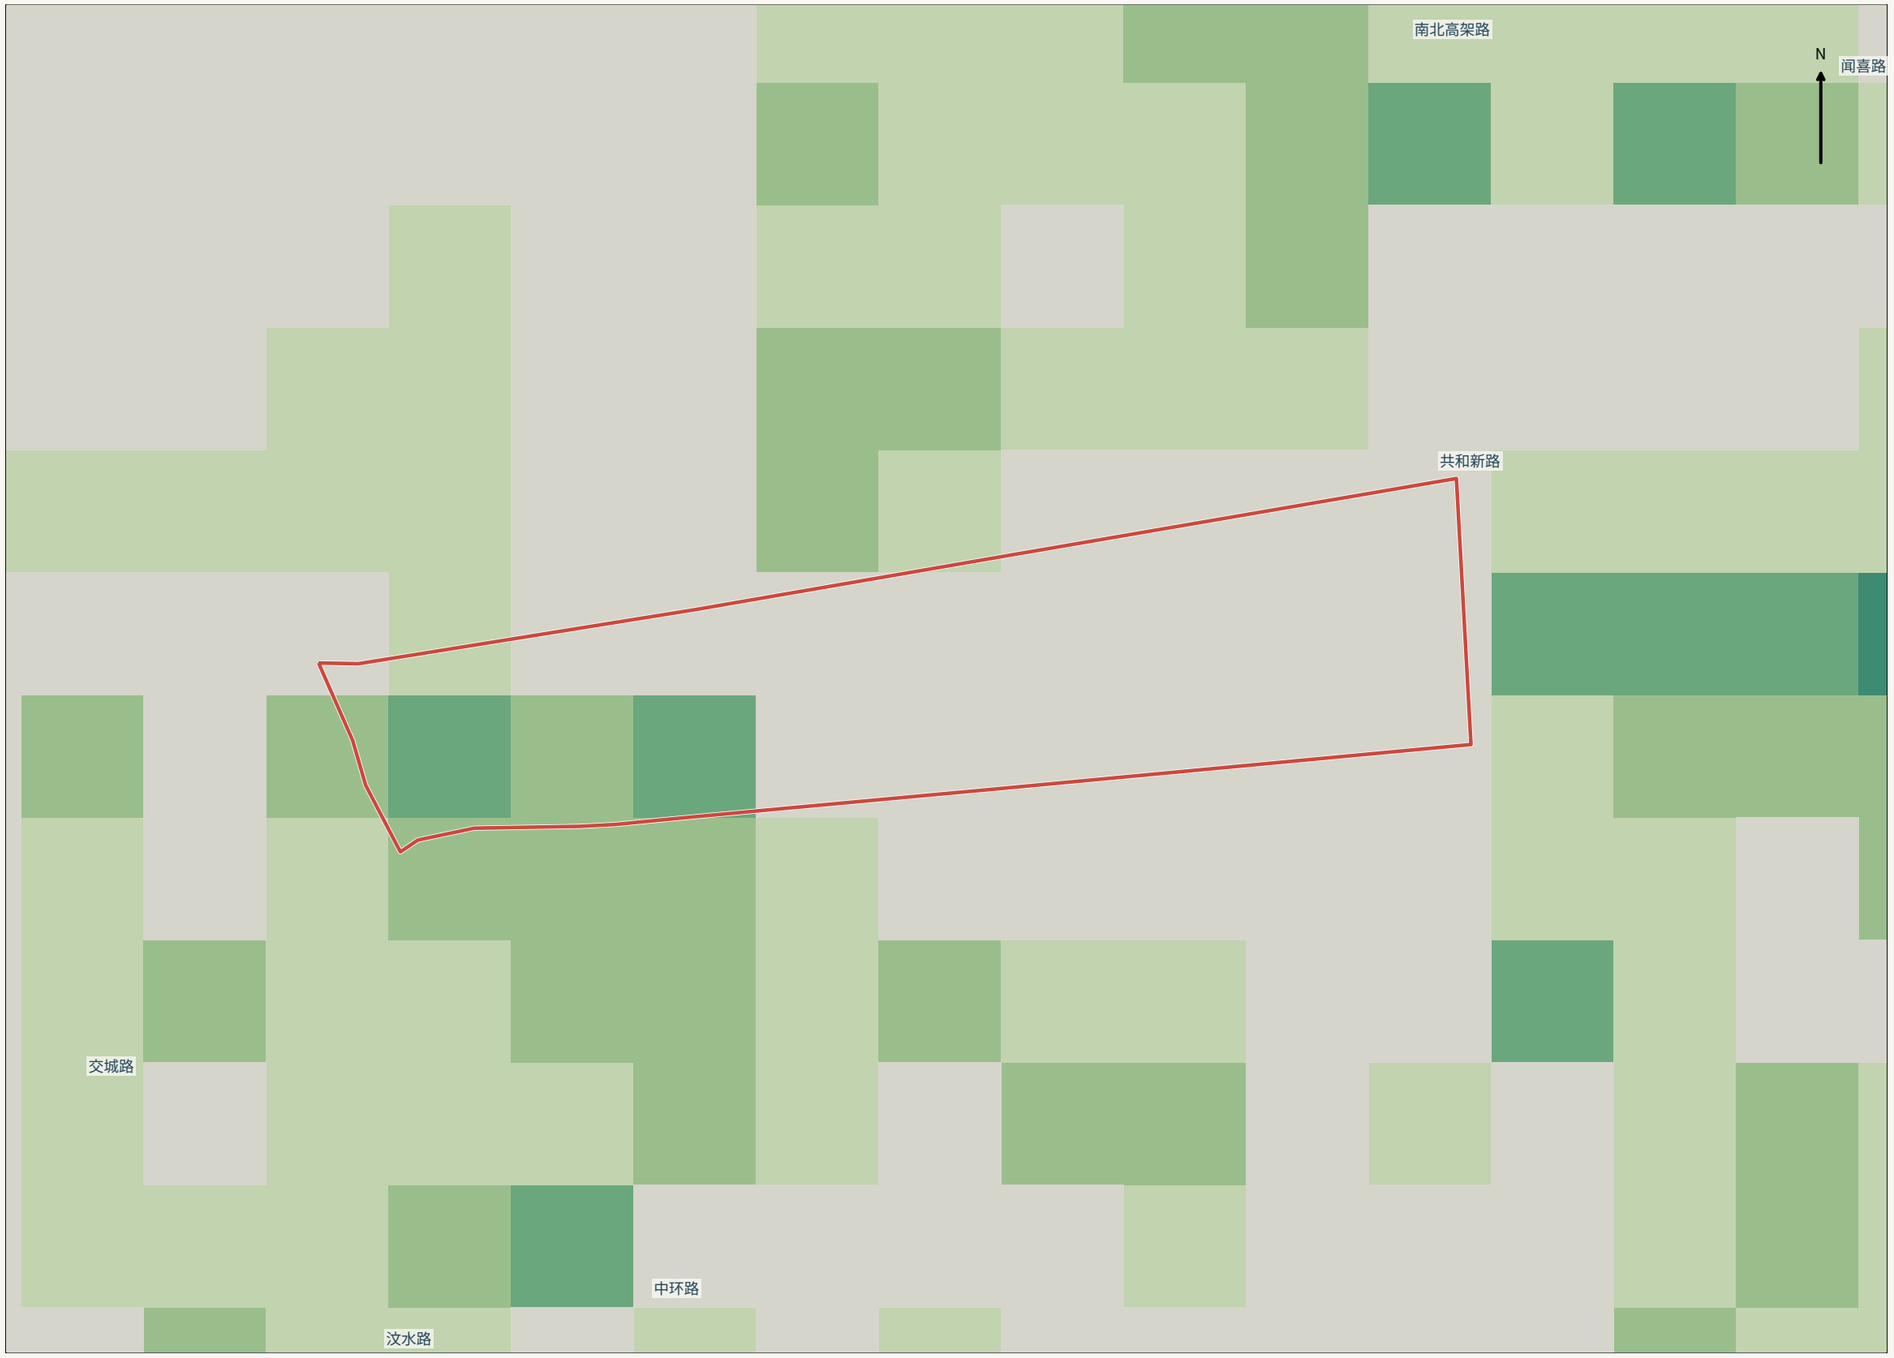

图例 / LEGEND

- 0 – 0.2
- 0.2 – 0.4
- 0.4 – 0.6
- 0.6 – 0.8
- 0.8 – 1
- 资料/有效覆盖不足，未计算
- 核心设计范围 / Design Site

主要发现 / FINDINGS

• 200m真实几何统计；视图内204个单元

• 有效107；中位值0.152

•
全域已知功能占比仍约52.33%；低覆盖单元不计算

指标与方法 / METHOD

H(已映射功能面积)/ln(8)；已知功能比例≥5
0%。采用与全域相同固定分级；只是局部放大视图，不将设计线变成强制统计裁切。 未知用地不当已知类别；已知比例<50%留空，另有剔除在建类敏感性。

地块现状与问题

触及地块的29个200米图示单元仅10个具有有效混合度；地块内功能证据覆盖21.2%。局部空值首先是证据不足，不能确定为单功能片区。

区域协同关系

周边可见居住、商业和公共服务功能，地块的改善应关注这些功能能否经公共路径相互服务，而不是以红线为界重复配置全部业态。

改善方向

逐建筑和首层补查用途、开放时间、经营与人群活动，沿实际可达节点评估互补服务及分时共享；先验证需求，再确定功能组合，不为提高指数而混合配置。

A3｜1:10,011.90｜EPSG:32651｜设计66.0948ha｜周边　研究区内500米环带；可达比例为步行路段长度，非人口覆盖。
来源沿用原图：© OpenStreetMap contributors / Overture；ESA、Copernicus、EC-JRC、USGS、WorldPop。三段说明区分现状证据与研究建议。

R04 车行路网与真实节点｜200米

Vehicle density and source-node junctions

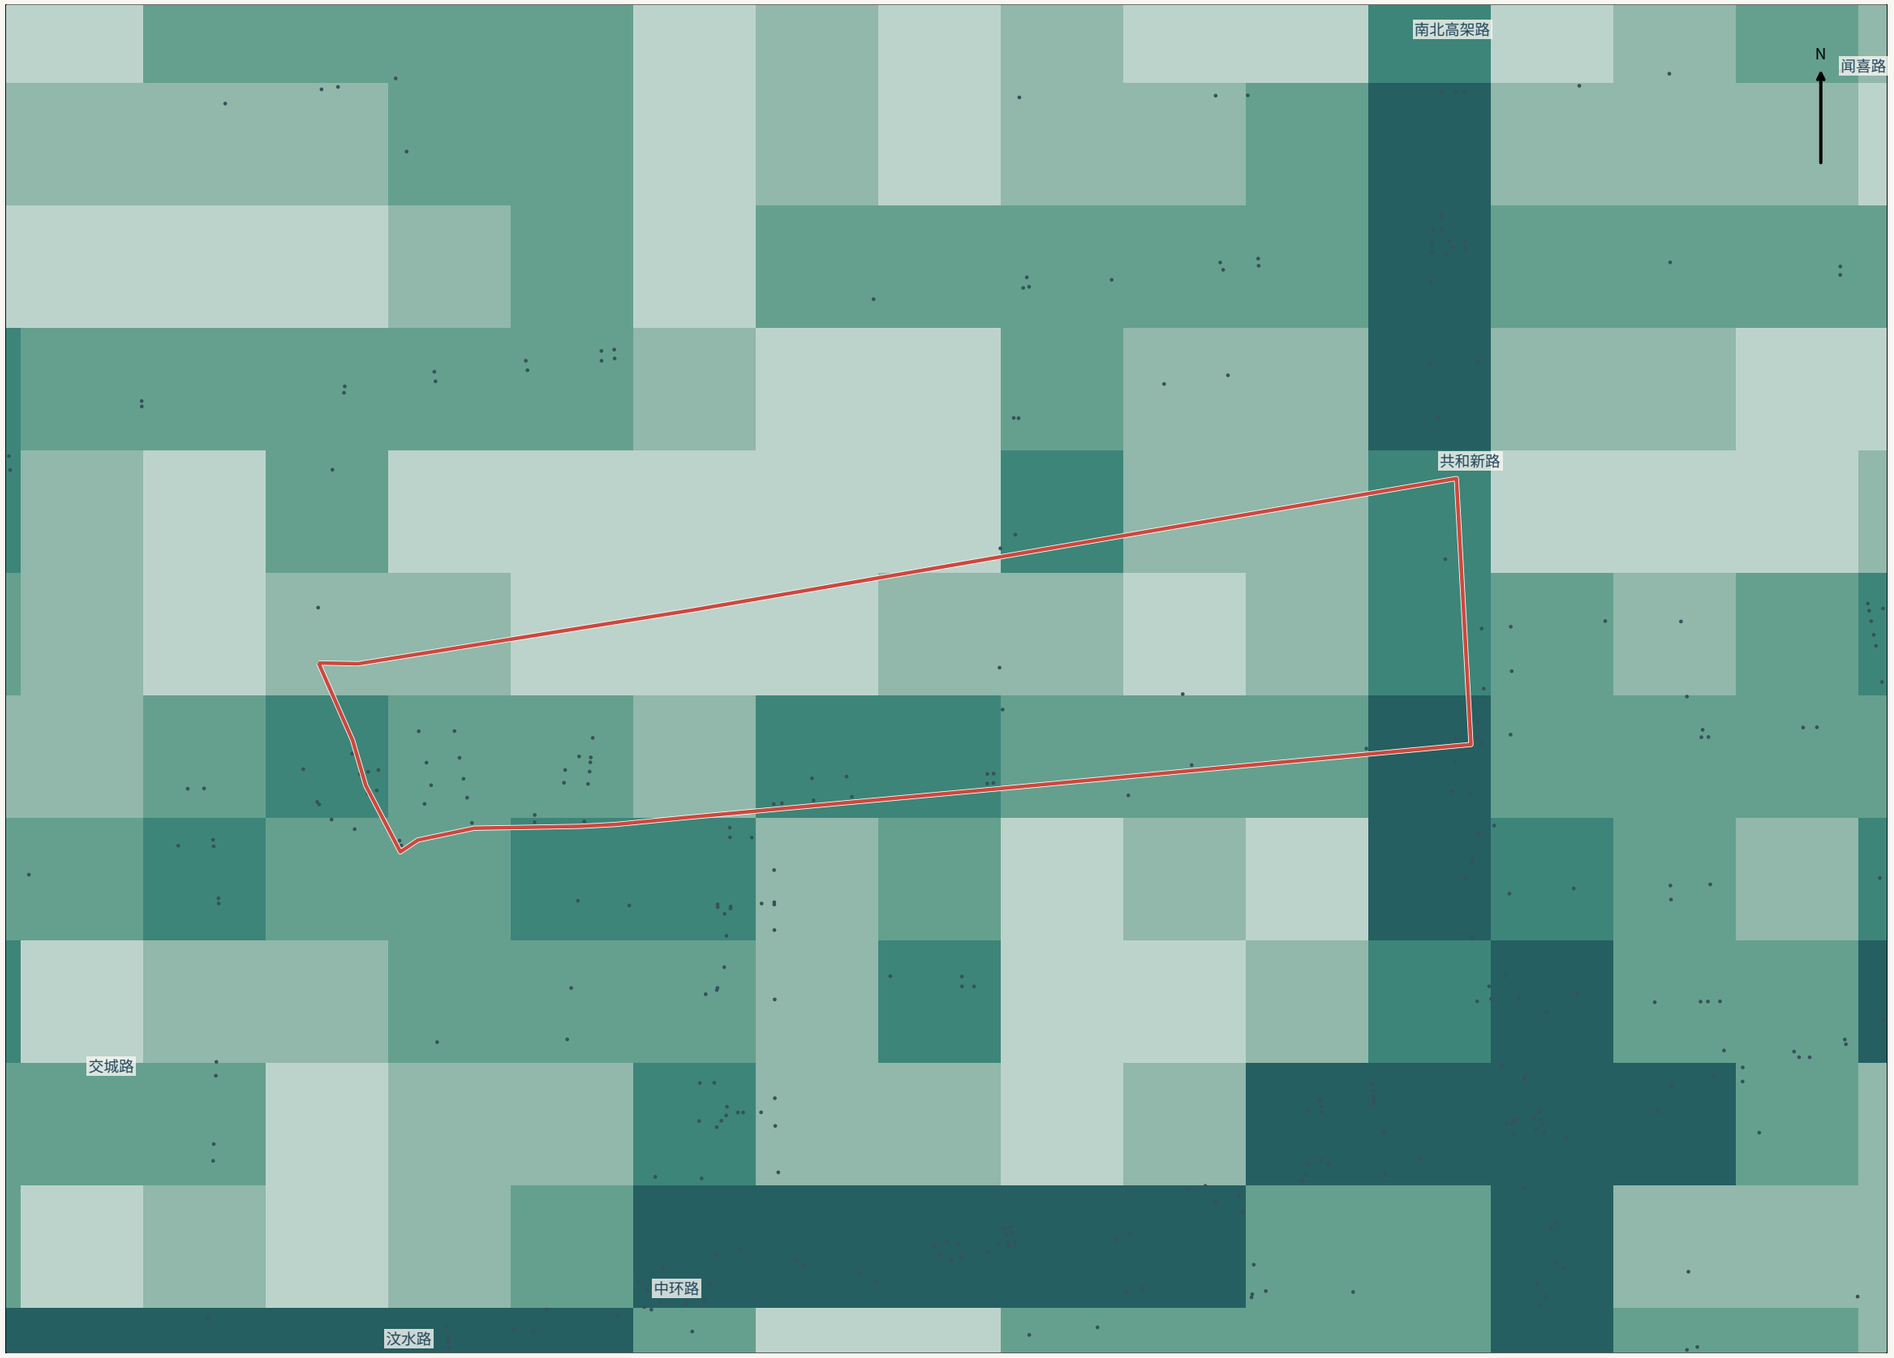

图例 / LEGEND

- 0 – 5
- 5 – 10
- 10 – 20
- 20 – 35
- 35 – 73
- 真实源节点车行度≥3
- 核心设计范围 / Design Site

主要发现 / FINDINGS

- 200m真实几何统计；视图内204个单元
- 有效204；中位值10

指标与方法 / METHOD

km / km²，双幅源道路分计。采用与全域相同固定分级；只是局部放大视图，不将设计线变成强制统计裁切。 只保留真实源拓扑；不把高架上下交点当路口。

地块现状与问题

地块车行源线密度13.90公里/平方公里，并有48处真实源节点。局部图强调节点位置，仍不能说明主路、高架上下空间和内部道路具有同等通行条件。

区域协同关系

江场西路、万荣路与共和新路等界面连接内部与区域道路，应将边界路口和跨街联系作为共同研究对象，区分区域车流和地块日常到达。

改善方向

逐个复核关键路口、过街与入口，协调人车分流、后勤及无障碍路线；只有在真实通行和交通安全条件得到证明后，才进一步设计新的连接。

A3｜1:10,011.90｜EPSG:32651｜设计66.0948ha｜周边　研究区内500米环带；可达比例为步行路段长度，非人口覆盖。

来源沿用原图：© OpenStreetMap contributors / Overture；ESA、Copernicus、EC-JRC、USGS、WorldPop。三段说明区分现状证据与研究建议。

R05 商业观察密度｜200米

Observed commercial POI density

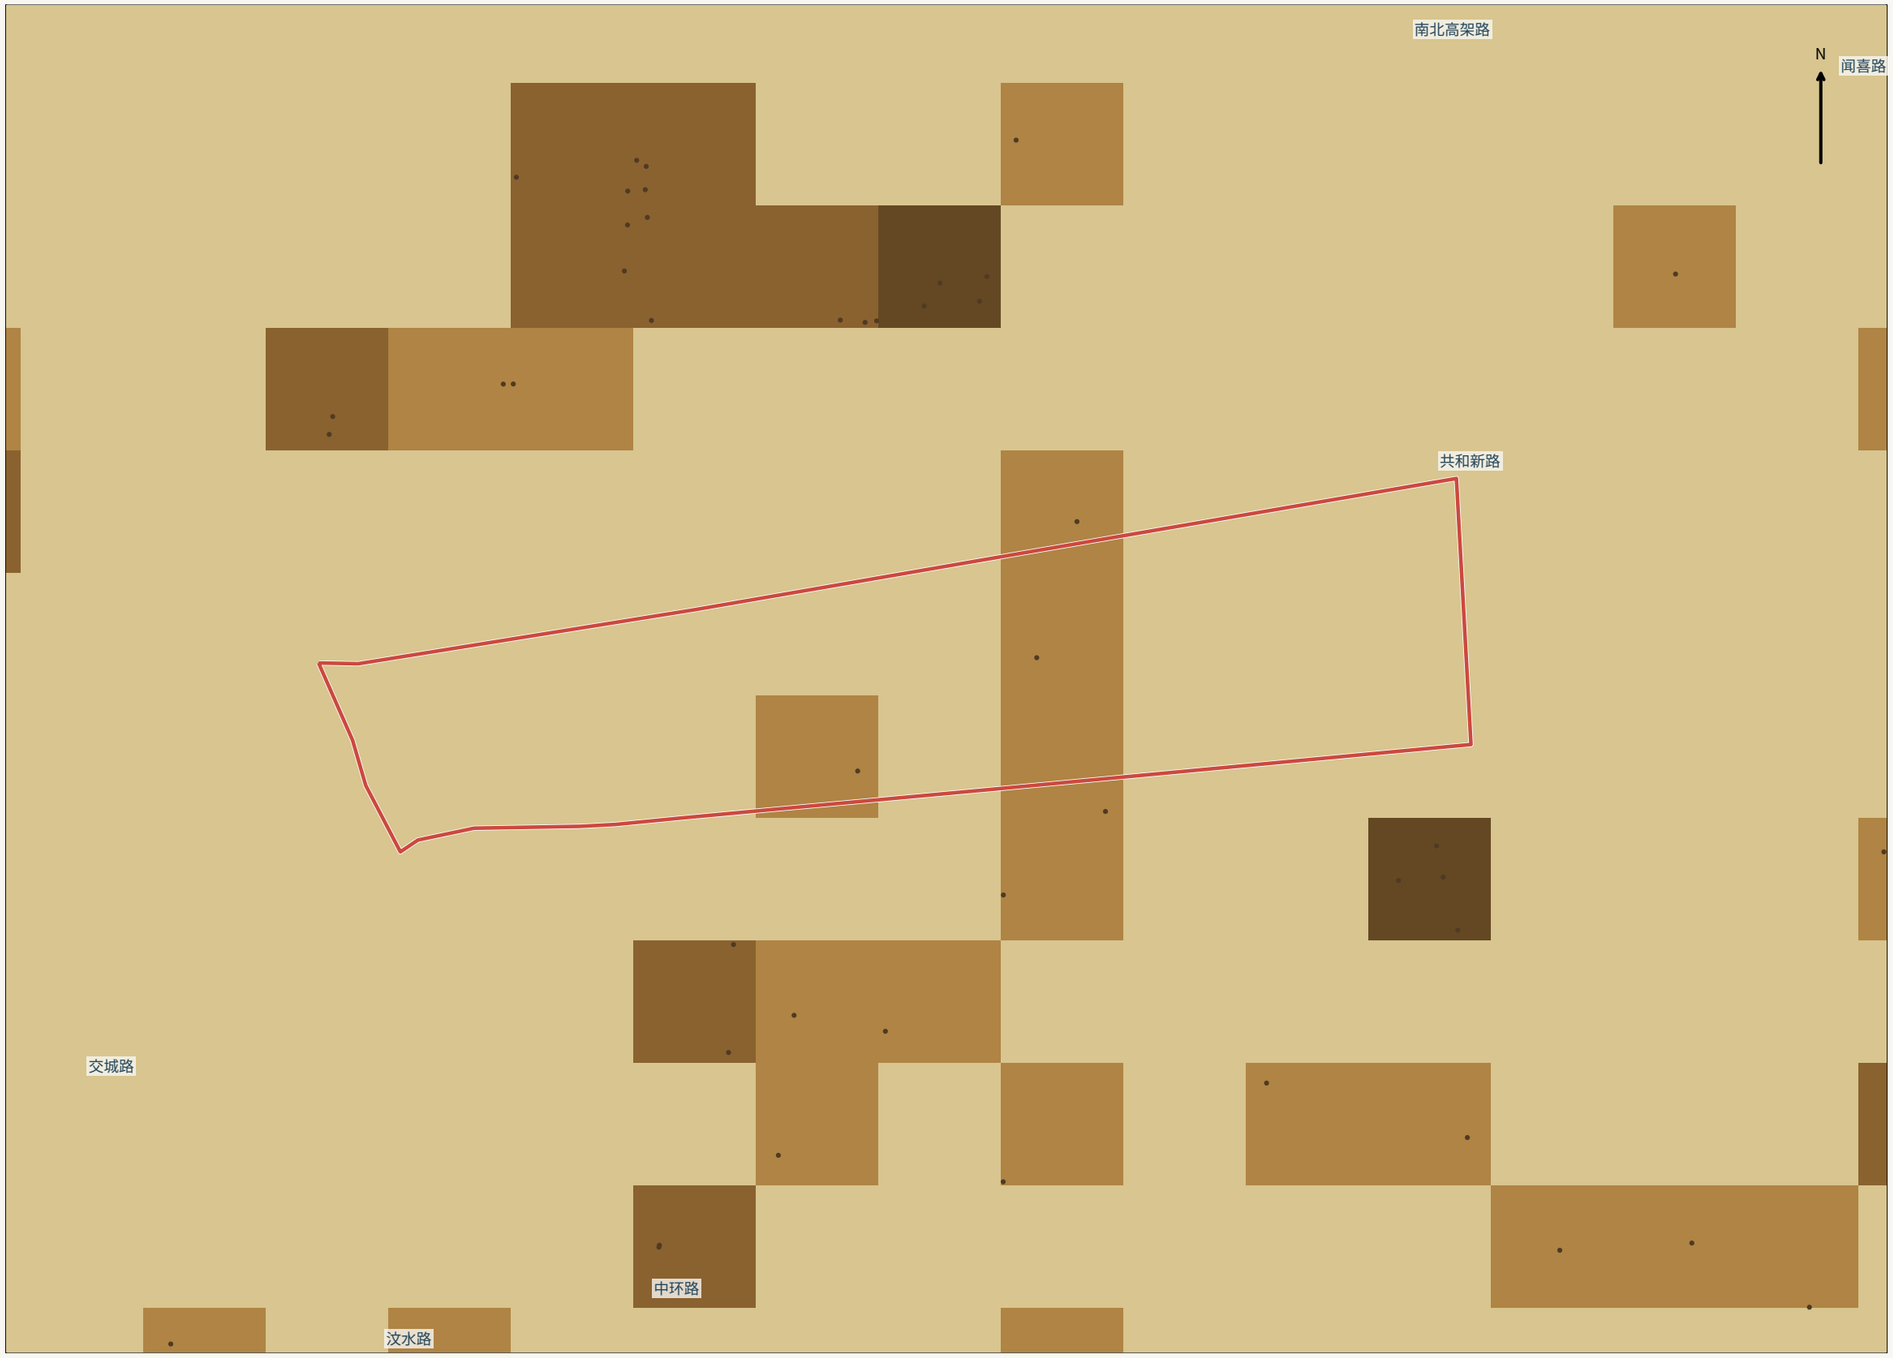

图例 / LEGEND

- 0 – 10
- 10 – 25
- 25 – 50
- 50 – 100
- 100 – 250
- 已映射商业观察点
- 核心设计范围 / Design Site

主要发现 / FINDINGS

- 200m真实几何统计；视图内204个单元
- 有效204；中位值0
- 局部观察点46；零格不能证明无商业

指标与方法 / METHOD

已映射商业POI / km^2；零值不表示无商业。采用与全域相同固定分级；只是局部放大视图，不将设计线变成强制统计裁切。 观察点密度，不是客流/就业；带宽100/200/400m对照见报告。

地块现状与问题

地块内商业观察点仅2条，密度图对数据遗漏十分敏感。空格和低值不等于没有门店，也不支持把某个空白街角认定为商业开发机会。

区域协同关系

周边环带记录24条商业观察点。地块可沿江场西路—万荣路衔接现有服务，重点研究互补、共享与便捷进入，不在内部复制封闭商业中心。

改善方向

补查沿街店铺、空置和客流，分清经营弱与记录少；有实际需求时先利用既有首层进行小规模、可调整的业态试点，再依据运营和居民反馈完善。

A3｜1:10,011.90｜EPSG:32651｜设计66.0948ha｜周边　研究区内500米环带；可达比例为步行路段长度，非人口覆盖。
来源沿用原图：© OpenStreetMap contributors / Overture；ESA、Copernicus、EC-JRC、USGS、WorldPop。三段说明区分现状证据与研究建议。

R06 公共环境改善机会｜100米

Research amenity-improvement screening

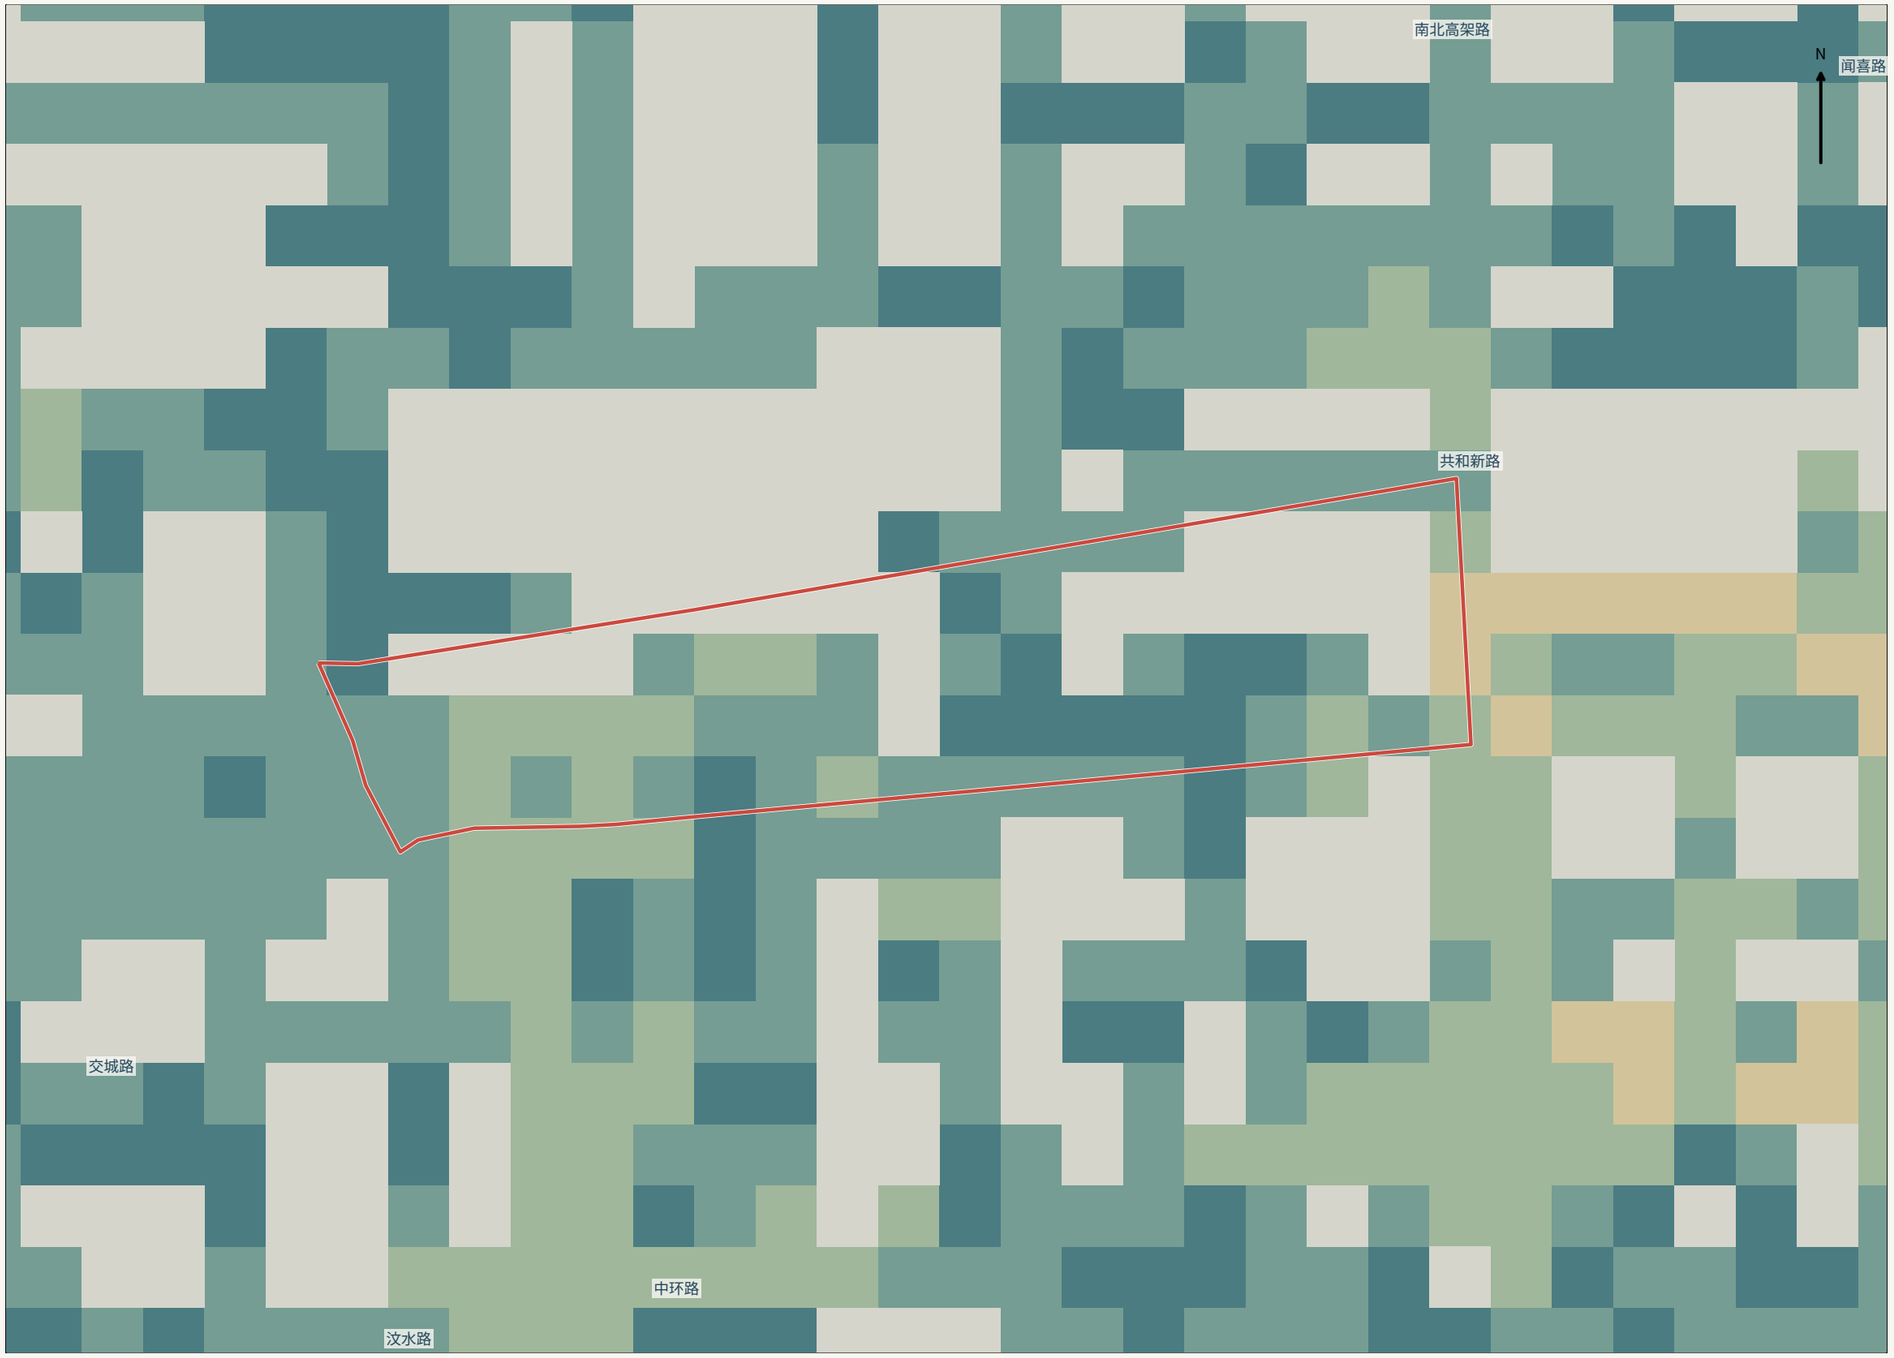

图例 / LEGEND

- 0 – 0.2
- 0.2 – 0.4
- 0.4 – 0.6
- 0.6 – 0.8
- 0.8 – 1
- 资料/有效覆盖不足，未计算
- 核心设计范围 / Design Site

主要发现 / FINDINGS

- 100m真实几何统计；视图内736个单元
- 有效492；中位值0.518

指标与方法 / METHOD

三项等权百分位均值，非法定更新风险。采用与全域相同固定分级；只是局部放大视图，不将设计线变成强制统计裁切。 V2三项等权体系沿用；不是政府更新、拆迁或建设名单。

地块现状与问题

地块有效初筛均值0.477，并非全域突出高值；约68.7%面积有分数。局部高值可帮助安排走访，但缺值和源数据稀疏限制了排序解释。

区域协同关系

设计地块与周边的改造应共享问题清单，优先选择能同时改善街道通行、绿化和日常服务接入的接口，避免以红线分割连续的公共环境问题。

改善方向

实查高值单元后，把可实施的入口、遮荫、休憩和服务补点组合成分期行动；用权属、成本、需求与运营反馈校核顺序，不以初筛分数直接替代项目决策。

A3｜1:10,011.90｜EPSG:32651｜设计66.0948ha｜周边　研究区内500米环带；可达比例为步行路段长度，非人口覆盖。
来源沿用原图：© OpenStreetMap contributors / Overture；ESA、Copernicus、EC-JRC、USGS、WorldPop。三段说明区分现状证据与研究建议。

R07 数据问题与改善机会｜100米

Evidence issues and improvement screening

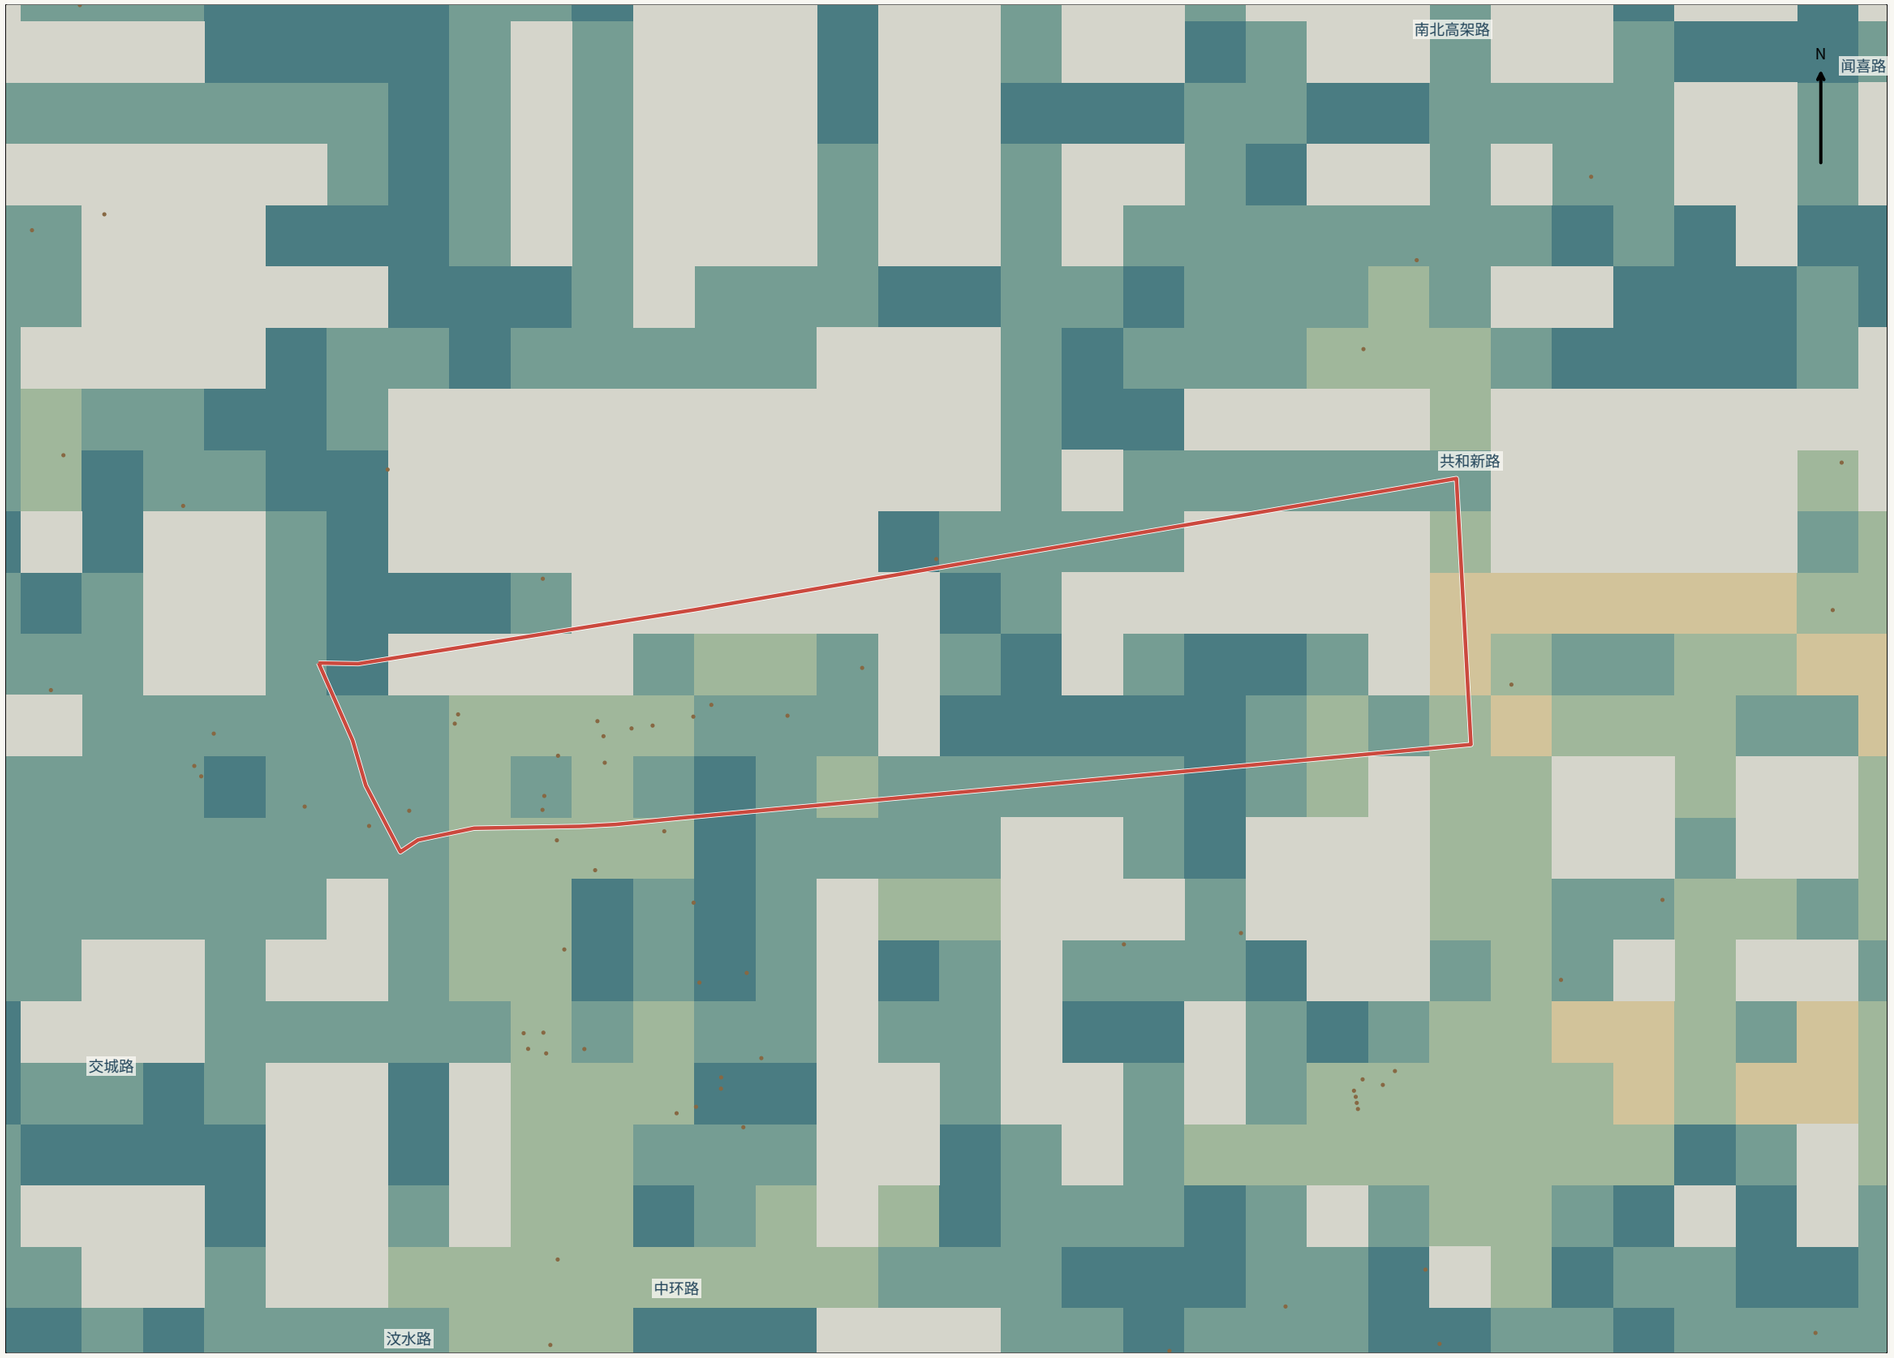

图例 / LEGEND

- 0 – 0.2
- 0.2 – 0.4
- 0.4 – 0.6
- 0.6 – 0.8
- 0.8 – 1
- 资料/有效覆盖不足，未计算
- 原端点复核位置（非确认错误）
- 核心设计范围 / Design Site

主要发现 / FINDINGS

- 100m真实几何统计；视图内736个单元
- 有效492；中位值0.518

指标与方法 / METHOD

三项等权百分位均值，非法定更新风险。采用与全域相同固定分级；只是局部放大视图，不将设计线变成强制统计裁切。 点线面问题保留原位置，不是所有问题格网化。

地块现状与问题

地块局部需复核15处源端点和2处路建叠置。图中标记指向数据或空间问题的核查位置，不是已经确认的实体缺陷。

区域协同关系

复核路线应跨越设计边界，与江场西路、万荣路及高架界面一起检查；需要区分真实门禁、分层道路、数据断点和估宽偏差，避免只追求图面线网闭合。

改善方向

按位置建立照片、通行条件、实宽与责任主体台账；确认后再处理入口、过街和连续人行等可实施问题，先修正误判记录，不依据示意坡度安排工程。

A3｜1:10,011.90｜EPSG:32651｜设计66.0948ha｜周边　研究区内500米环带；可达比例为步行路段长度，非人口覆盖。
来源沿用原图：© OpenStreetMap contributors / Overture；ESA、Copernicus、EC-JRC、USGS、WorldPop。三段说明区分现状证据与研究建议。

R08 2025模型人口｜原生约1公里

Native WorldPop population model 2025

图例 / LEGEND

- 0 – 1e+04
- 1e+04 – 2e+04
- 2e+04 – 4e+04
- 4e+04 – 8e+04
- 8e+04 – 1.72e+05
- 核心设计范围 / Design Site

主要发现 / FINDINGS

• 原生模型：48个AOI裁切格网

• 2025约1km /
2020约100m；不重新细分

指标与方法 / METHOD

模型人 / km²；两年份产品不可直接作人口变化。
原生人口单元保持不变；卫星与建筑只增加空间参照，不制造人口局部差异。 2025
ALPHA模型，非普查实测人口。

地块现状与问题

设计区触及7个原生约1公里人口单元，内部色差不是楼栋级人口差异。细部公共空间和服务容量不能直接由这幅局部放大图确定。

区域协同关系

地块模型密度约2.10万人/平方公里，全域约2.07万；宜作为片区协同背景，不能推断地块应独立承担多少新增设施。

改善方向

联合调查地块与邻近街区的现况居住、就业和到访人群，按实际时段配置共享空间与接入路线；模型保持原生尺度，不向100米网格分摊人口来制造精细结论。

A3｜1:10,011.90｜EPSG:32651｜设计66.0948ha｜周边　研究区内500米环带；可达比例为步行路段长度，非人口覆盖。
来源沿用原图：© OpenStreetMap contributors / Overture；ESA、Copernicus、EC-JRC、USGS、WorldPop。三段说明区分现状证据与研究建议。